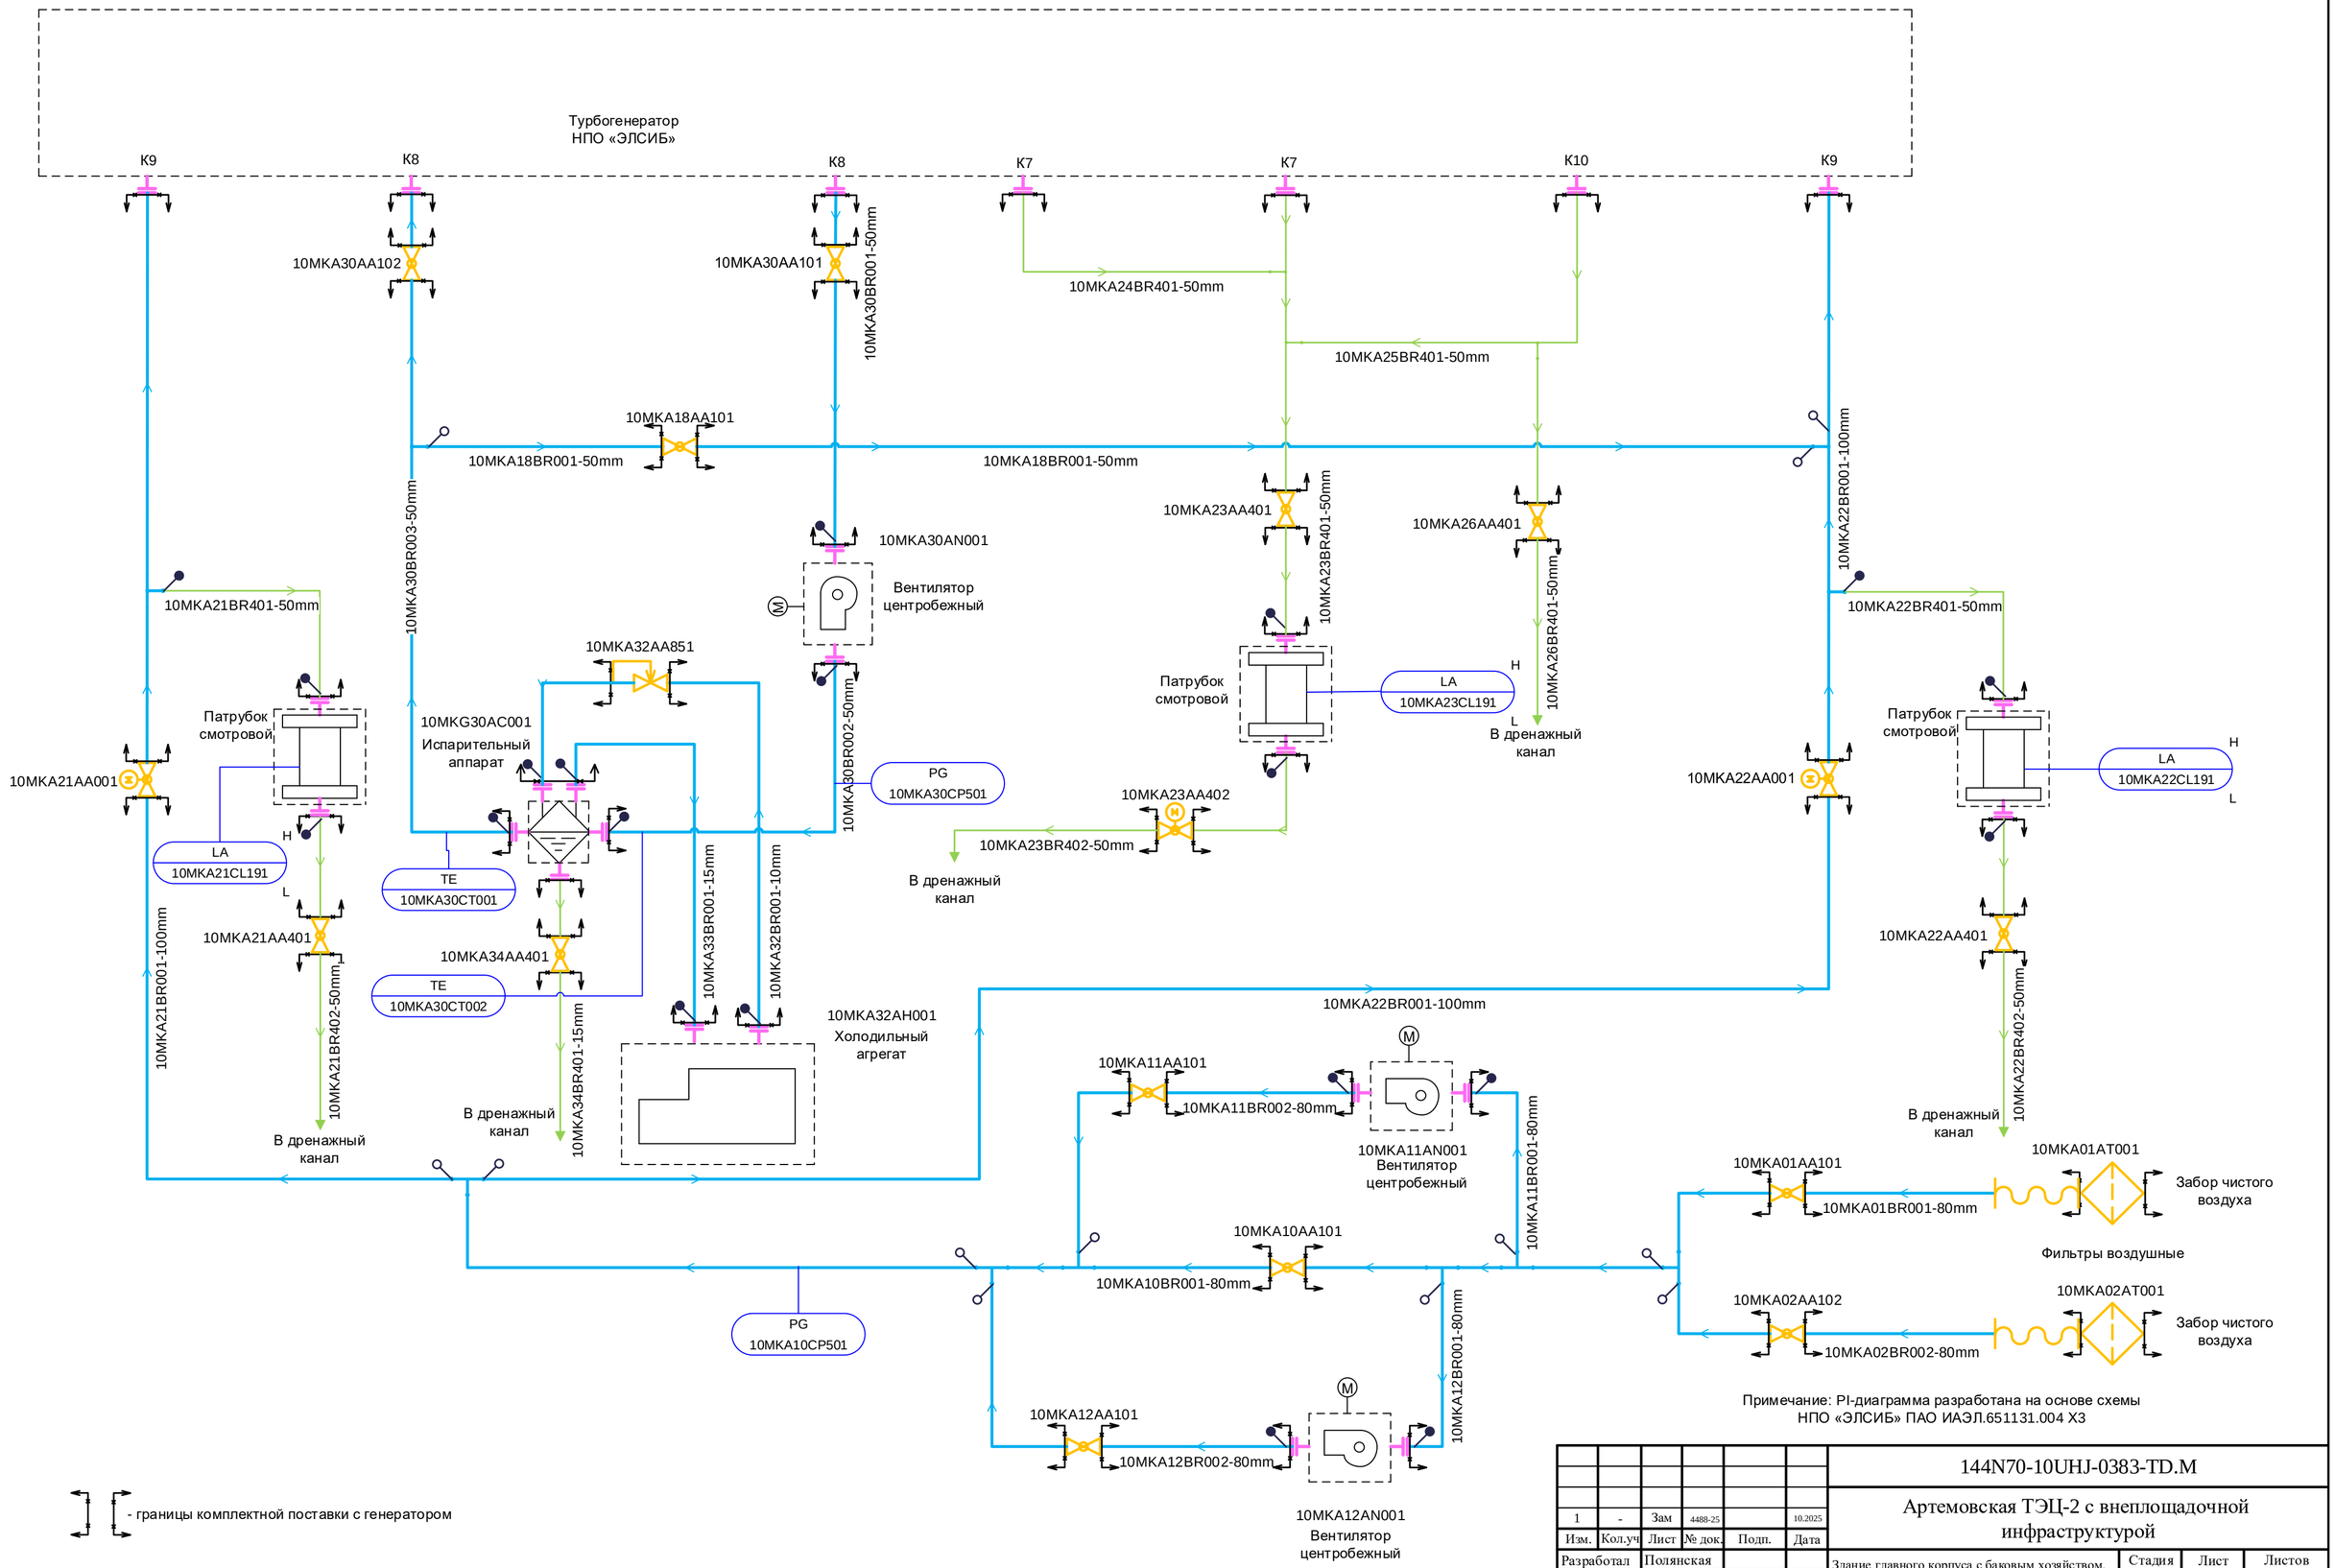

Примечание: PI-диаграмма разработана на основе схемы НПО «ЭЛСИБ» ПАО ИАЭЛ.651131.004 Х3

1	-	Зам	4488-25		10.2025	
Изм.	Кол.уч	Лист	№ док.	Подп.	Дата	
Разработал		Полянская				
Проверил		Смирнова				
Н. контр.		Черемушкина				

144N70-10UHJ-0383-TD.M

Артемовская ТЭЦ-2 с внеплощадочной инфраструктурой

Здание главного корпуса с баковым хозяйством. PI-диаграмма трубопроводов подпитки воздухом и влагоудаления турбогенератора.

PI-диаграмма трубопроводов подпитки воздухом и влагоудаления турбогенератора. Система МКА. Блок 1.

Стадия	Лист	Листов
Р	2	

АКЦИОНЕРНОЕ ОБЩЕСТВО ИНСТИТУТ ТЕПЛОЭЛЕКТРОПРОЕКТ г. МОСКВА

Согласовано

ОАСУ

Взам. инв. №

Подпись и дата

Инв. № подл.

Формат А2