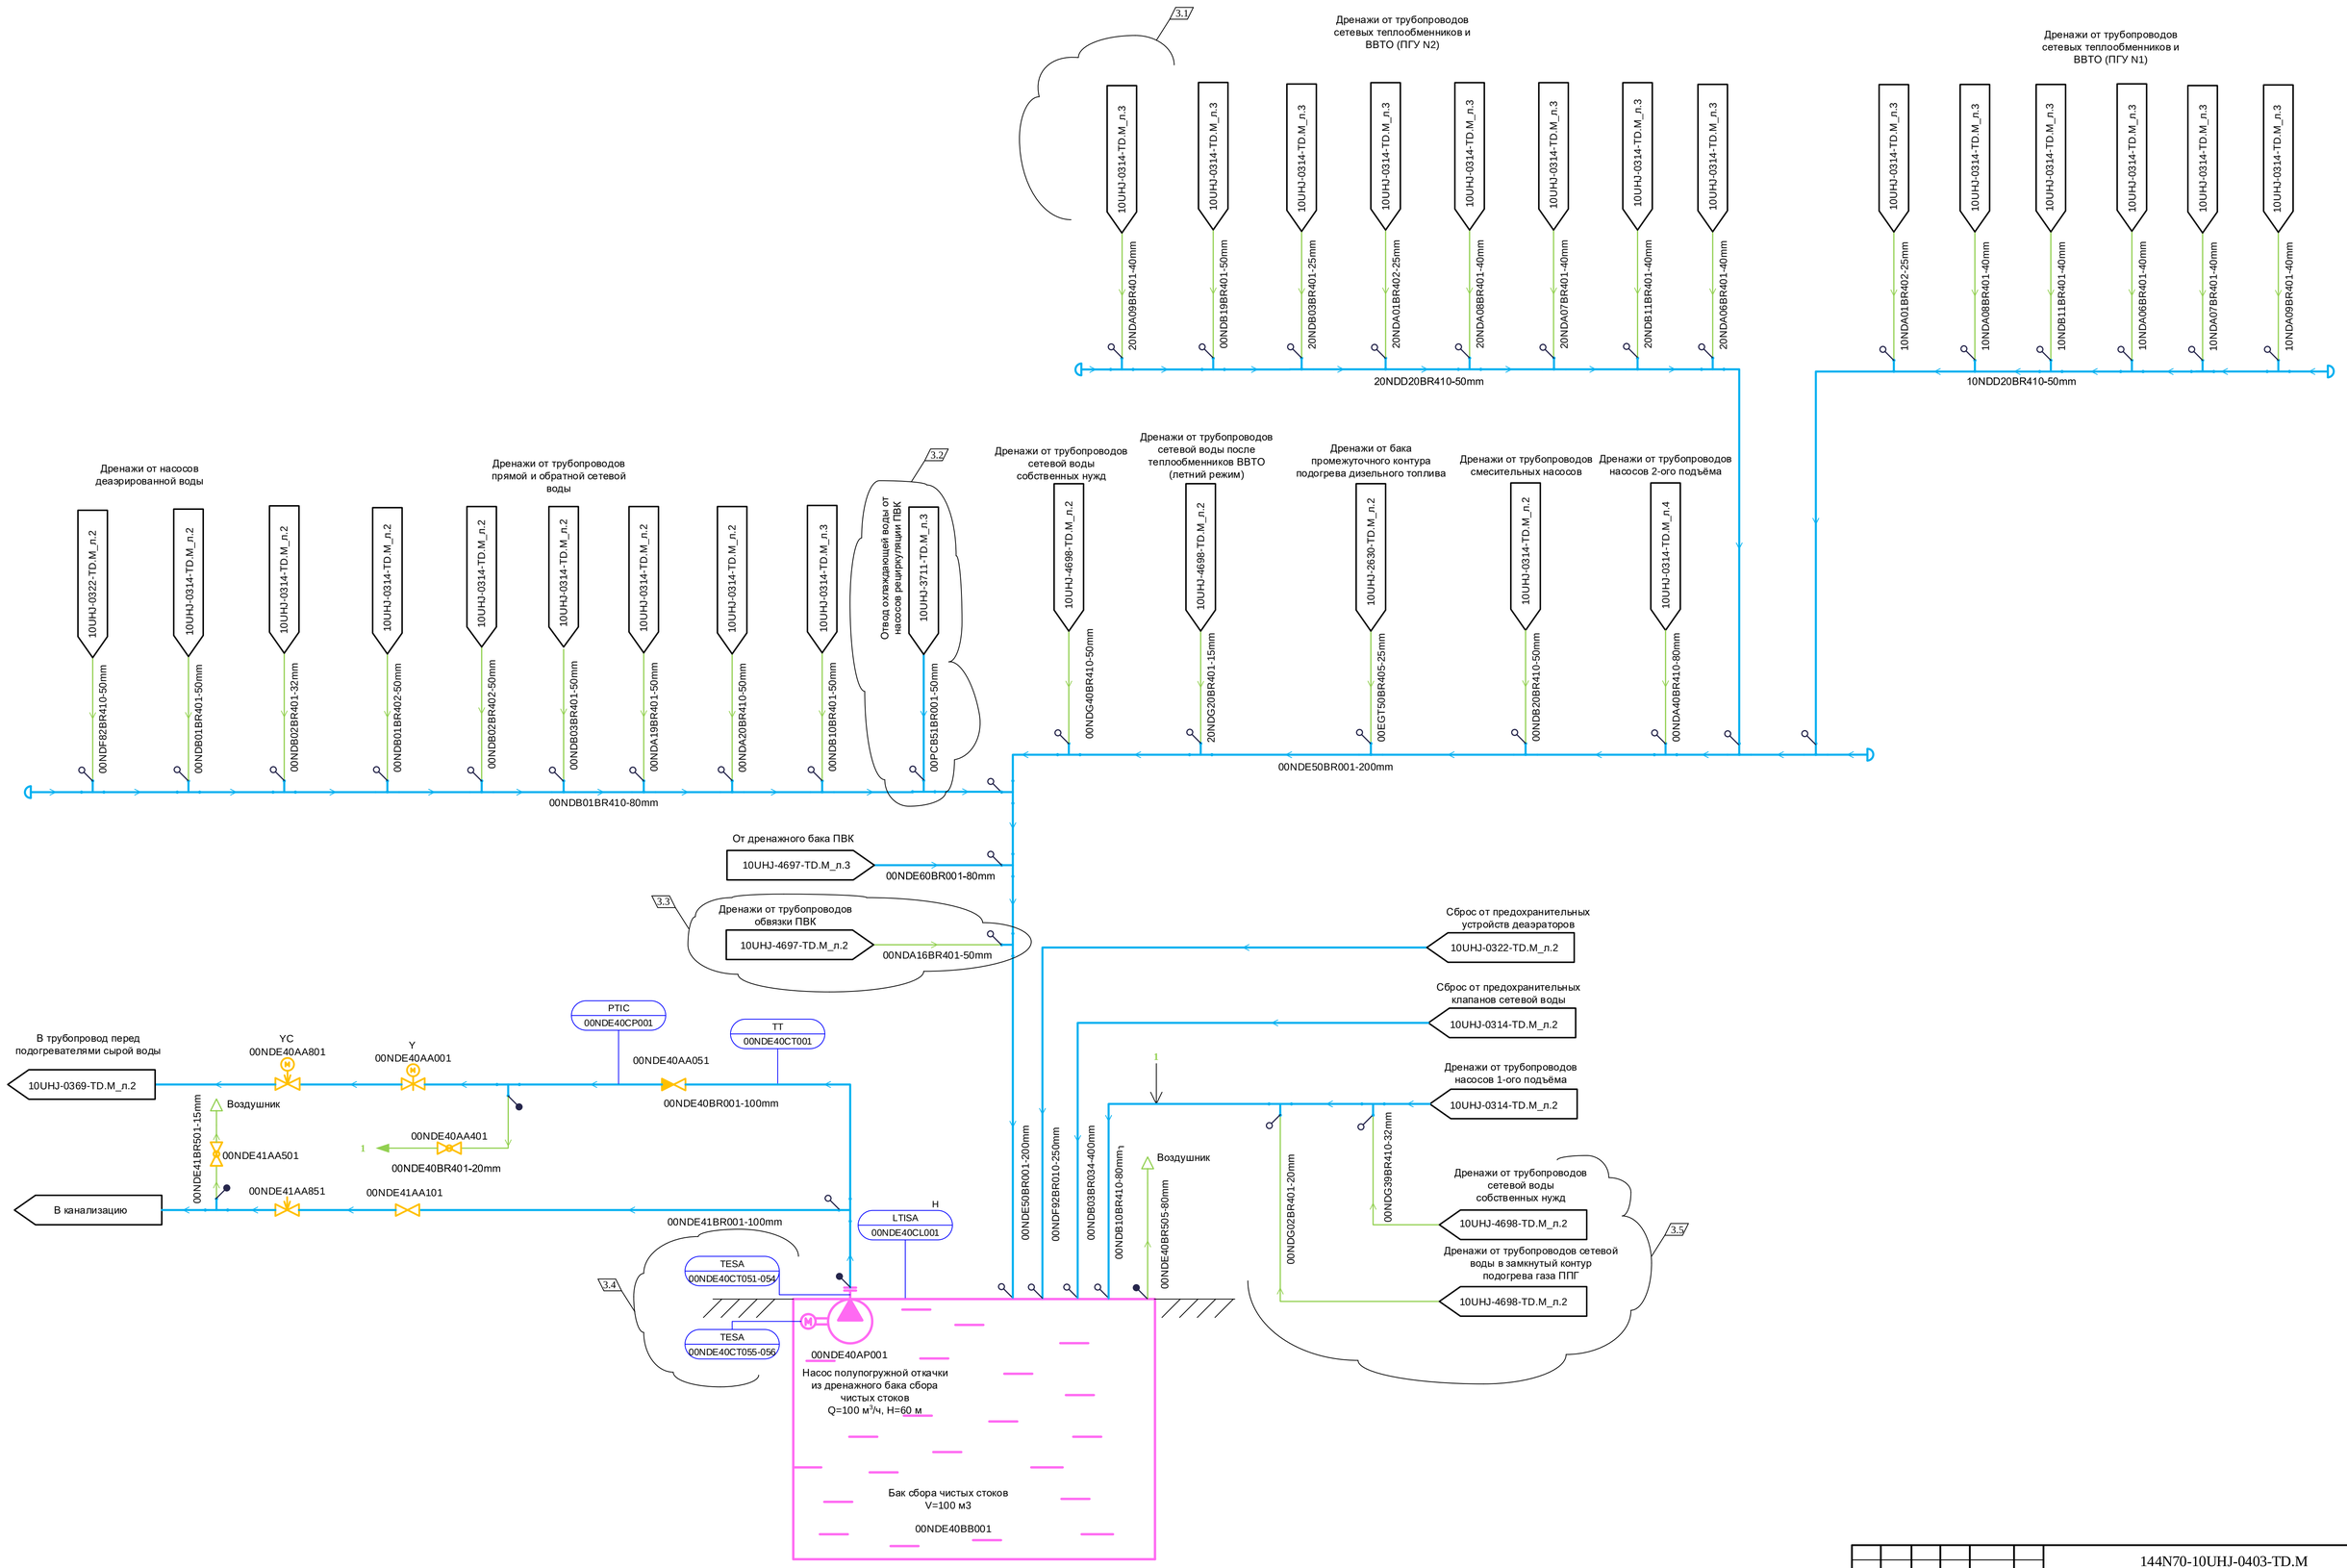

3	5	Зам.	6315-25		12.25	144N70-10UHJ-0403-TD.M
Изм.	Кол.уч	Лист	№ док.	Подп.	Дата	Строительство Артемовской ТЭЦ-2 с внеплощадной инфраструктурой
Разработал		Салищева				Здание главного корпуса с баковым хозяйством. PI-диаграмма трубопроводов сбора дренажей сетевой воды.
Проверил		Дёмина				Стадия: Р; Лист: 2; Листов:
Н. контр.		Черёмушкина				PI-диаграмма трубопроводов сбора дренажей сетевой воды. Система NDE, NDB, NDD

АКЦИОНЕРНОЕ ОБЩЕСТВО ИНСТИТУТ ТЕПЛОЭЛЕКТРОПРОЕКТ г. МОСКВА

Согласовано

Взам. инв. №

Подпись и дата

Инв. № подл.

Формат А1