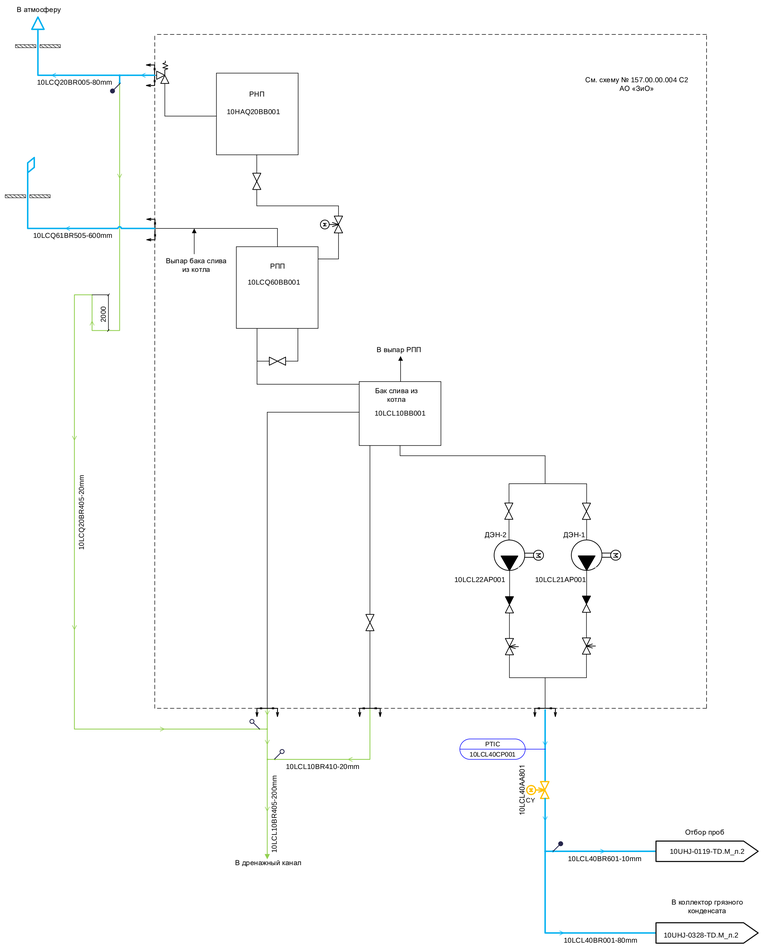

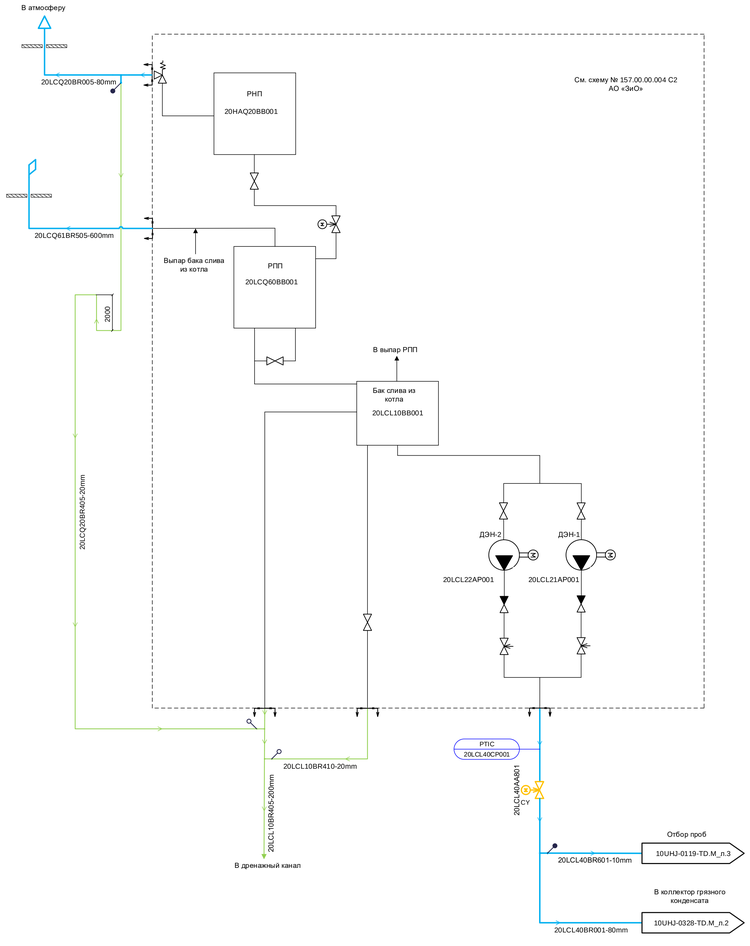

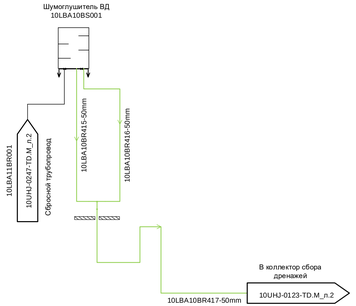

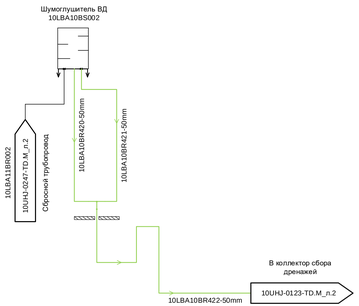

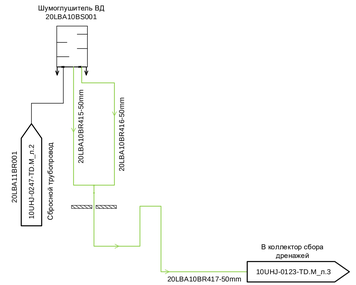

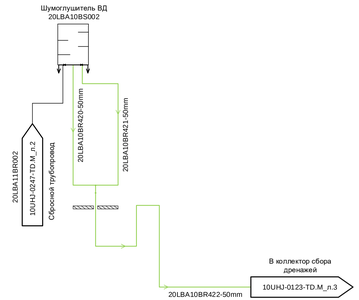

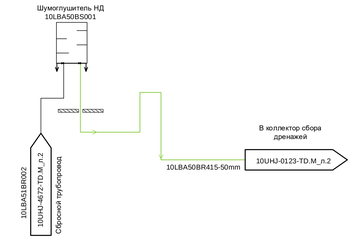

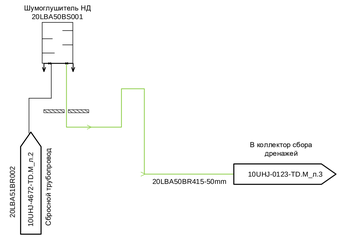

						144N70-10UHJ-0456-TD.M			
						Артемовская ТЭЦ-2 с внеплощадочной инфраструктурой			
Изм.	Кол.уч	Лист	№ док.	Подп.	Дата				
Разработал		Дроздов				Здание главного корпуса с бытовым хозяйством. PI-диаграмма дренажей, воздушников и вспомогательных трубопроводов котла.	Стадия	Лист	Листов
Проверил		Демина					Р	2	
Н. контр.		Астраханцев				PI-диаграмма дренажей, воздушников и вспомогательных трубопроводов котла.	ПОВТОРНОЕ ПРИМЕНЕНИЕ ТЕХЭНЕРГОПРОЕКТ АО СПб		

Согласовано

Взам. инв. №

Подпись и дата

Инв. № подл.

Формат А2х3