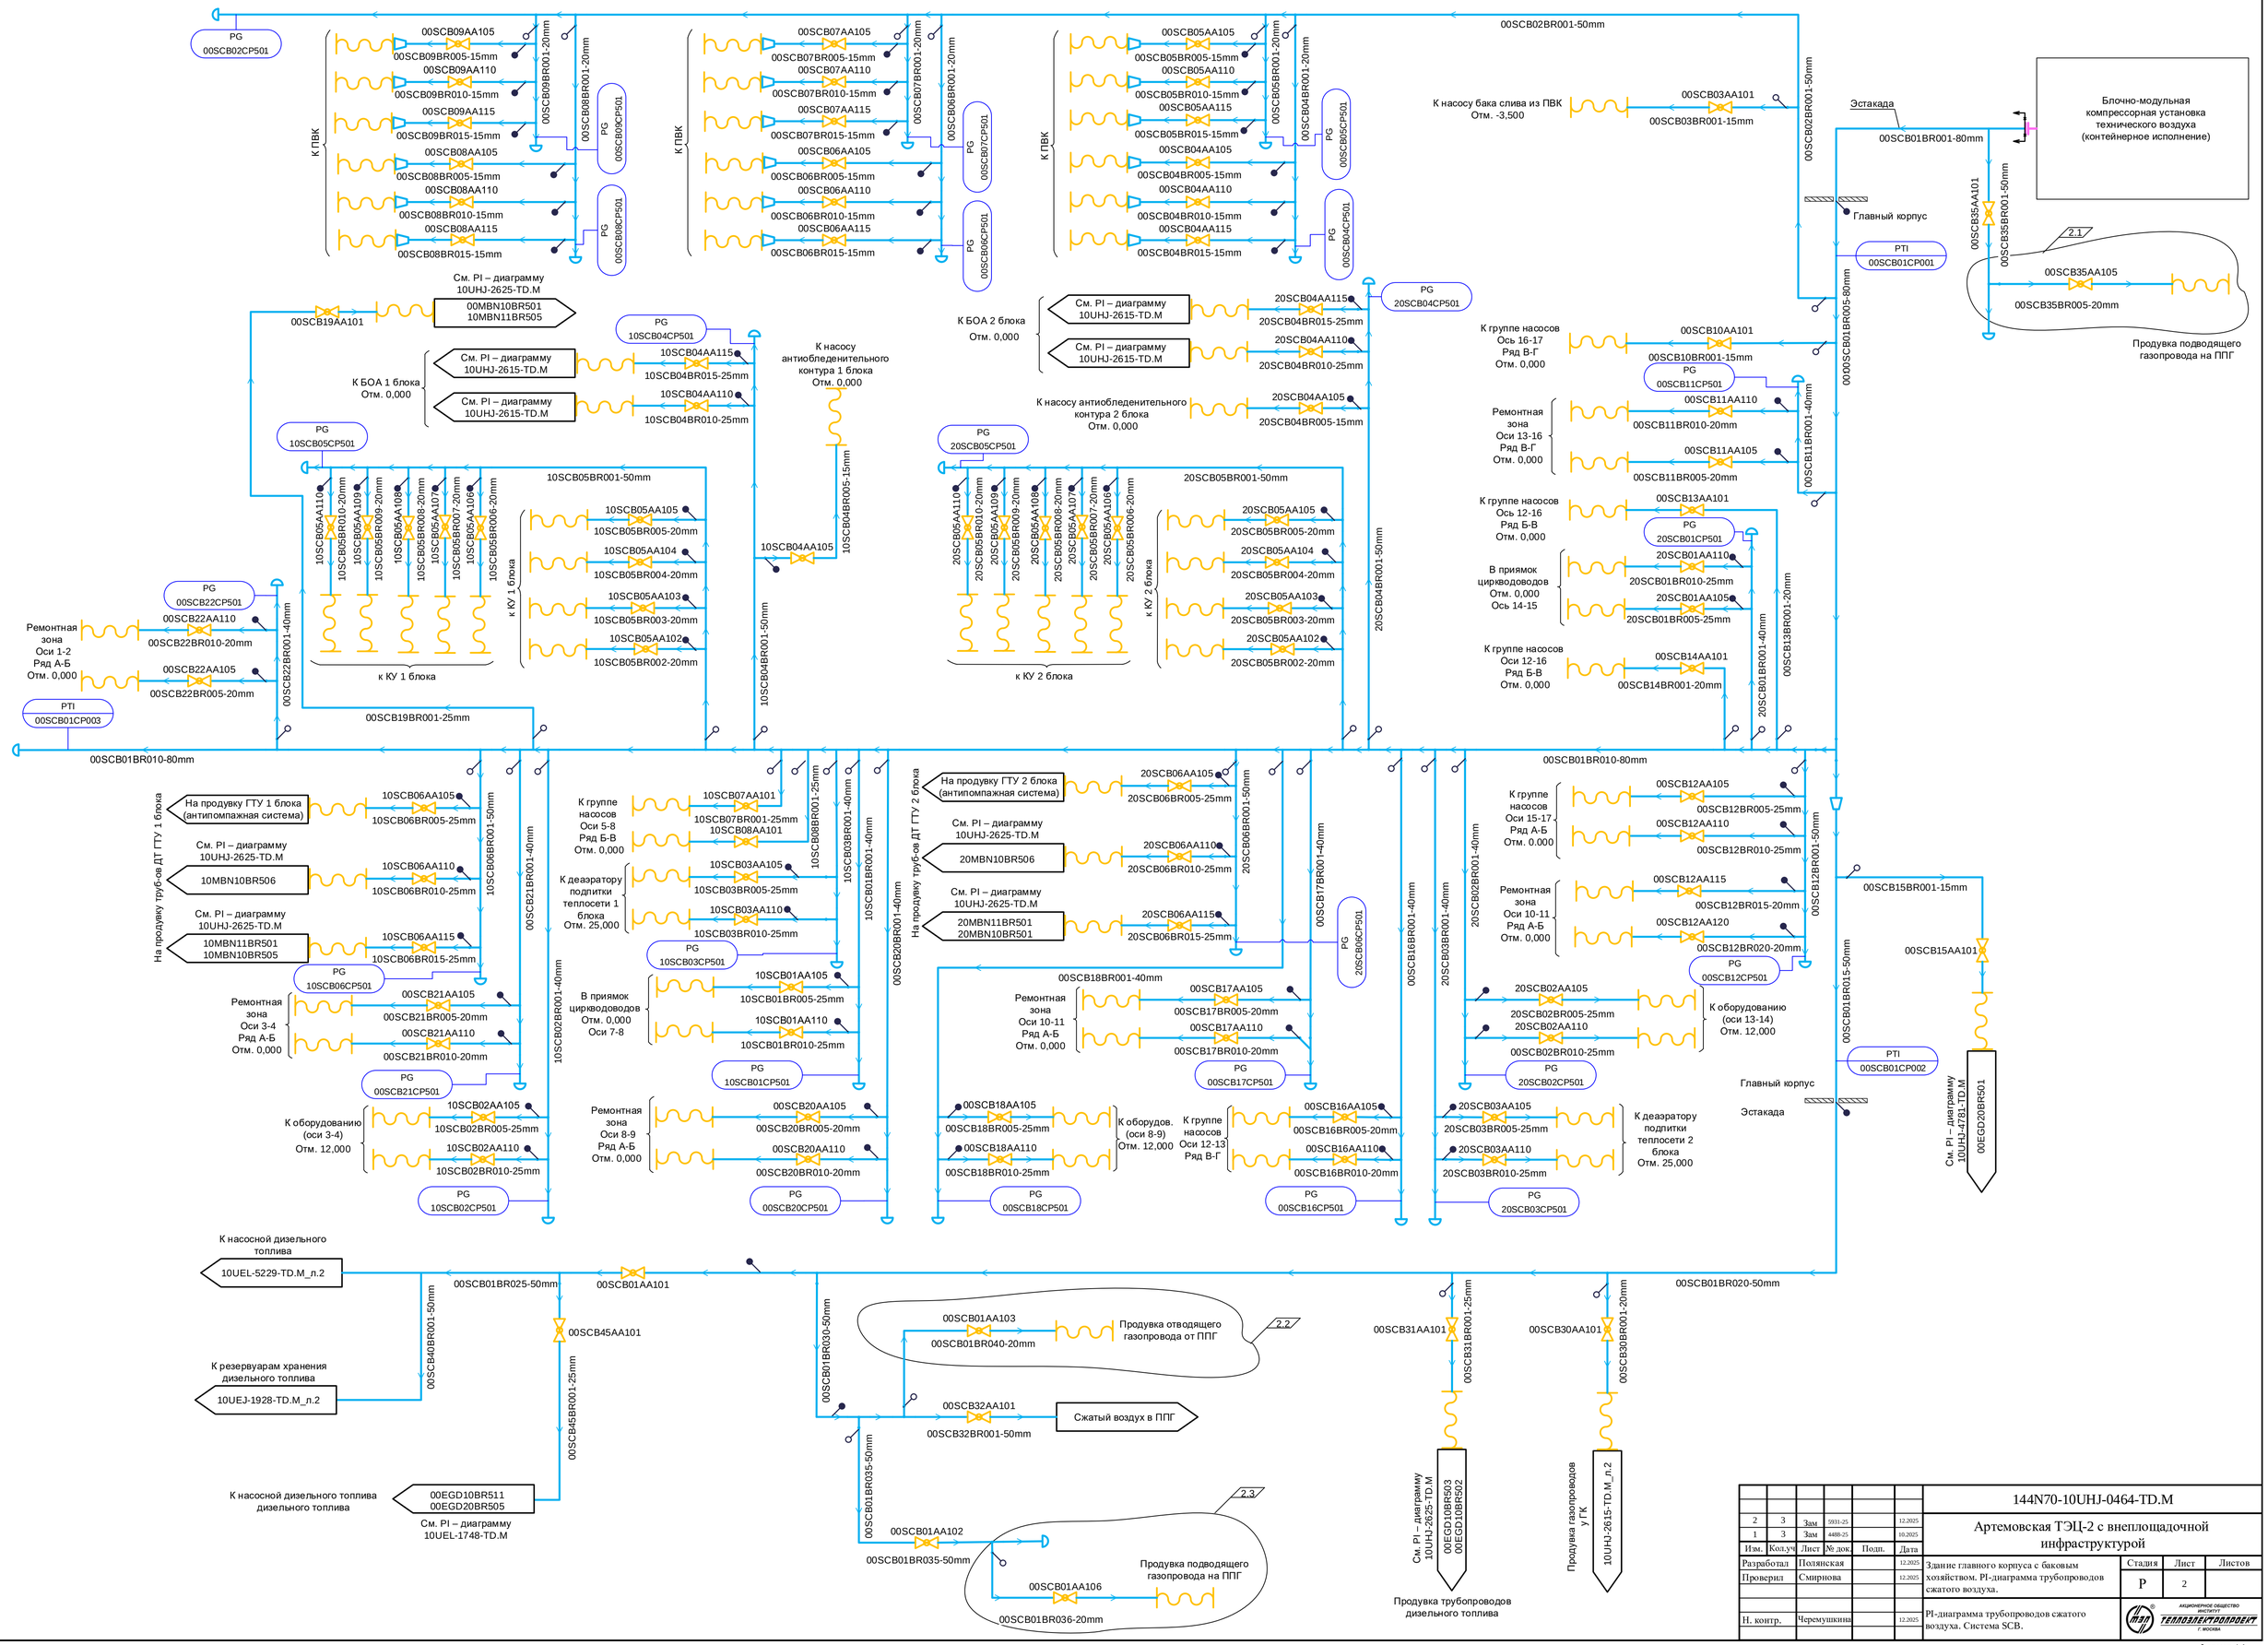

2	3	Зам	5931-25		12.2025	144N70-10UHJ-0464-TD.M
1	3	Зам	4488-25		10.2025	Артемовская ТЭЦ-2 с внеплощадочной инфраструктурой
Изм.	Кол.уч	Лист	№ док.	Подп.	Дата	
Разработал		Полянская			12.2025	Здание главного корпуса с баковым хозяйством. PI-диаграмма трубопроводов сжатого воздуха.
Проверил		Смирнова			12.2025	
Н. контр.		Черемушкина			12.2025	PI-диаграмма трубопроводов сжатого воздуха. Система SCB.

Стадия	Лист	Листов
Р	2	

АКЦИОНЕРНОЕ ОБЩЕСТВО ИНСТИТУТ ТЕПЛОЭЛЕКТРОПРОЕКТ г. МОСКВА

Согласовано: ОАСУ Долженкова

Взам. инв. № | Подпись и дата | Инв. № подл.

Формат А1