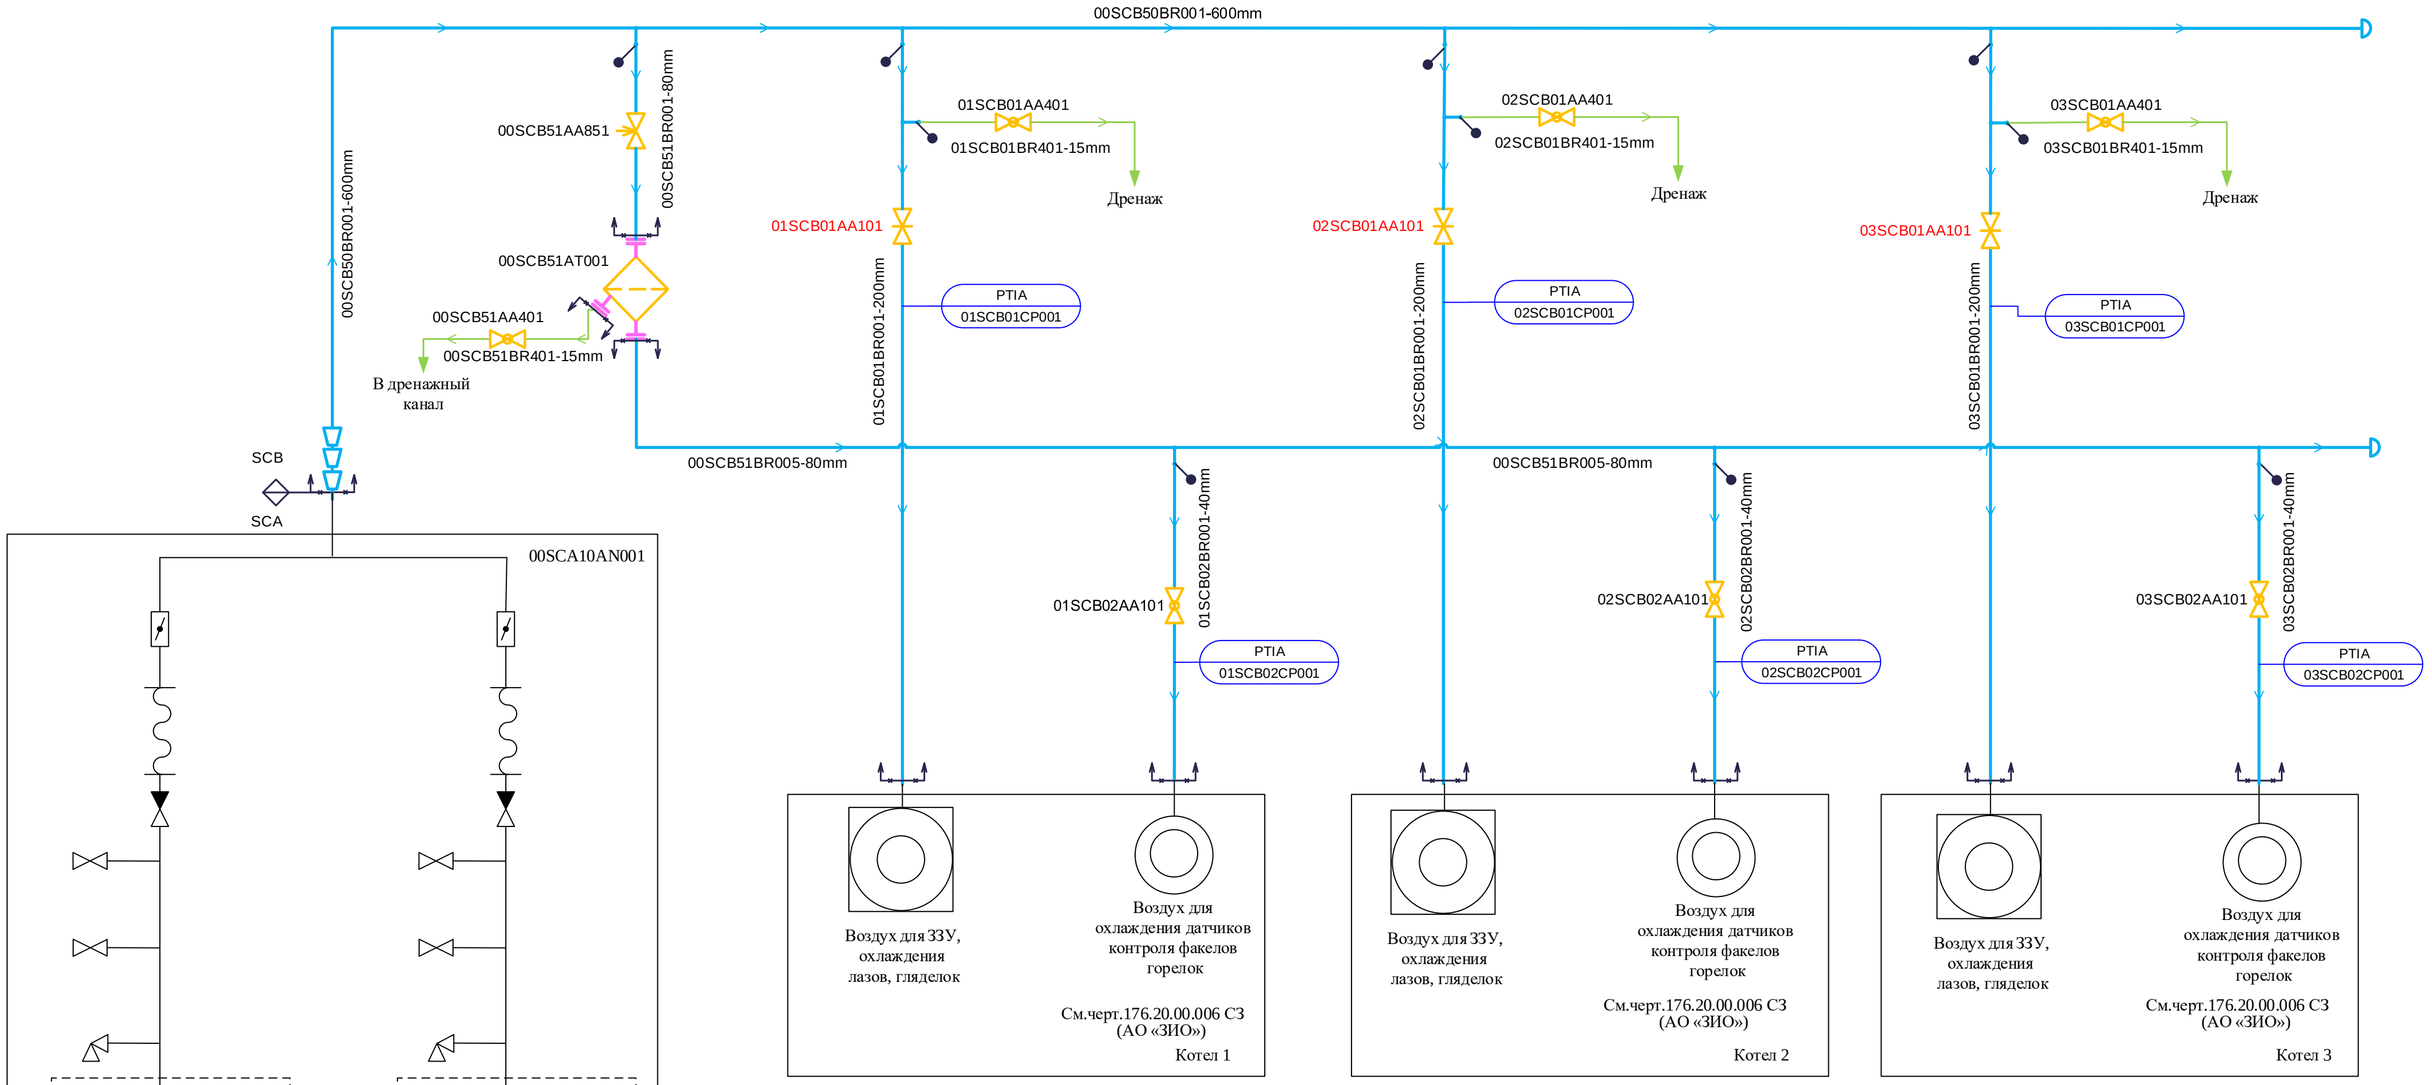

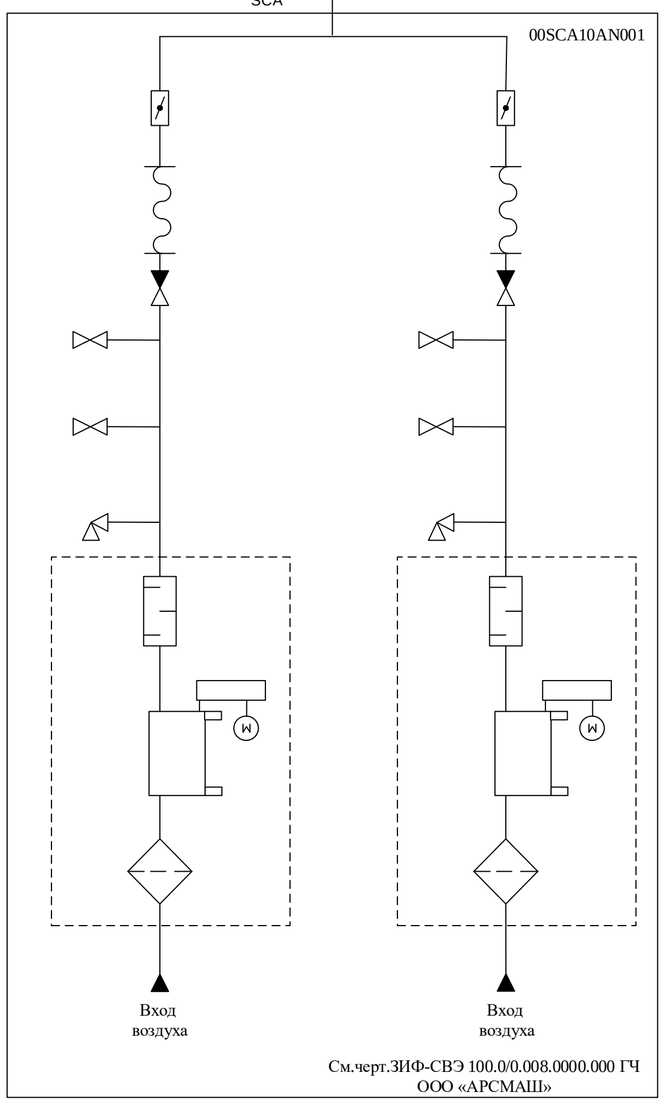

Изм.	Кол.уч	Лист	№ док.	Подп.	Дата
2	-	Зам	5931-25		12.2025
1	-	Нов	4488-25		10.2025
Разработал		Полянская			12.2025
Проверил		Смирнова			12.2025
Н. контр.		Черемушкина			12.2025

144N70 – 10UHJ – 0464 – TD.M

Артемовская ТЭЦ-2 с внеплощадочной инфраструктурой

Здание главного корпуса с баковым хозяйством. PI-диаграмма сжатого воздуха.

Стадия	Лист	Листов
Р	3	

PI-диаграмма сжатого воздуха. Система SCB

АКЦИОНЕРНОЕ ОБЩЕСТВО ИНСТИТУТ ТЕПЛОЭЛЕКТРОПРОЕКТ Г. МОСКВА

Согласовано

ОАСУ Додельцева

Взам. инв. №

Подпись и дата

Инв. № подл.

Формат А2