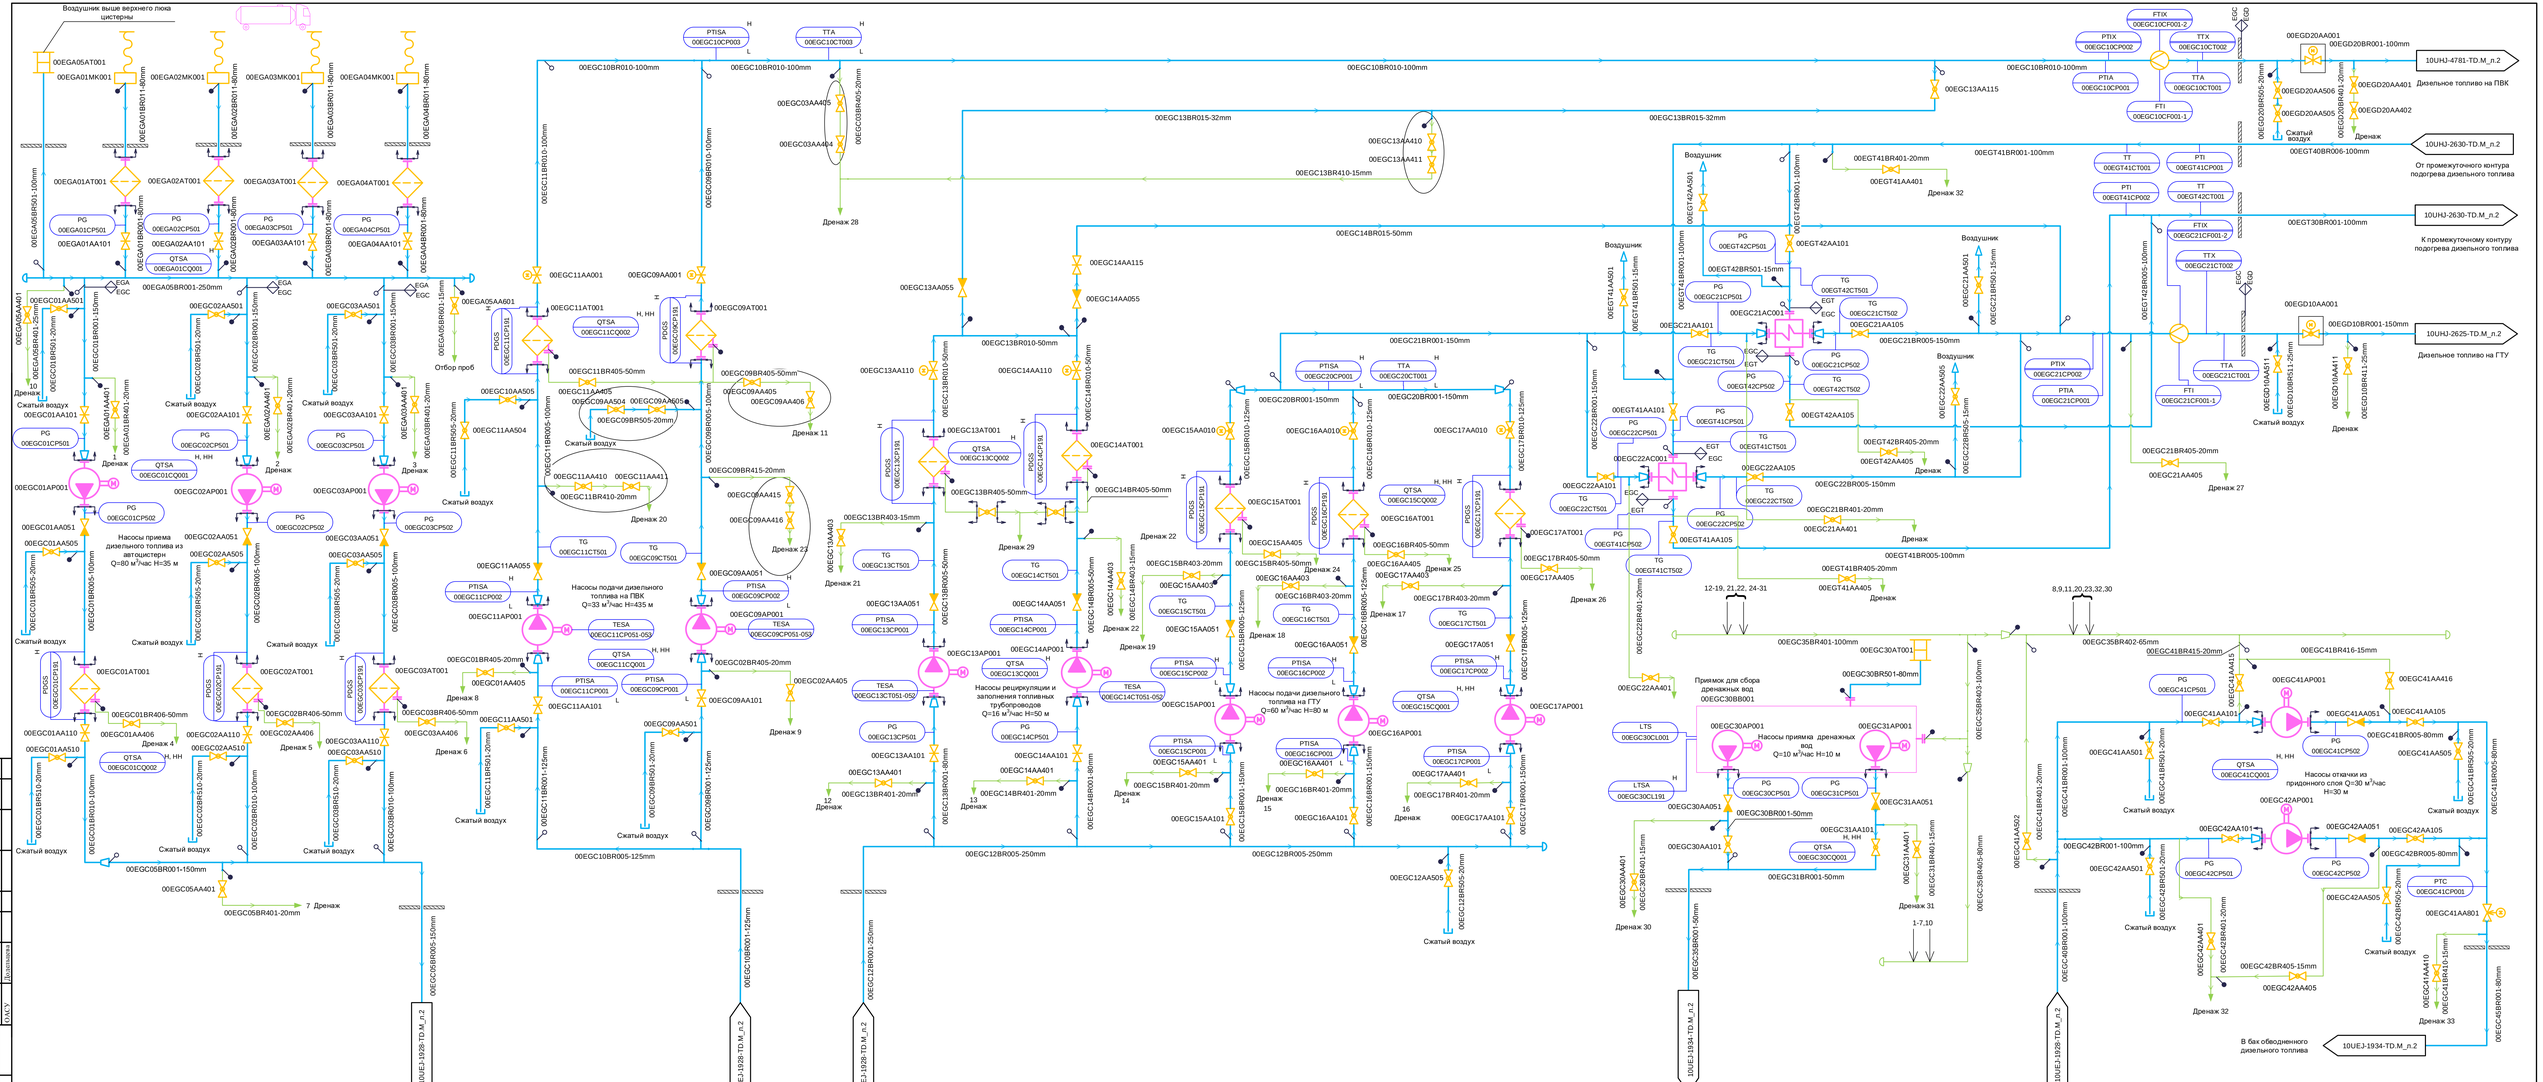

							144N70 – 10UEL – 1748 – TD.M
1	-	Зам	888-П			01.03.17	Строительство Артемовской ТЭЦ-2 с внеплощадочной инфраструктурой
Изм.	Кол.уч.	Лист	№ док.	Подп.	Дата		
Разработал	Полянская						Насосная станция жидкого топлива со складом масла в мелкой таре. PI-Диаграмма трубопроводов дизельного топлива
Проверил	Смирнова						Стадия: Р; Лист: 2; Листов:
Н. контр.	Чермушкин						PI-Диаграмма трубопроводов дизельного топлива. Система EGA, EGC

Согласовано

Взам. инв. №

Подпись и дата

Инв. № подл.

Формат А2х3