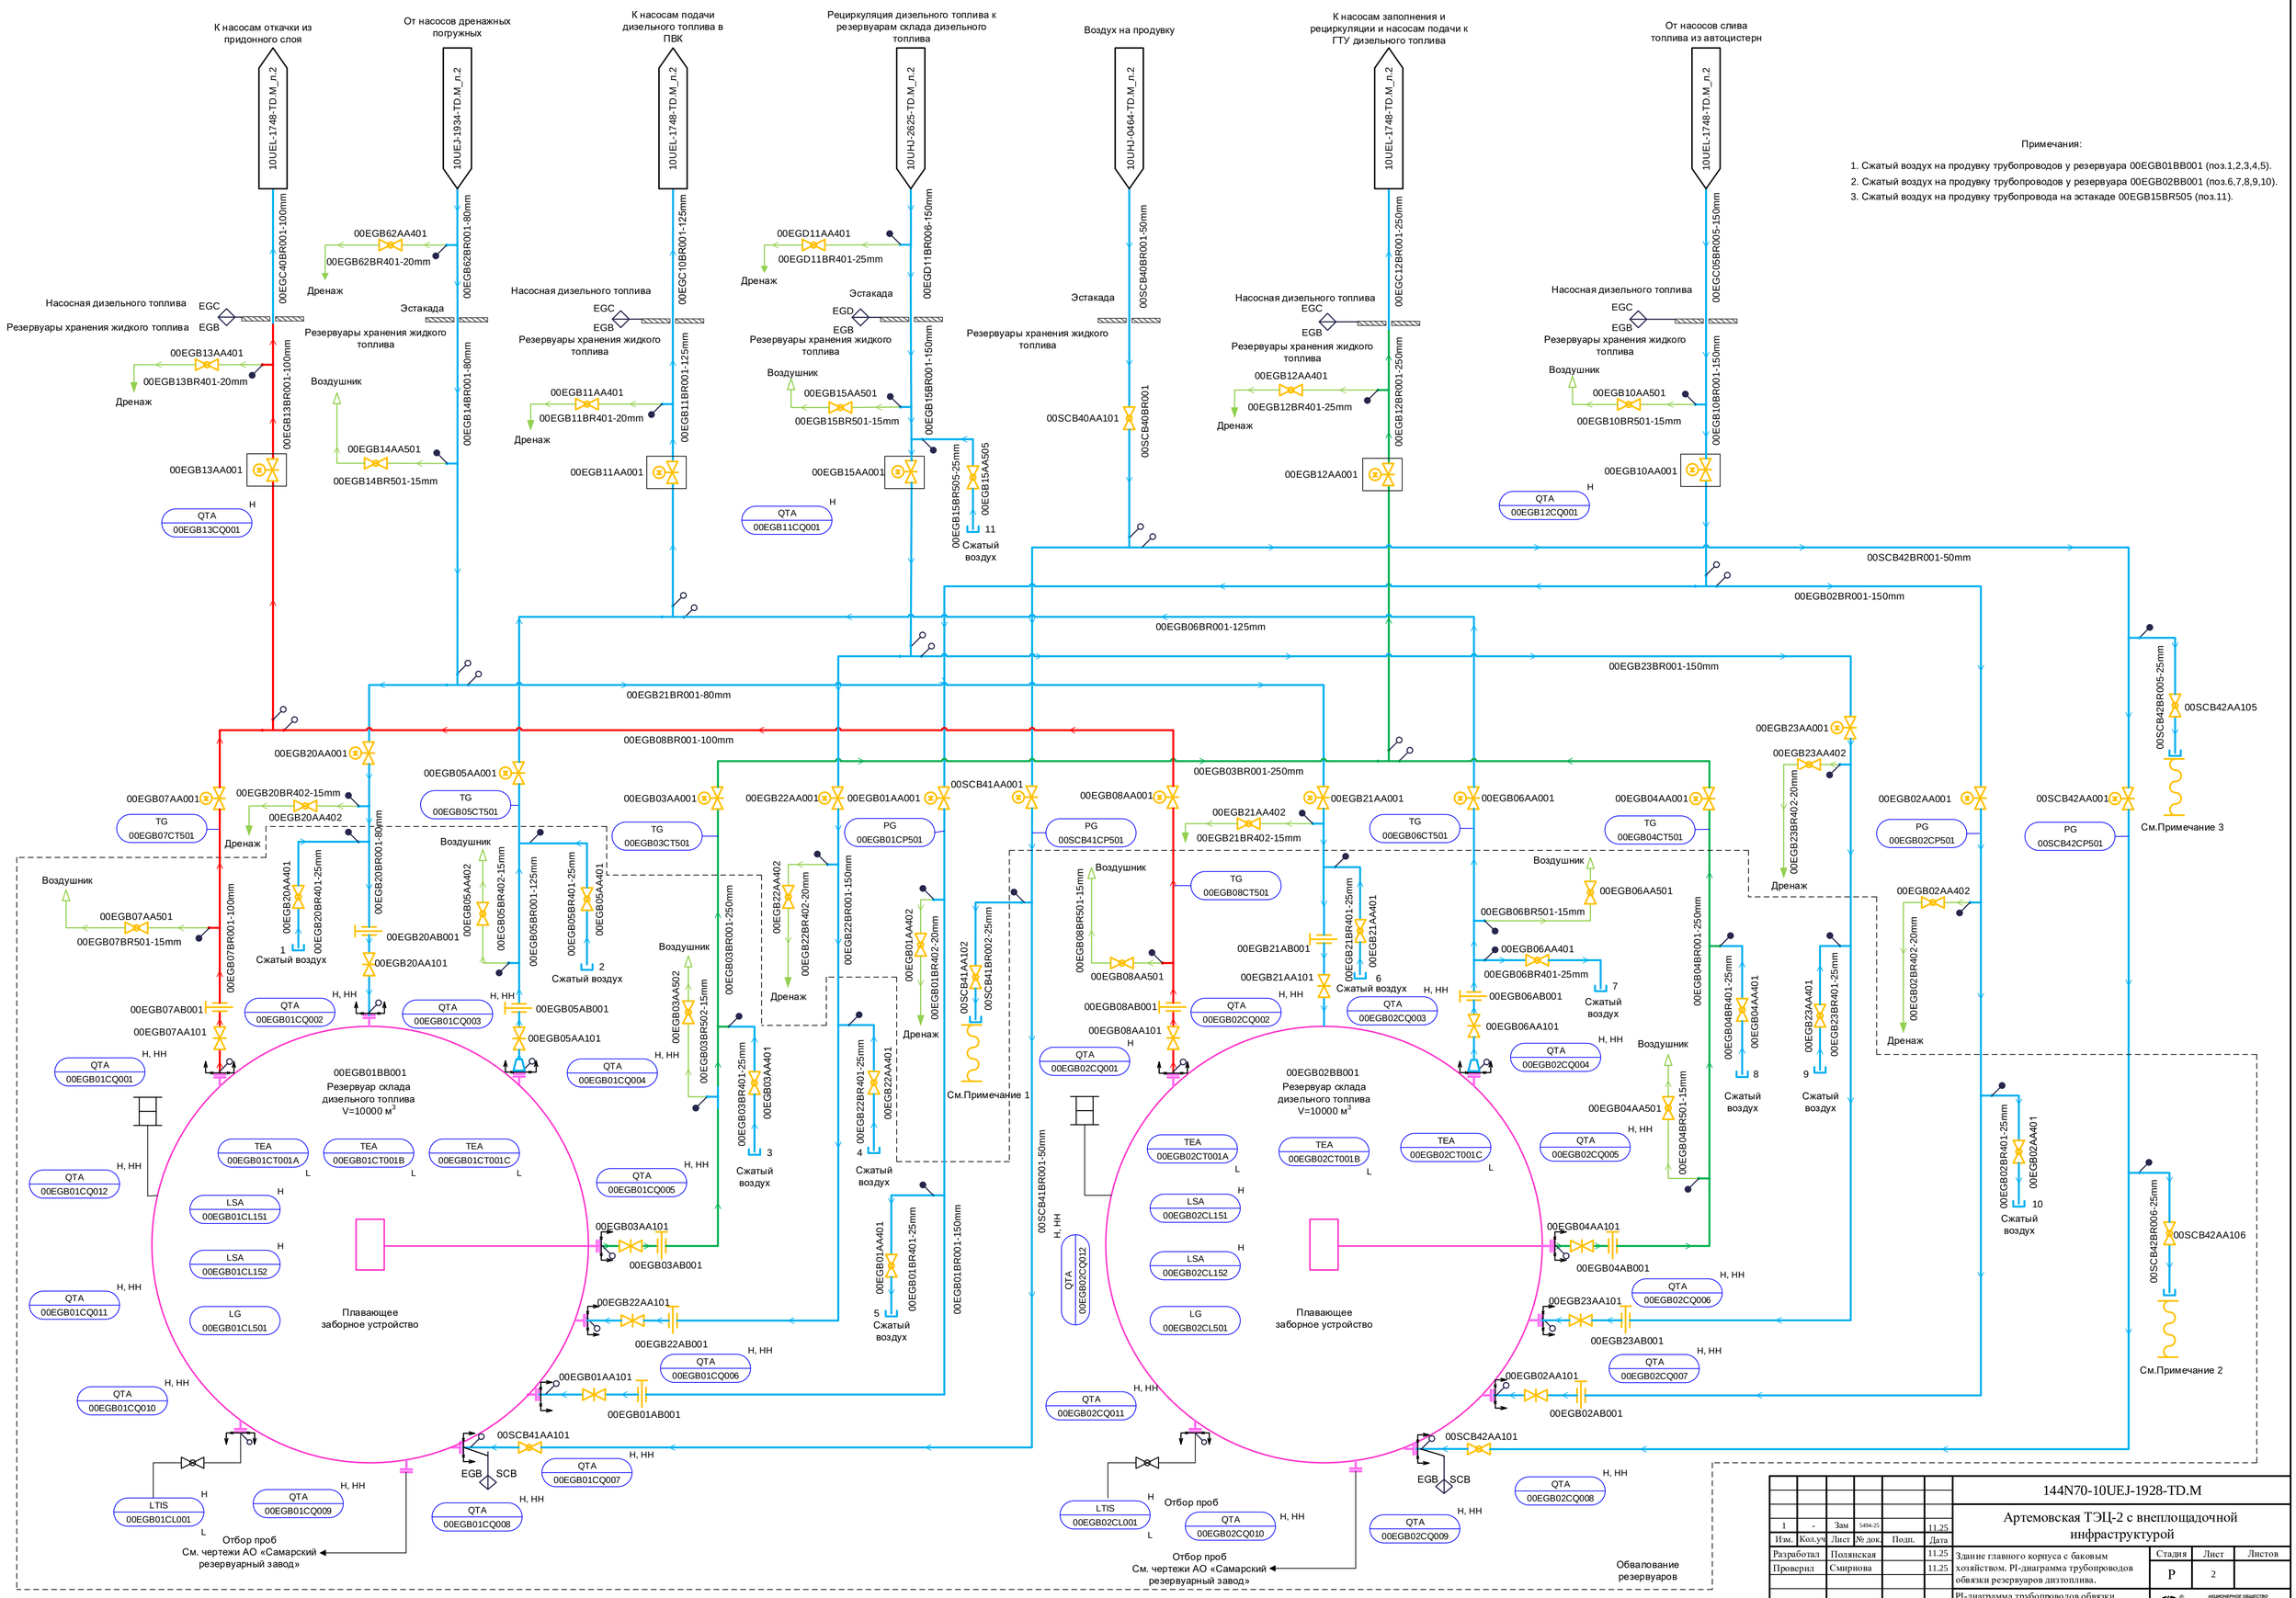


| | | | | | | |
|---|---|---|---|---|---|---|
| 1 | - | Зам | 5494-25 | | 11.25 | 144N70-10UEJ-1928-TD.M |
| Изм. | Кол.уч | Лист | № док. | Подп. | Дата | Артемовская ТЭЦ-2 с вненлощадочной инфраструктурой |
| Разработал | | Полянская | | | 11.25 | Здание главного корпуса с баковым хозяйством. PI-диаграмма трубопроводов обвязки резервуаров дизтоплива. |
| Проверил | | Смирнова | | | 11.25 | Стадия: Р; Лист: 2; Листов: |
| Н. контр. | | Черемушкина | | | 11.25 | PI-диаграмма трубопроводов обвязки резервуаров дизтоплива. Система EGB, EGC, EGD, SCB. |

АКЦИОНЕРНОЕ ОБЩЕСТВО ИНСТИТУТ ТЕПЛОЭЛЕКТРОПРОЕКТ г. МОСКВА

Согласовано

ОАСУ

Взам. инв. №

Подпись и дата

Инв. № подл.

Формат А1