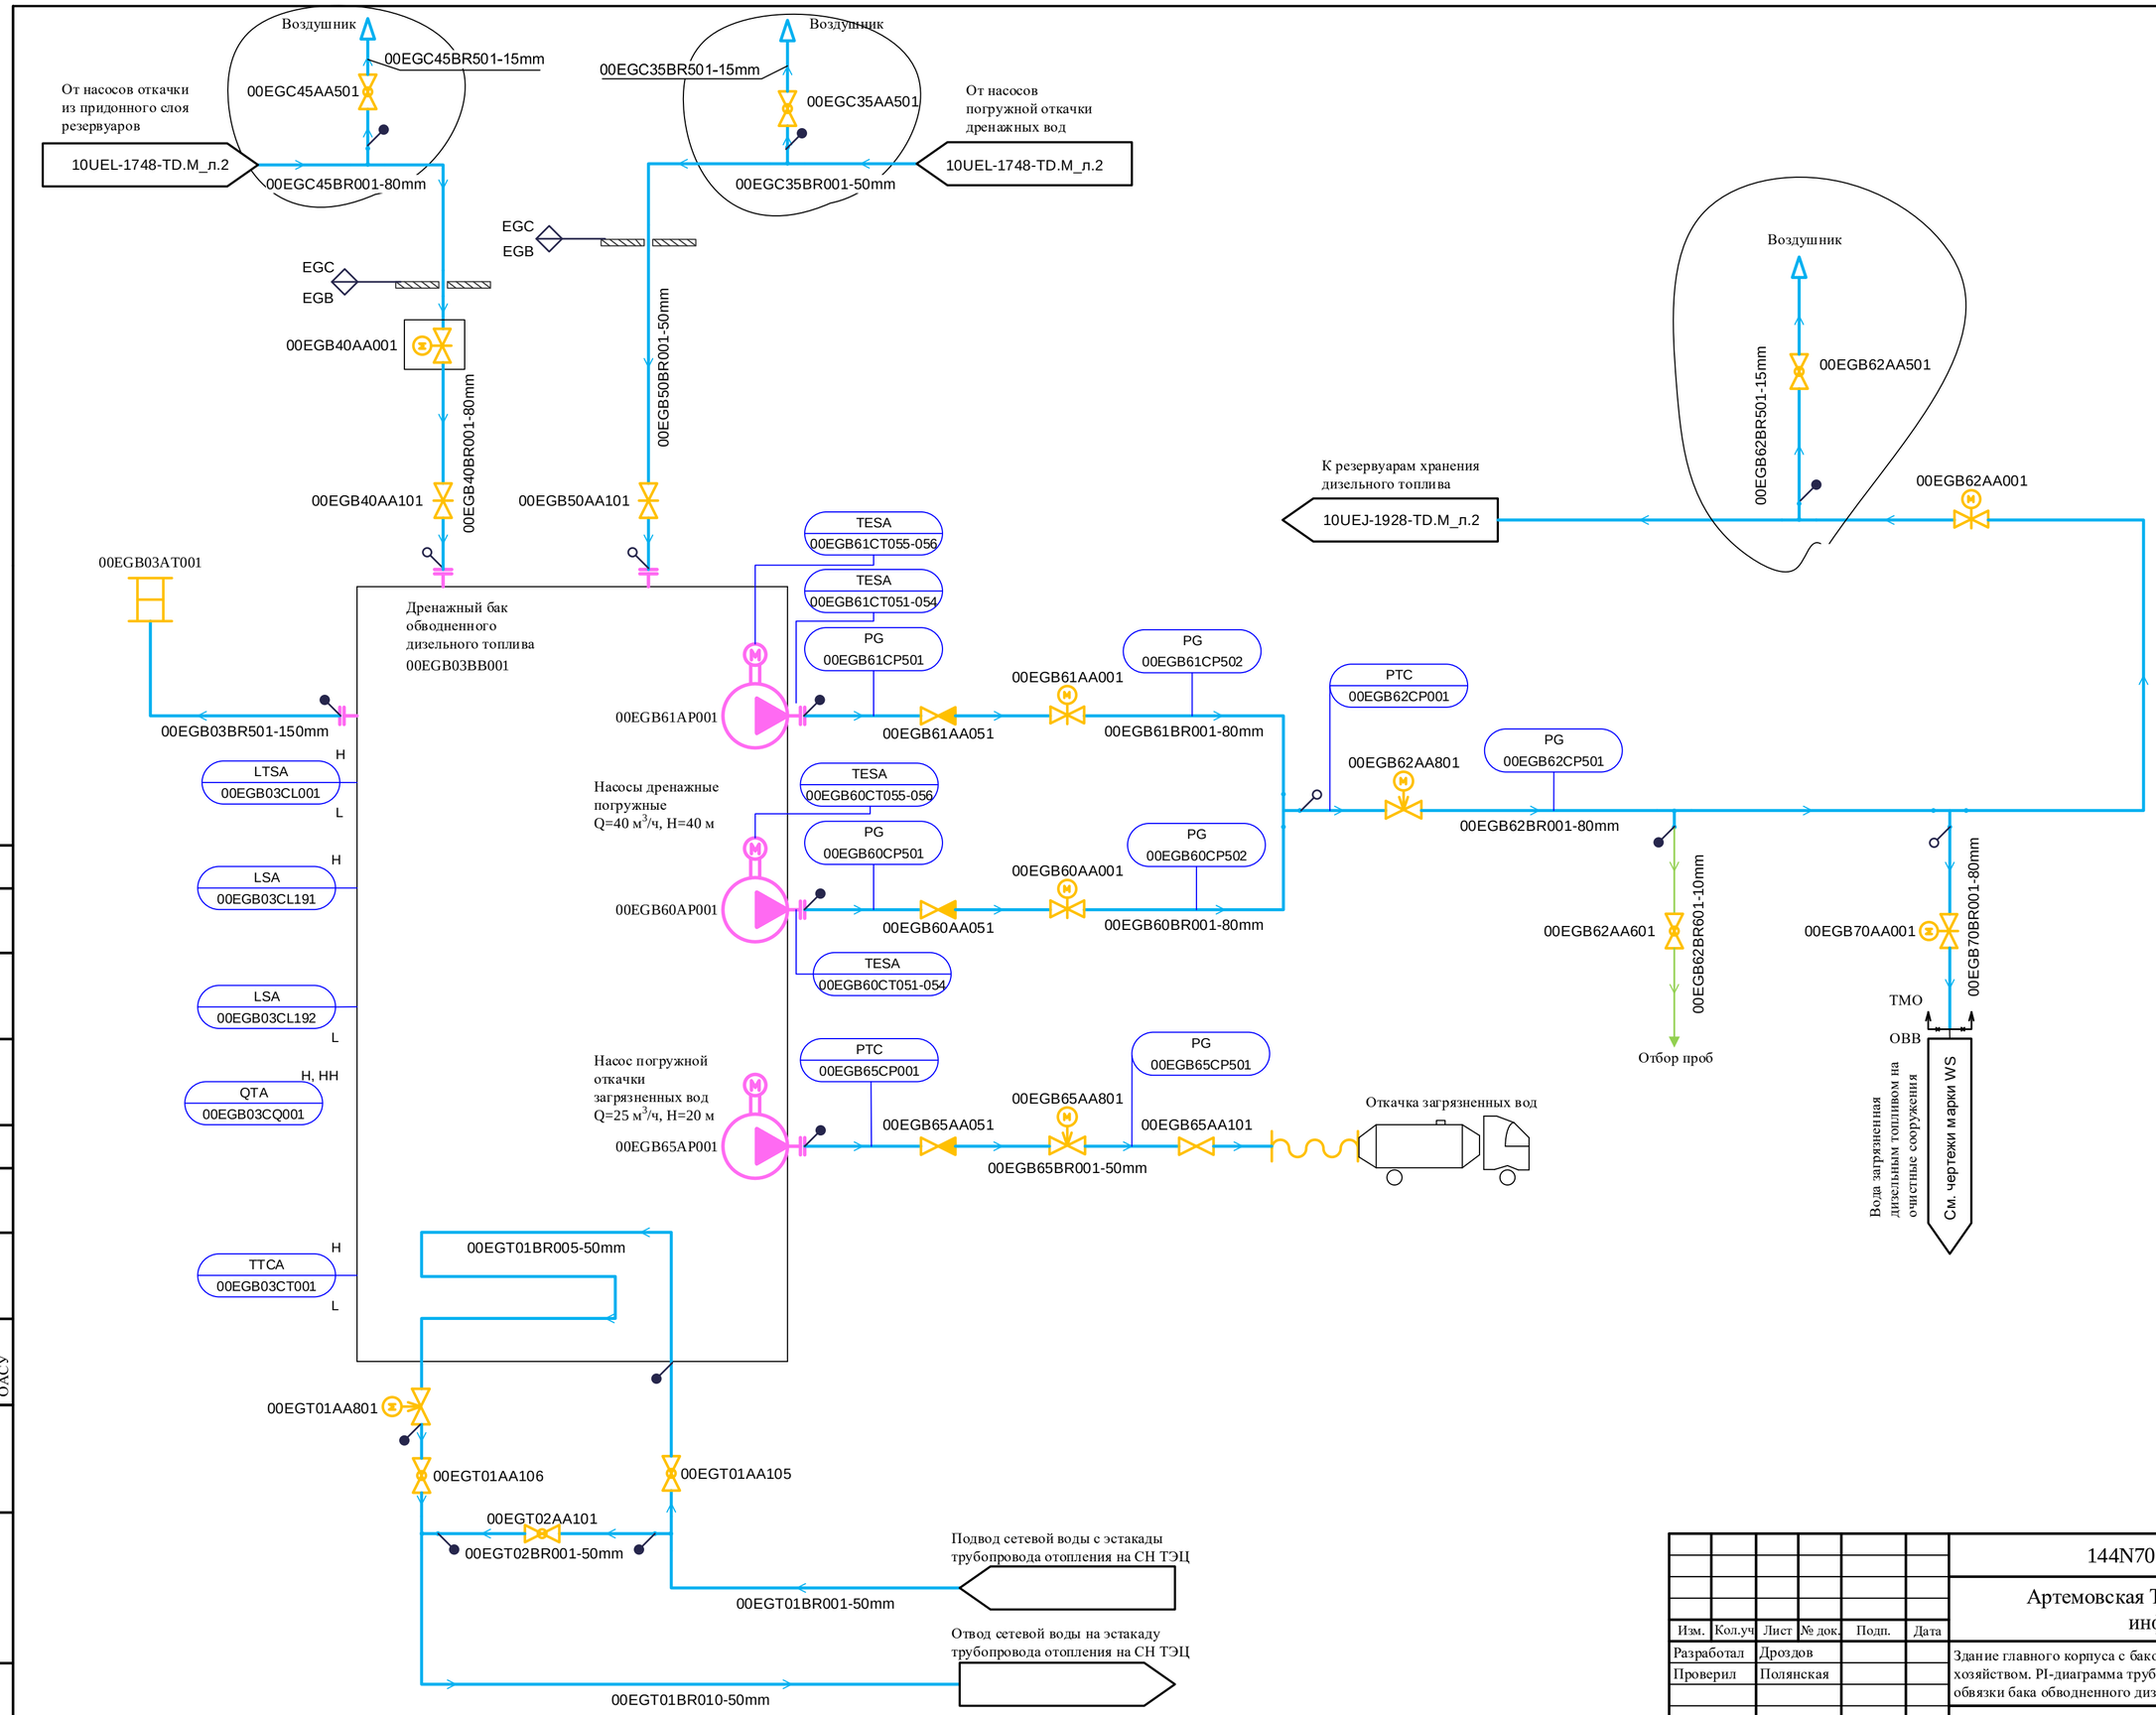

Изм.	Кол.уч	Лист	№ док.	Подп.	Дата	144N70-10UEJ-1934-TD.M
						Артемовская ТЭЦ-2 с внеплощадочной инфраструктурой
Разработал		Дроздов				Здание главного корпуса с баковым хозяйством. PI-диаграмма трубопроводов обвязки бака обводненного дизтоплива.
Проверил		Полянская				Стадия: Р; Лист: 2; Листов:
Н. контр.		Астраханцев				PI-диаграмма трубопроводов обвязки бака обводненного дизтоплива.

АКЦИОНЕРНОЕ ОБЩЕСТВО ИНСТИТУТ ТЕПЛОЭЛЕКТРОПРОЕКТ г. МОСКВА

Согласовано

ОАСУ

Взам. инв. №

Подпись и дата

Инв. № подл.

Формат А2