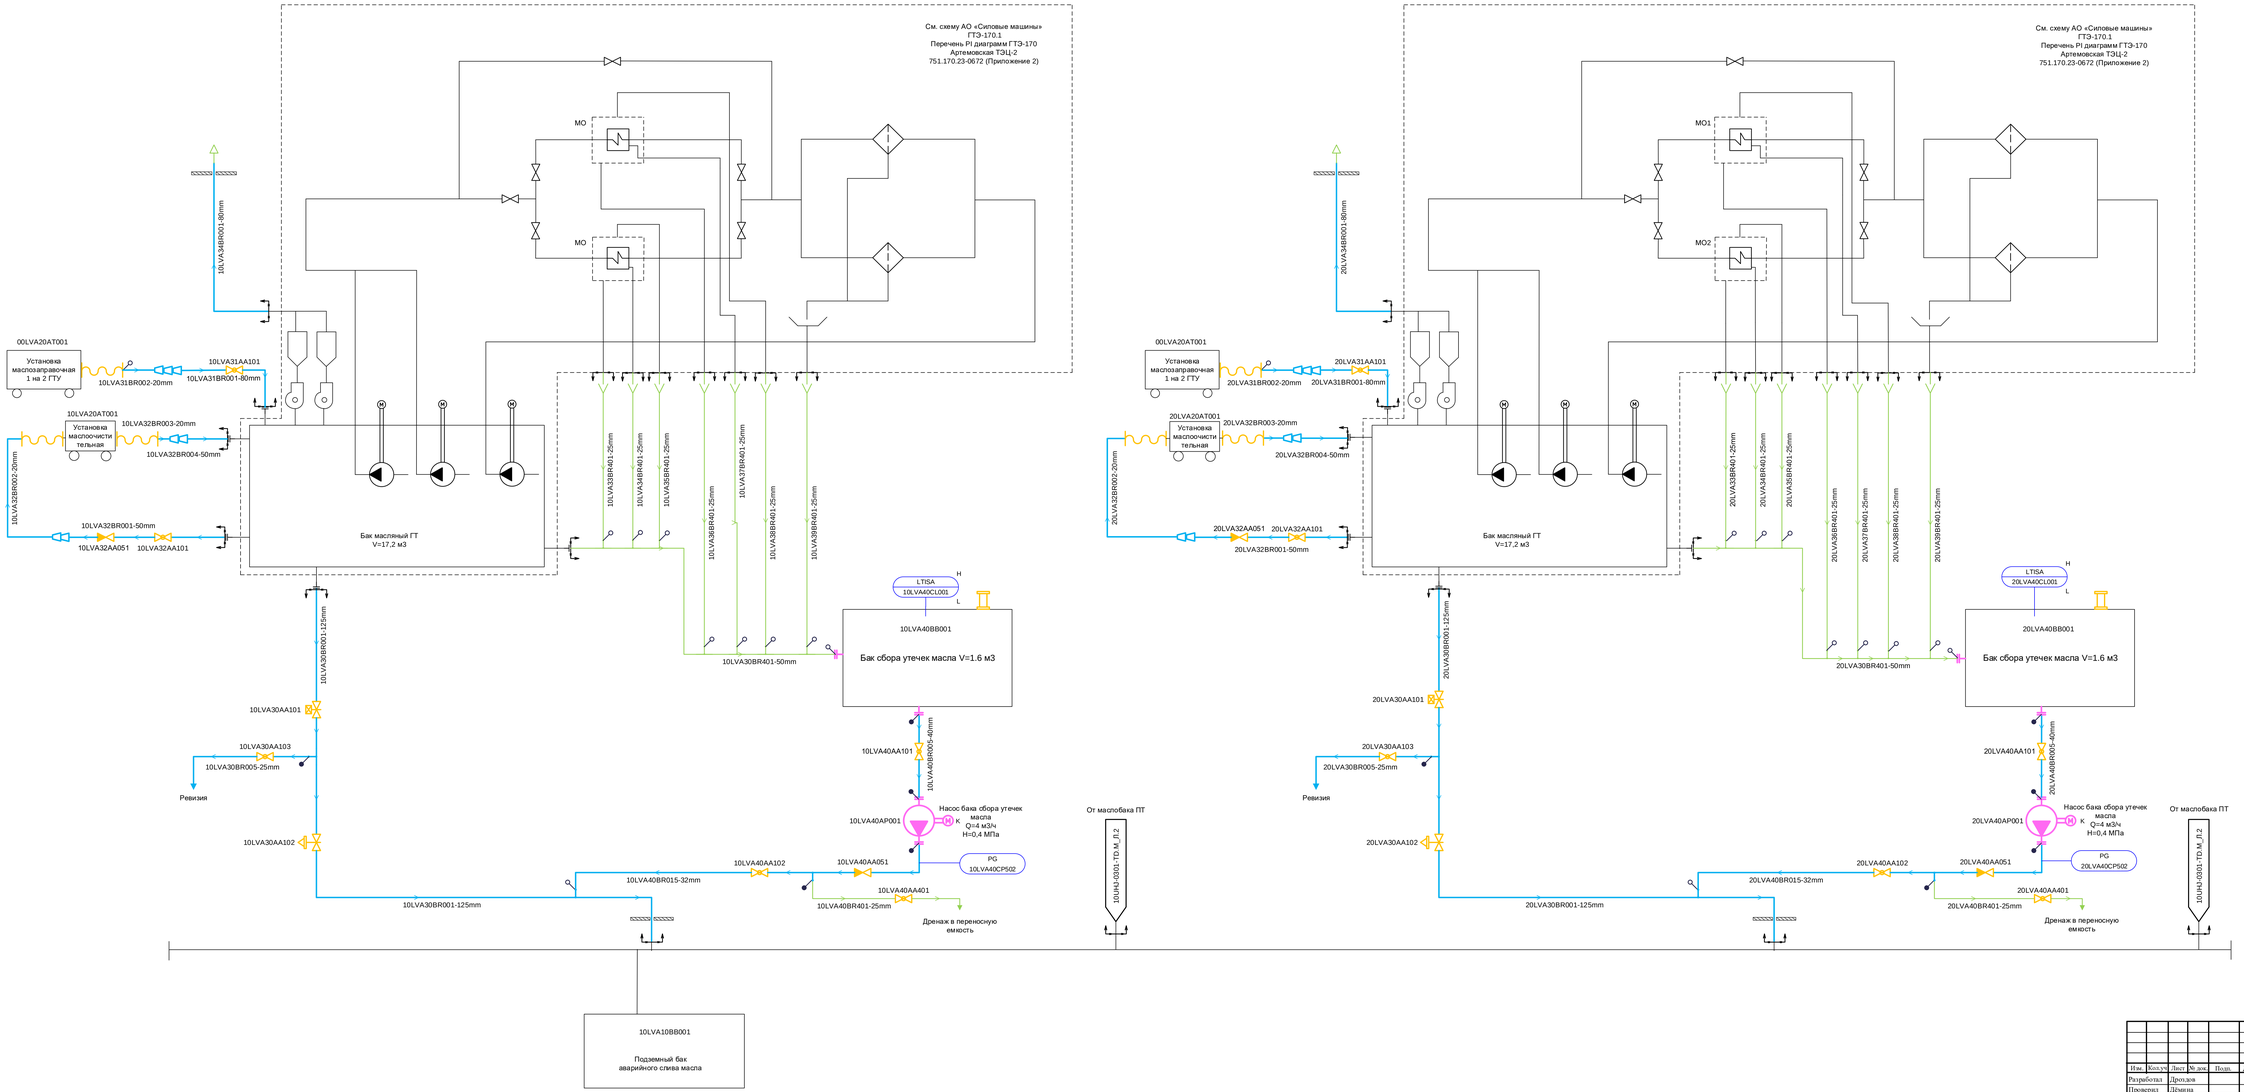

Примечание:
1.Управление насосами 10LVA40AP001 и 20LVA40AP001 по месту.
2.При снижении уровня в баках 10LVA40BB001, 20LVA40BB001 сбора утечек масла до Min значения отключения насосов.
3.Сигнализация высокого уровня в баках сбора утечек масла.
4.Задвижки 10LVA30AA101 , 20LVA30AA101 оснащены замковым устройством.
5.Задвижка 10LVA30AA102,20LVA30AA102 оснащены копонковым приводом.

Изм.	Кол.уч.	Лист	№ док.	Подп.	Дата	144N70-10UHJ-2610-TD.M	
						Артемовская ТЭЦ-2 с внеплощадочной инфраструктурой	
Разработал	Дроздов					Здание главного корпуса с боковым хозяйством. PI-диаграмма трубопроводов маслоснабжения ГТУ.	Стадия: Р; Лист: 2; Листов:
Проверил	Демина						
Н. контр.	Астраханцев					PI-диаграмма трубопроводов маслоснабжения ГТУ.	АКЦИОНЕРНОЕ ОБЩЕСТВО ТЕХЭНЕРГОПРОМФИНИШ

Согласовано

ОАСУ	
Взам. инв. №	
Подпись и дата	
Инв. № подл.	

Формат А2х3