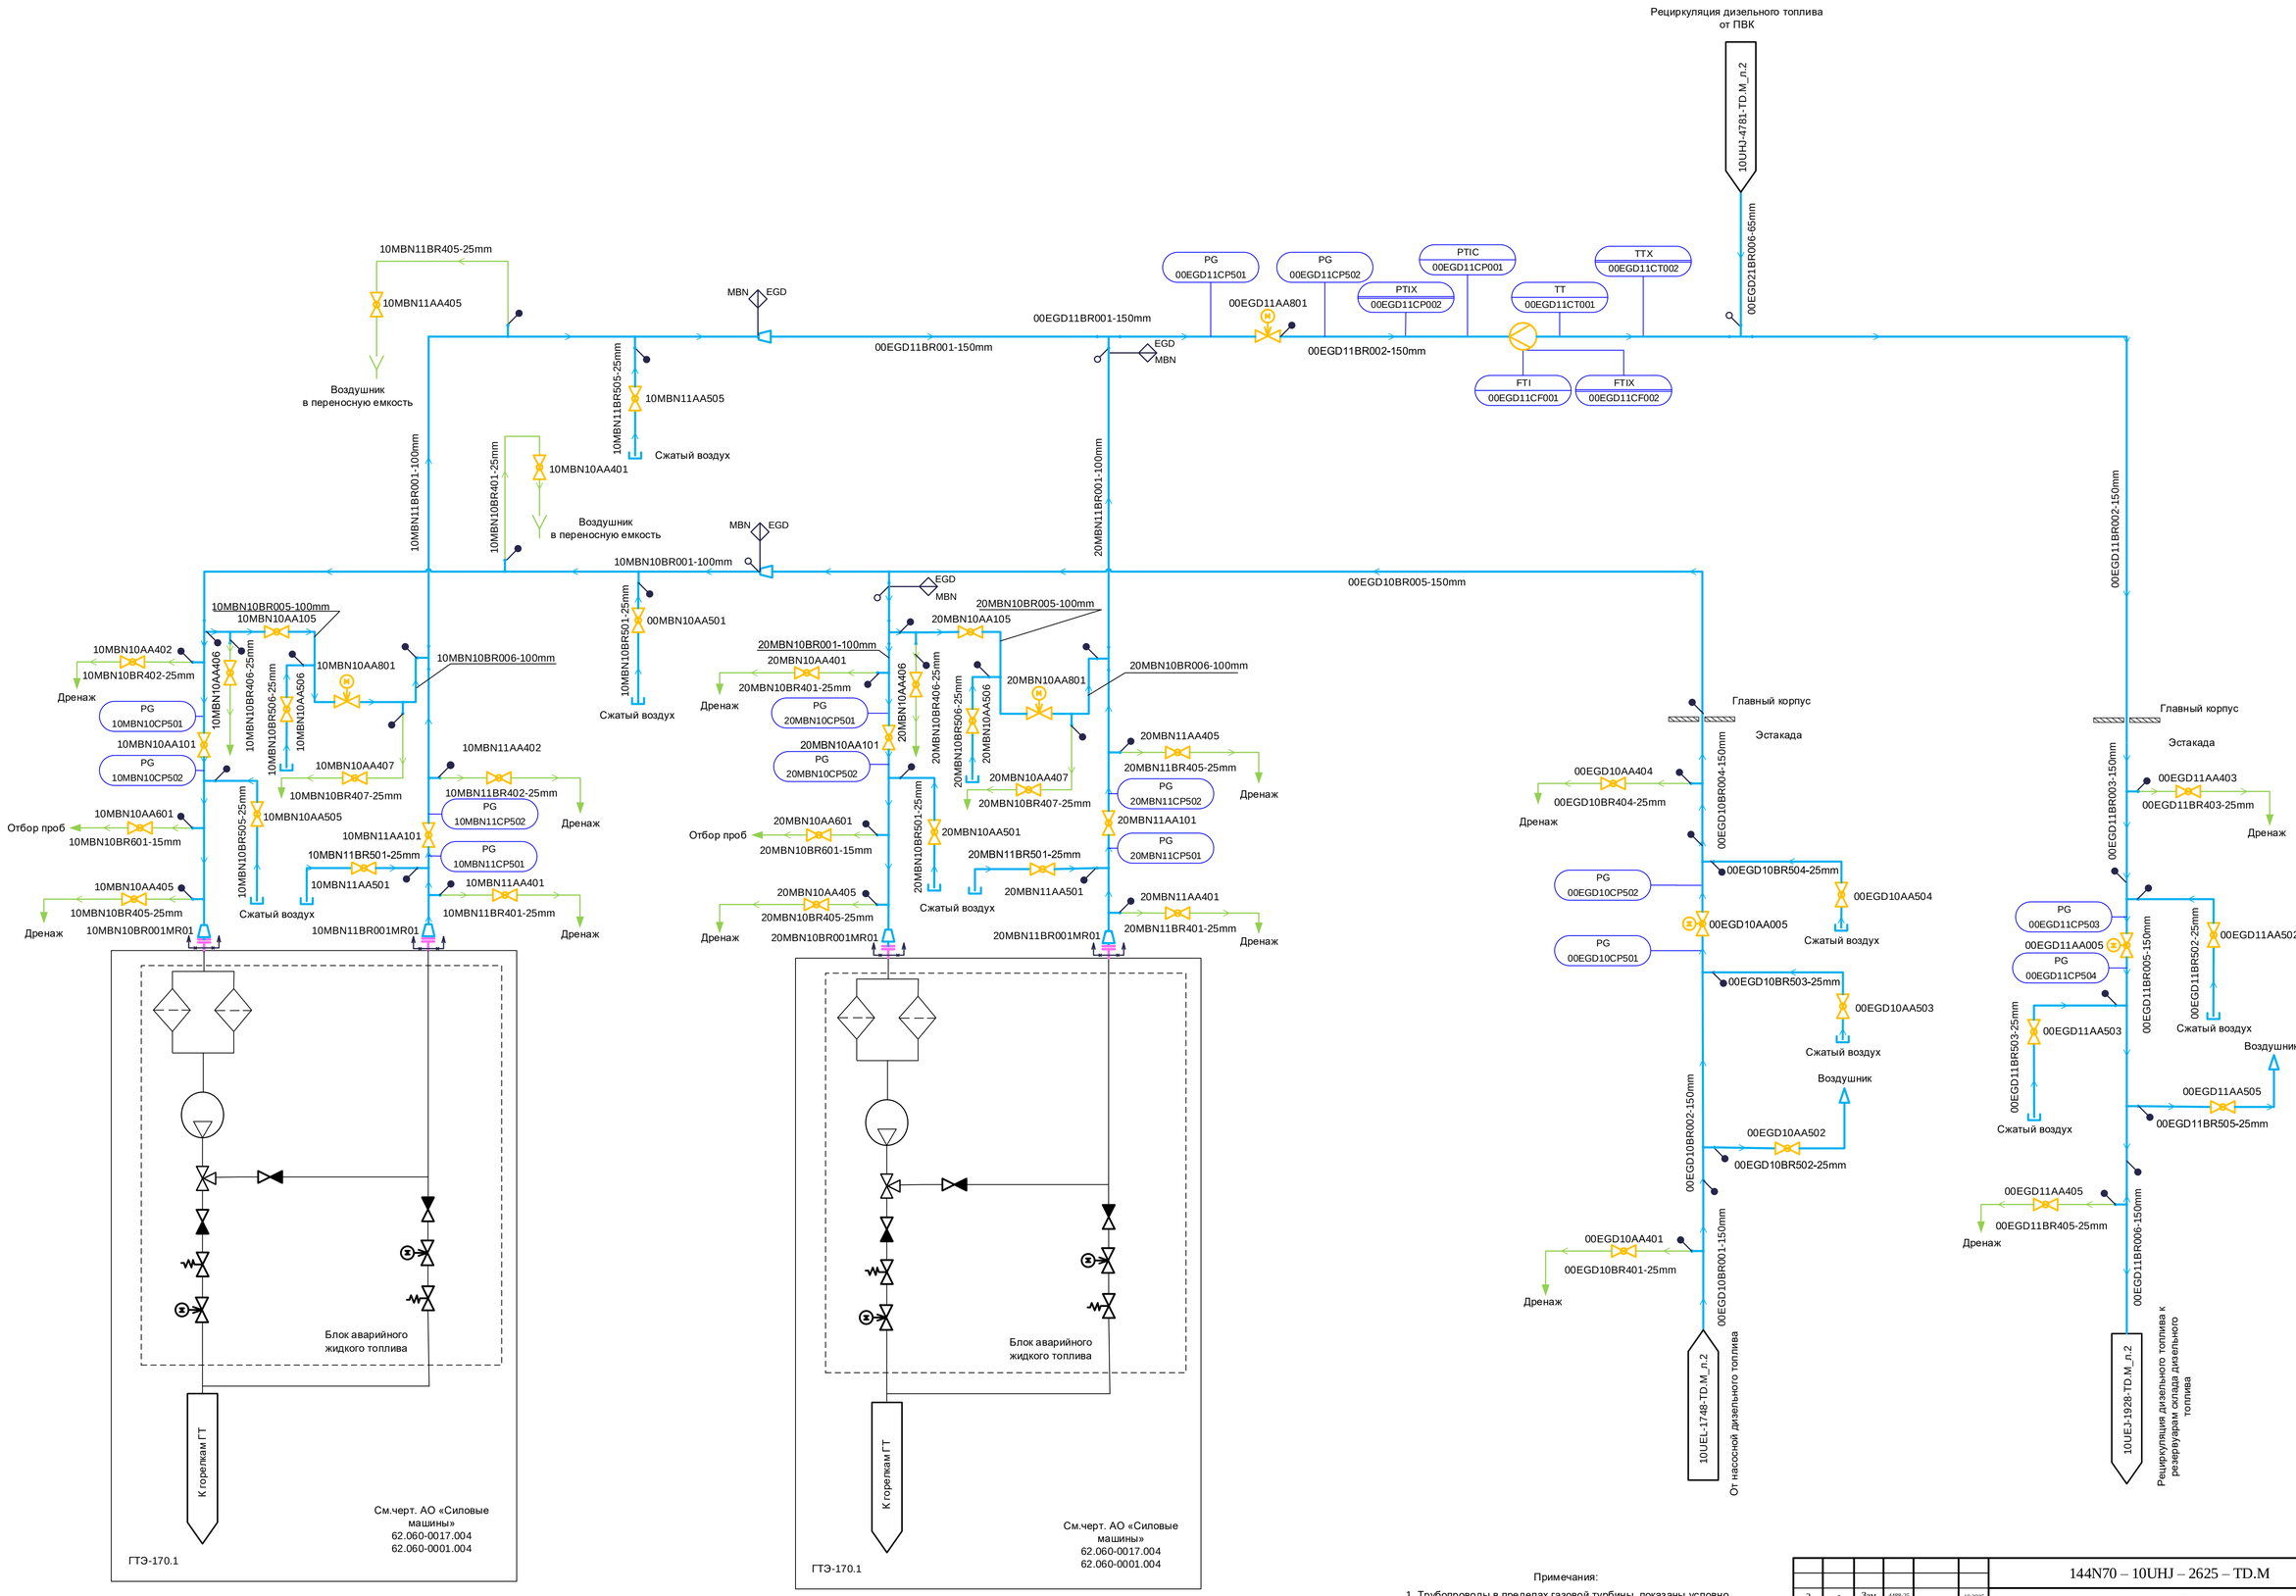

Примечания:

1. Трубопроводы в пределах газовой турбины показаны условно.
2. Все дренажи слить в переносную емкость.

Изм.	Кол.уч	Лист	№ док.	Подп.	Дата
2	-	Зам	4488-25		10.2025
1	-	Зам	2548-24		

144N70 – 10UHJ – 2625 – TD.M

Строительство Артемовской ТЭЦ-2 с внеплощадочной инфраструктурой

Разработал	Полянская	
Проверил	Смирнова	
Н. контр.	Черемушкина	

Здание главного корпуса с баковым хозяйством. PI-диаграмма дизельного топлива

PI -диаграмма дизельного топлива ГТУ. Система EGD, MBN

Стадия	Лист	Листов
Р	2	

АКЦИОНЕРНОЕ ОБЩЕСТВО ИНСТИТУТ ТЕПЛОЭЛЕКТРОПРОЕКТ Г. МОСКВА

Формат А1

Согласовано: ОАСУ Долженкова

Взам. инв. №

Подпись и дата

Инв. № подл.