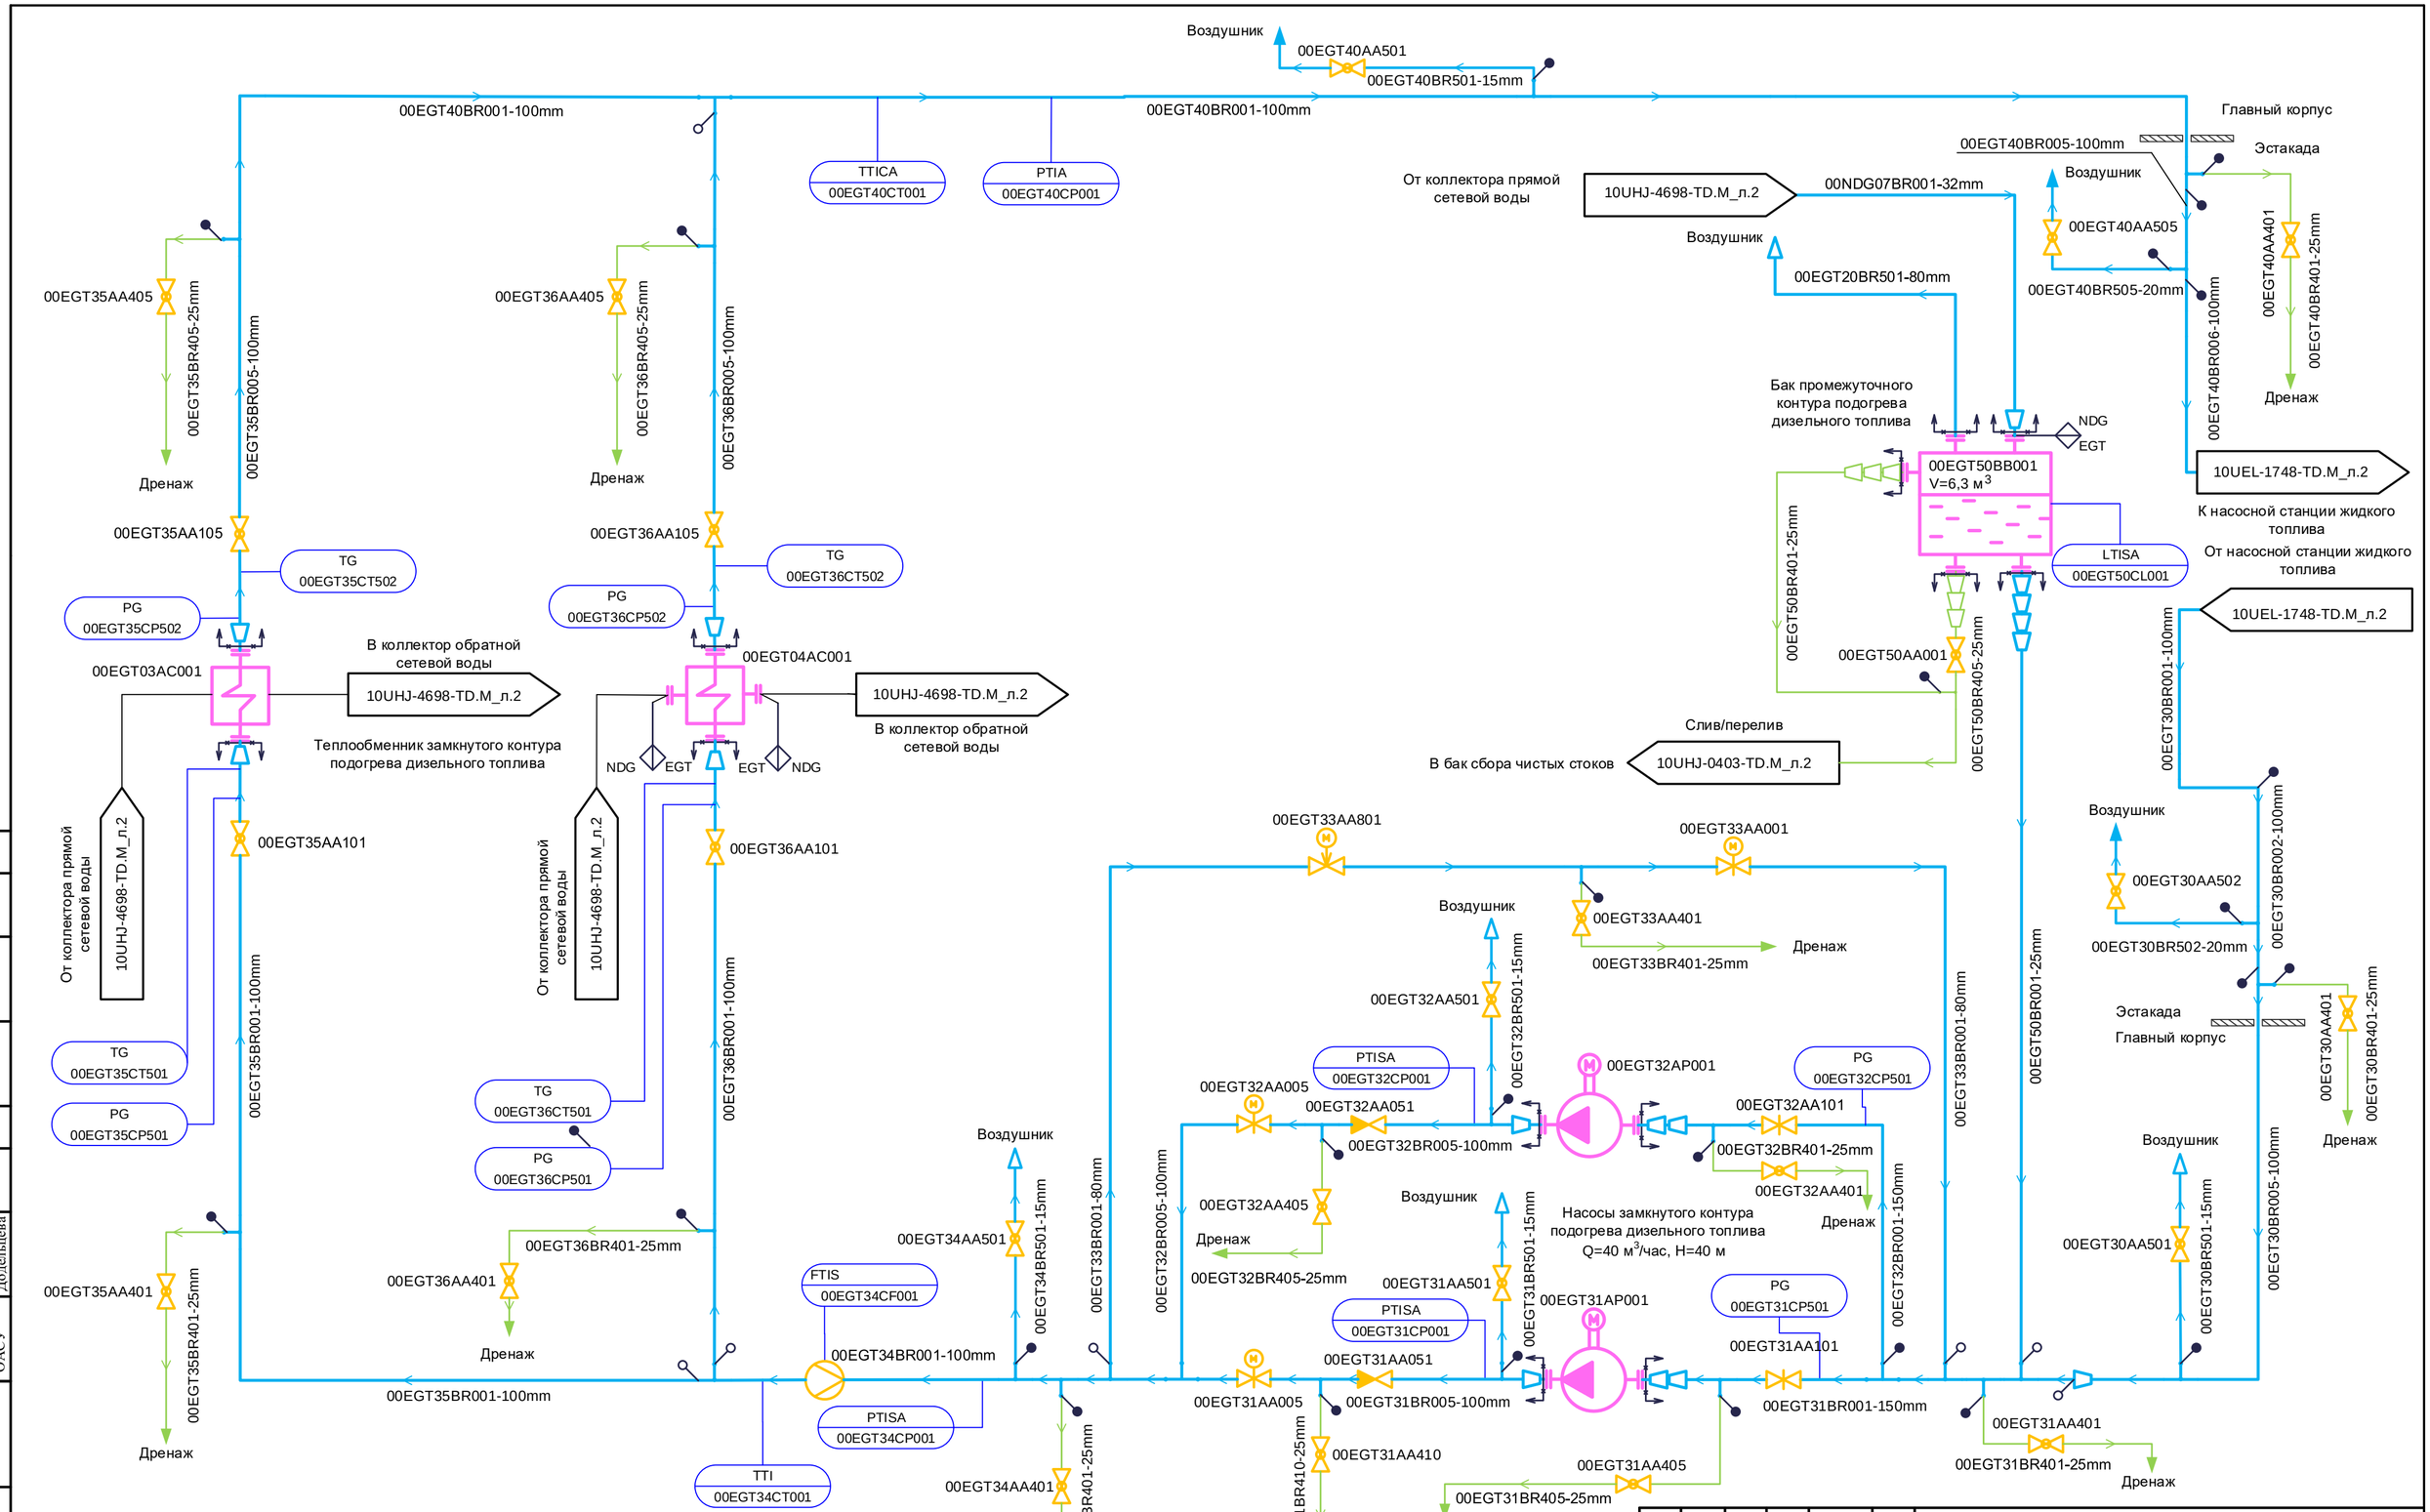

Примечания:

1. Дренажи ГК слить в дренажный приямок.
2. Дренажи с эстакады слить в ливневую канализацию. Температура рабочей среды не выше 40°С.

1	-	Зам.	4488-25		10.2025	
Изм.	Кол.уч	Лист	№ док.	Подп.	Дата	
Разработал		Полянская				
Проверил		Смирнова				
Н. контр.		Черемушкина				

144N70 – 10UHJ – 2630 – TD.M

Строительство Артемовской ТЭЦ-2 с внеплощадочной инфраструктурой

Здание главного корпуса с баковым хозяйством. PI-диаграмма трубопроводов промежуточного контура подогрева дизельного топлива

Стадия	Лист	Листов
Р	2	

PI-диаграмма трубопроводов промежуточного контура подогрева дизельного топлива. Система EGT

АКЦИОНЕРНОЕ ОБЩЕСТВО ИНСТИТУТ ТЕПЛОЭЛЕКТРОПРОЕКТ г. МОСКВА

Согласовано

ОАСУ Долецева

Взам. инв. №

Подпись и дата

Инв. № подл.

Формат А2