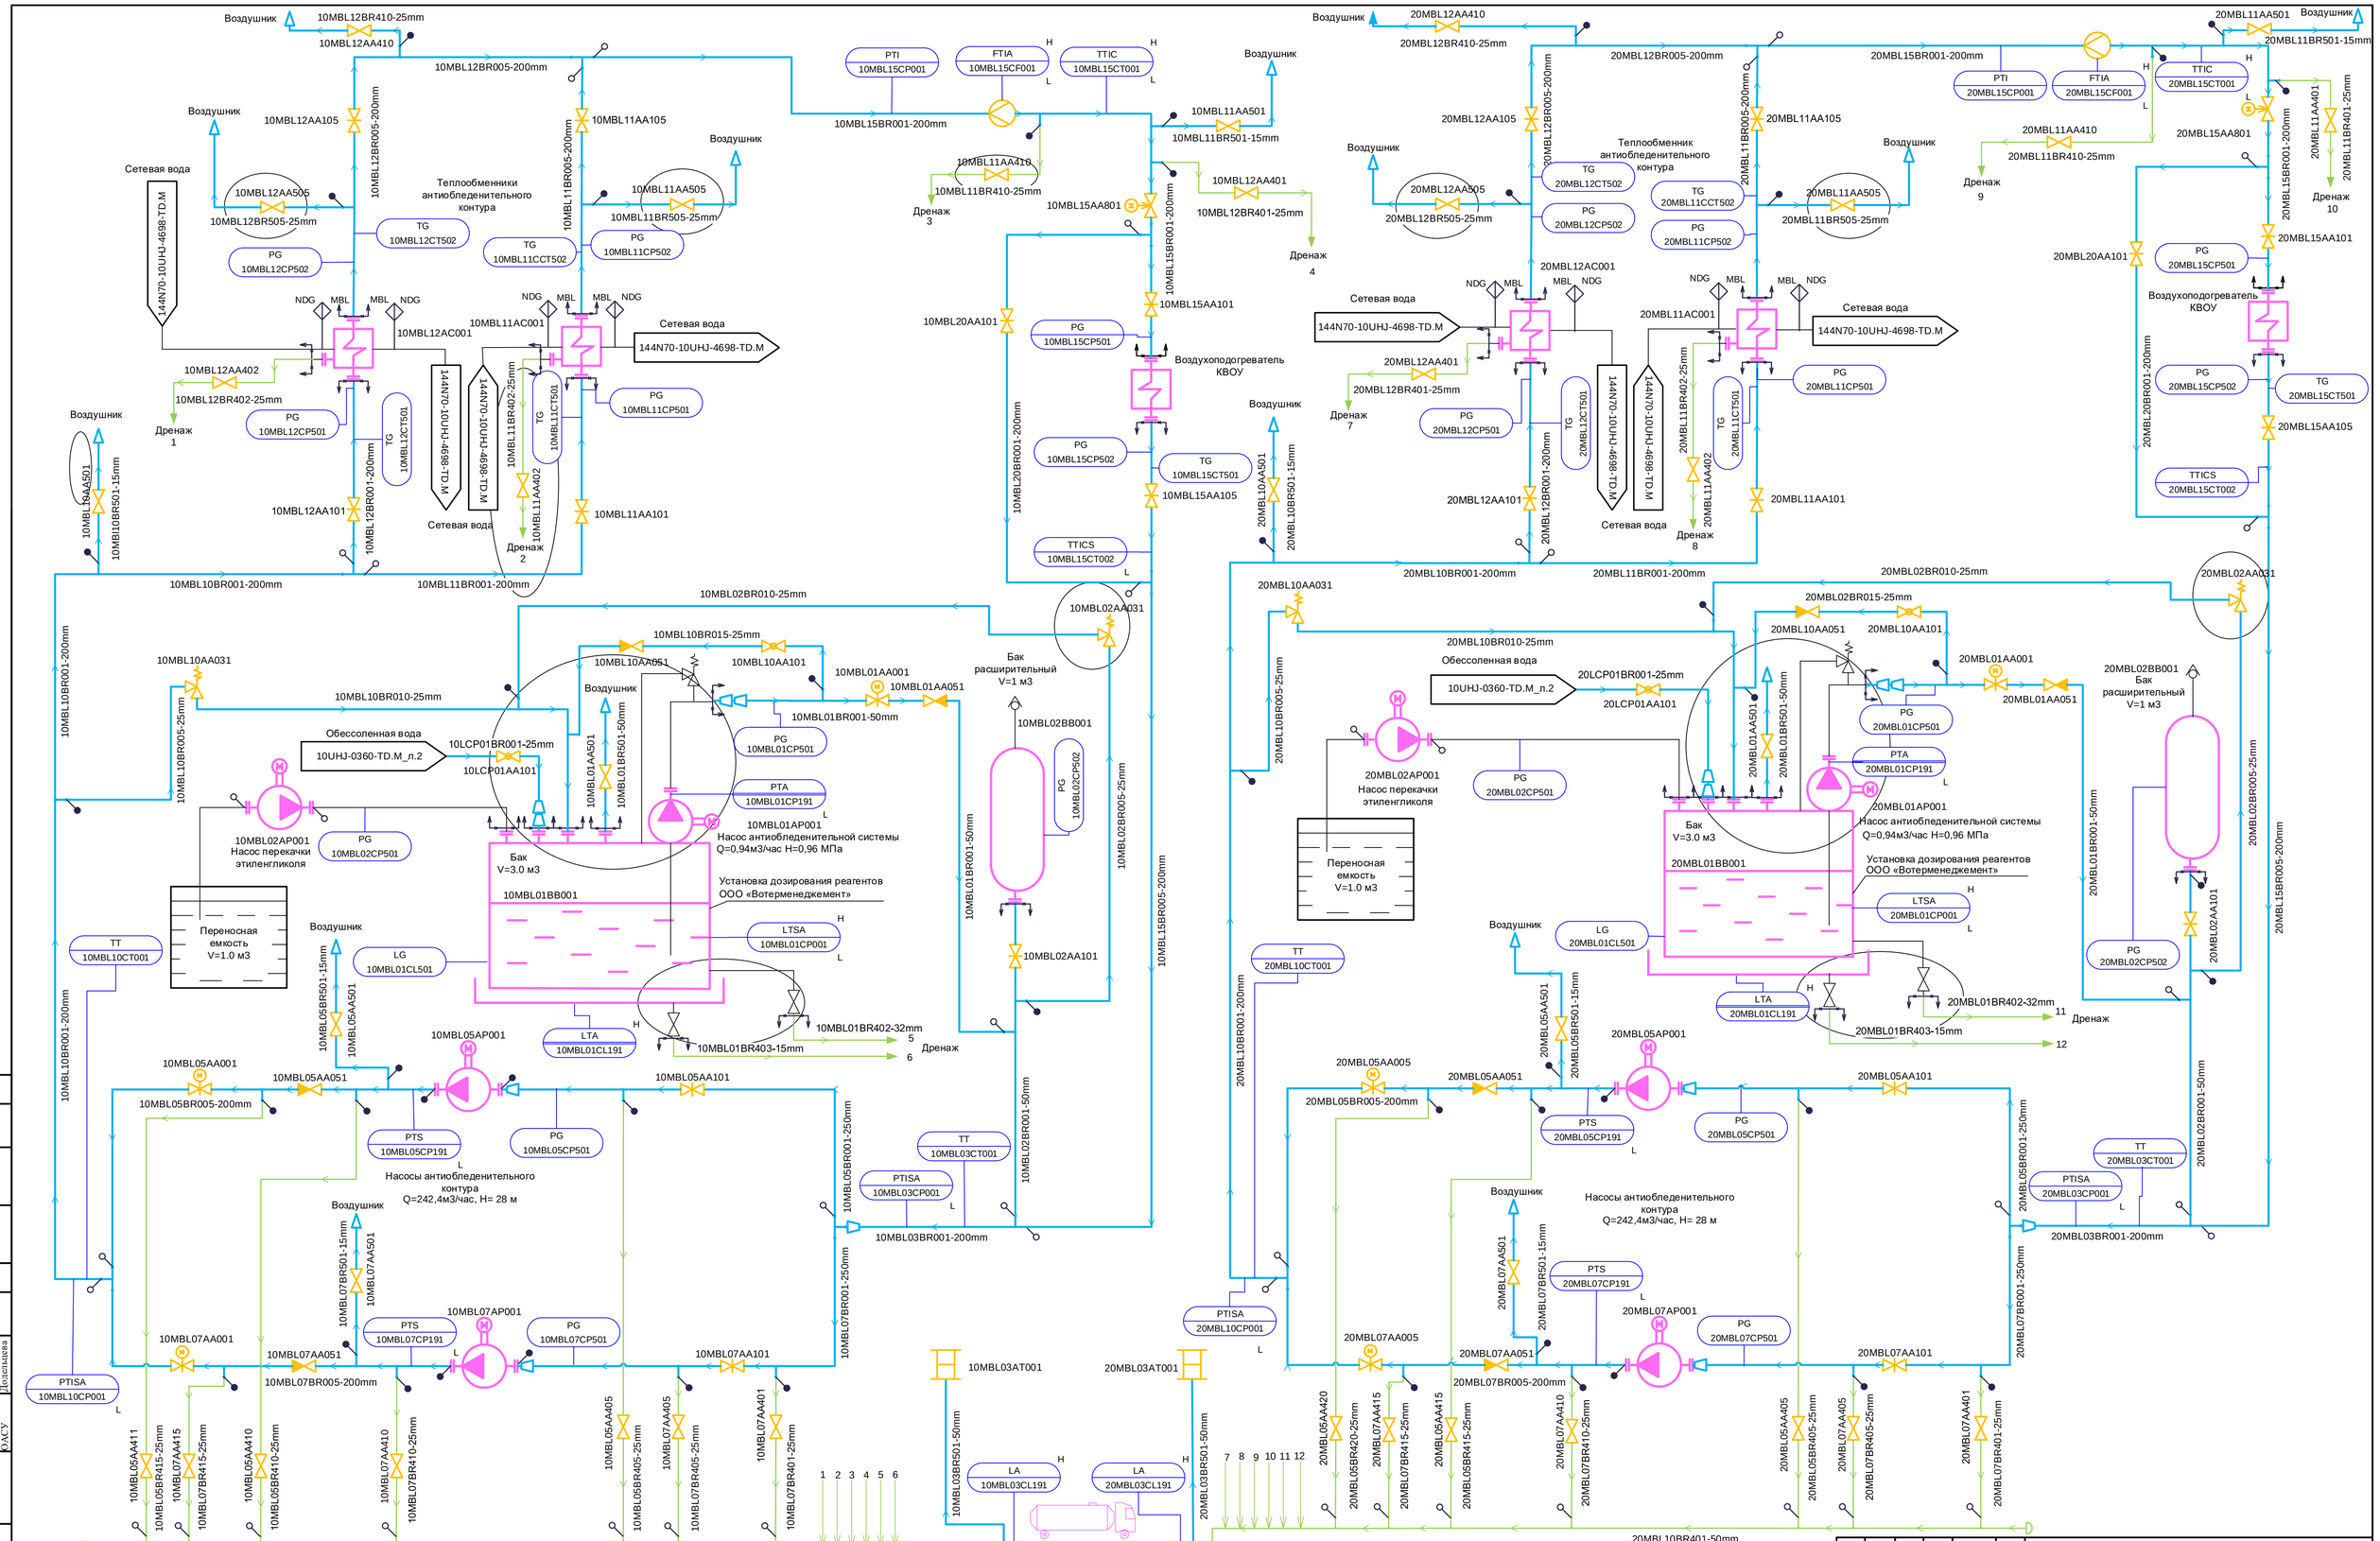


| | | | | | | |
|---|---|---|---|---|---|---|
| 1 | - | Зам. | 4488-25 | | 10.2025 | 144N70 – 10UHJ – 3692 – TD.M |
| Изм. | Кол.уч | Лист | № док. | Подп. | Дата | Строительство Артемовской ТЭЦ-2 с внеплощадочной инфраструктурой |
| Разработал | Полянская | | | | | Здание главного корпуса с баковым хозяйством. PI-диаграмма трубопроводов антиобледенительной системы |
| Проверил | Смирнова | | | | | Стадия: Р; Лист: 2; Листов: |
| Н. контр. | Черемушкина | | | | | PI-диаграмма трубопроводов антиобледенительной системы. Система MBL |

АКЦИОНЕРНОЕ ОБЩЕСТВО ИНСТИТУТ ТЕПЛОЭЛЕКТРОПРОЕКТ Г. МОСКВА

Согласовано | ОАСУ | Подпись и дата | Взам. инв. № | Инв. № подл.

Формат А1