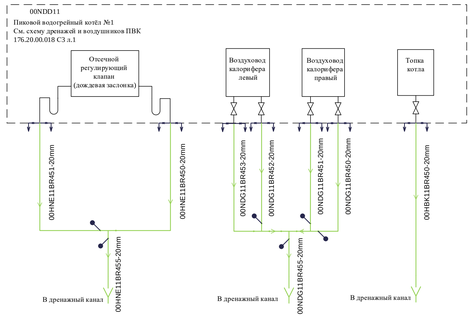


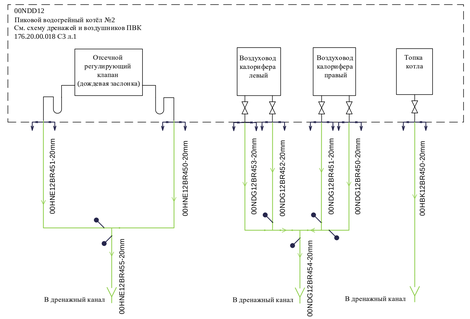


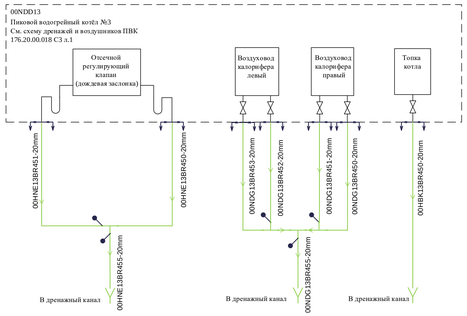


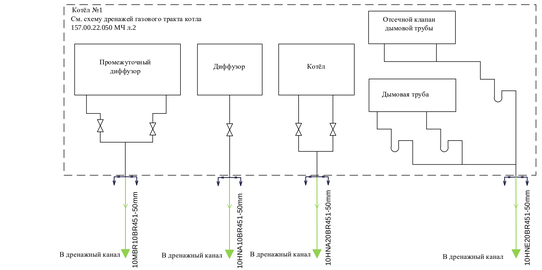


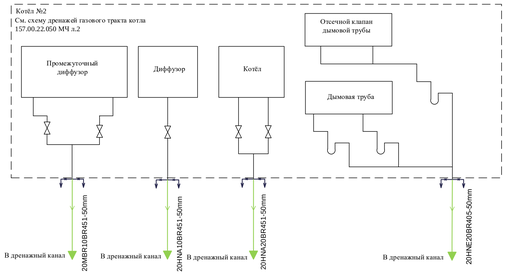


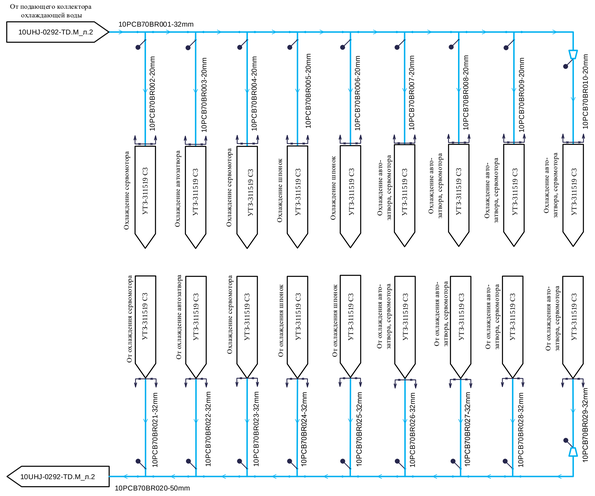


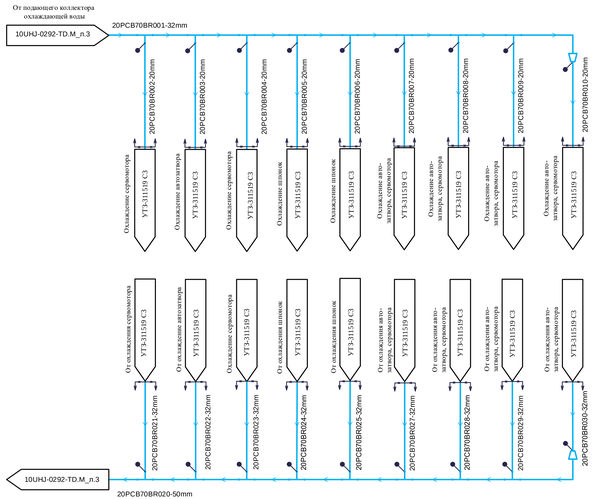


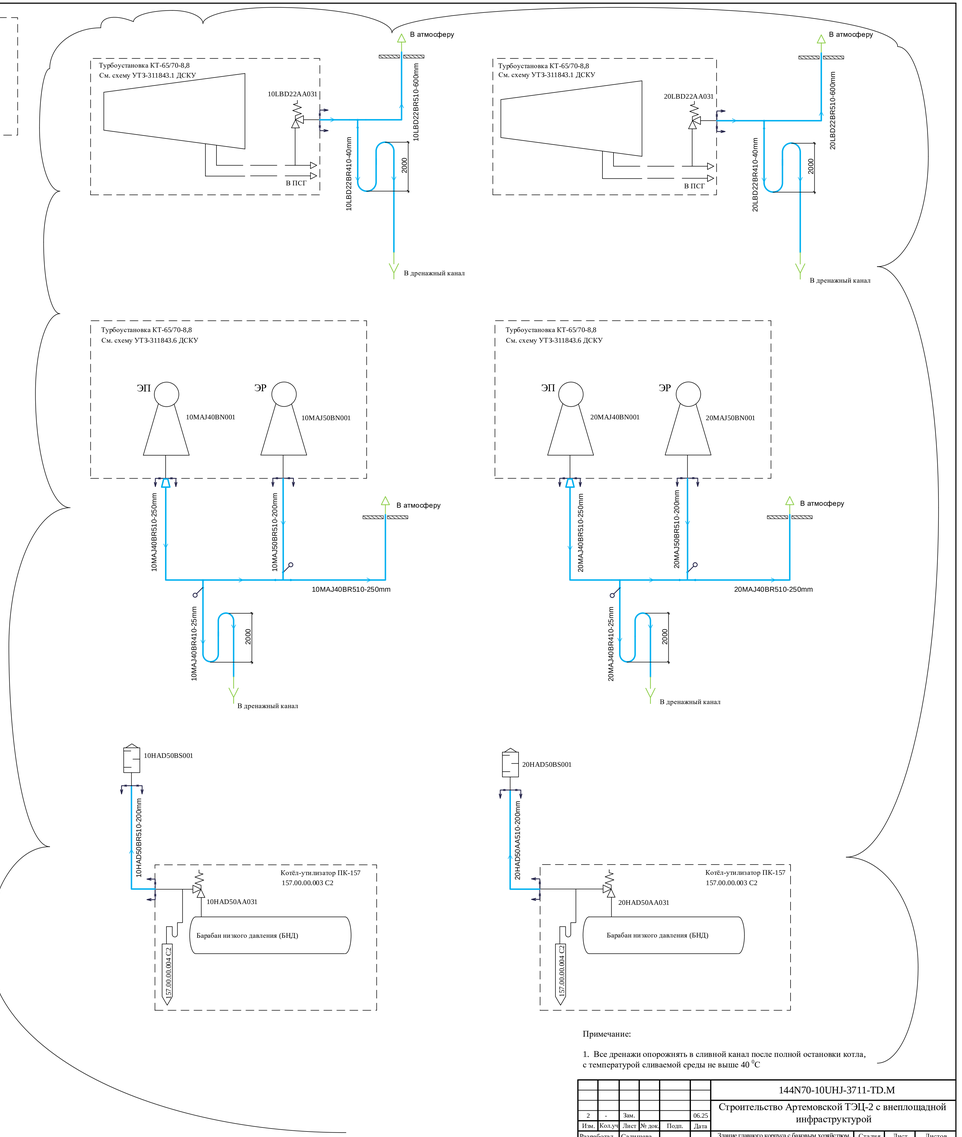


Примечание:

1. Все дренажи опорожнить в сливной канал после полной остановки котла, с температурой сливаемой среды не выше 40 °С

| | | | | | | | | | |
|---|---|---|---|---|---|---|---|---|---|
| | | | | | | 144N70-10UHJ-3711-TD.M | | | |
| | | | | | | Строительство Артемовской ТЭЦ-2 с внеплощадной инфраструктурой | | | |
| 2 | - | Зам. | | | 06.25 | | | | |
| Изм. | Кол.уч | Лист | № док. | Подп. | Дата | | | | |
| Разработал | | Селиверова | | | | Замок главного корпуса с банным хозяйством. PI-Диаграмма вспомогательных трубопроводов низкого давления | Стадия | Лист | Листов |
| Проверил | | Дёмина | | | | | Р | 2 | |
| Н. контр. | | Чернушкина | | | | PI-Диаграмма вспомогательных трубопроводов низкого давления. Система NDG, HBK, HNA, HNE, PCB | АКЦИОНЕРНОЕ ОБЩЕСТВО ТЕХНОПРОМЭКСПОРТ | | |

Согласовано

ОАОСУ

Взам. инв. №

Подпись и дата

Инв. № подл.

Формат А2х3