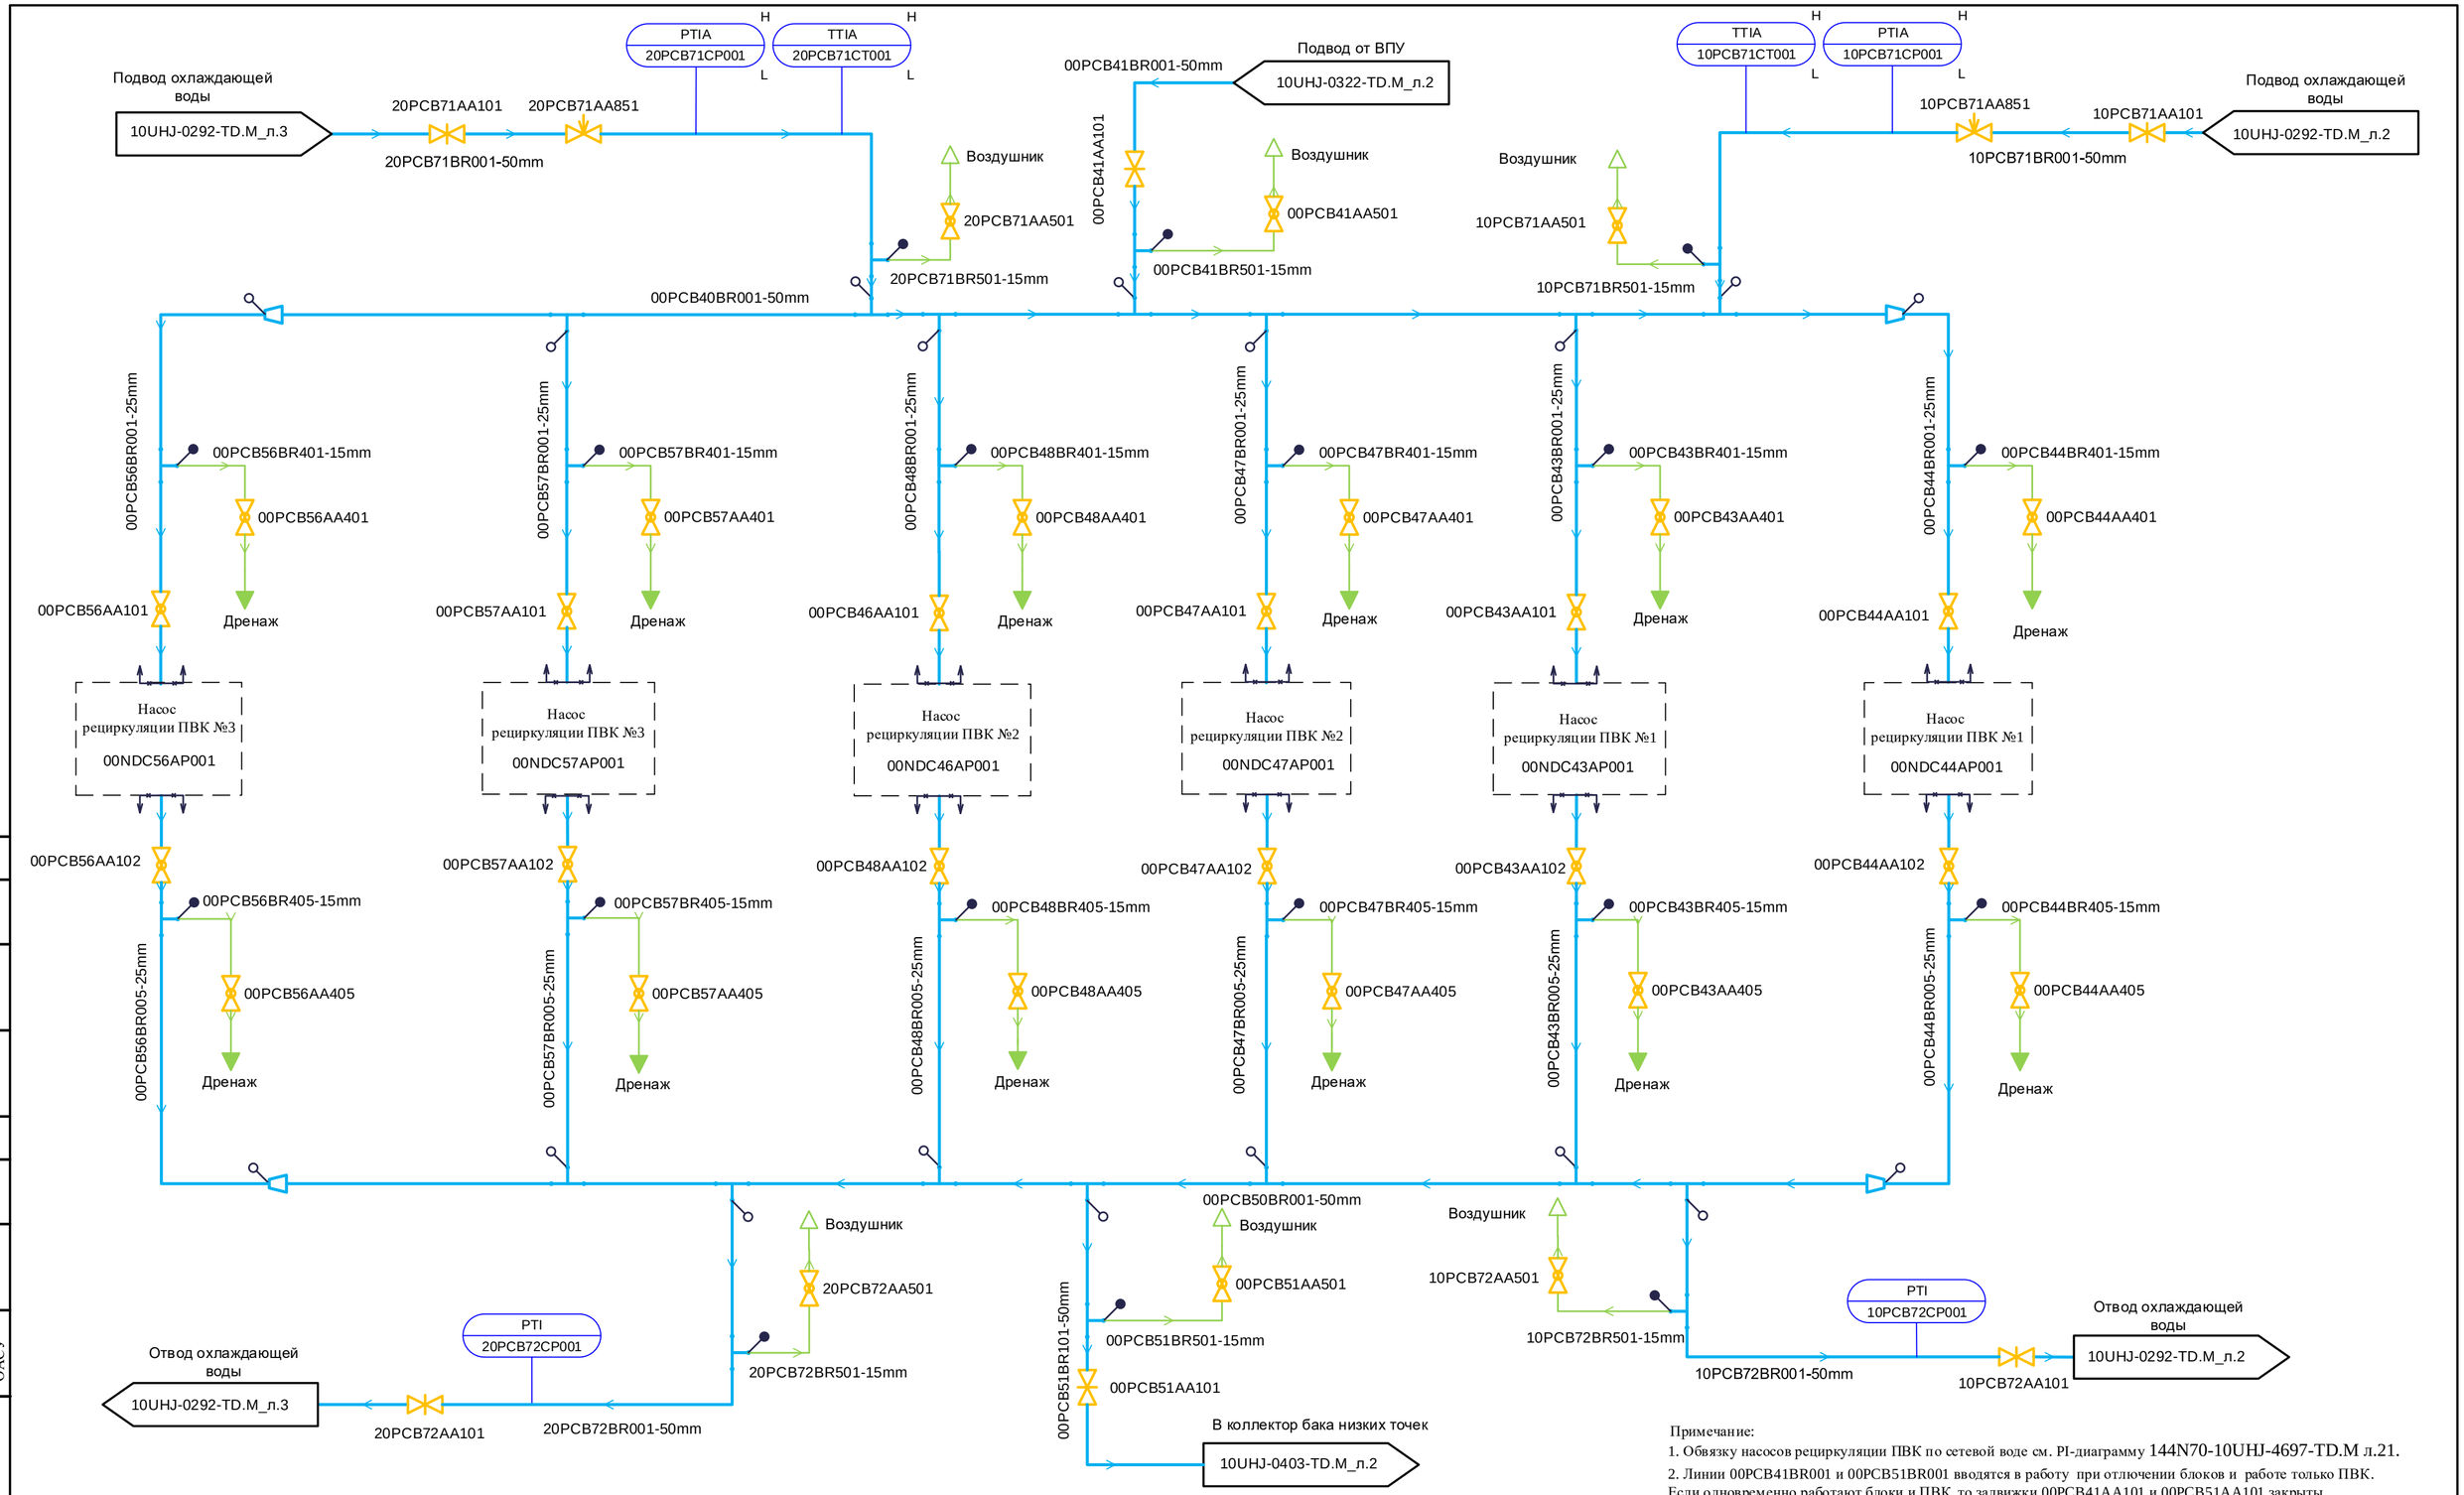

Примечание:

1. Обвязку насосов рециркуляции ПВК по сетевой воде см. PI-диаграмму 144N70-10UHJ-4697-TD.M л.21.
2. Линии 00PCB41BR001 и 00PCB51BR001 вводятся в работу при отключении блоков и работе только ПВК. Если одновременно работают блоки и ПВК, то задвижки 00PCB41AA101 и 00PCB51AA101 закрыты.

2	-	Нов.	6125-25		12.25	
Изм.	Кол.уч	Лист	№ док.	Подп.	Дата	
Разработал		Салищева				
Проверил		Дёмина				
Н. контр.		Черёмушкина				

144N70-10UHJ-3711-TD.M

Строительство Артемовской ТЭЦ-2 с внеплощадной инфраструктурой

Здание главного корпуса с баковым хозяйством. PI-Диаграмма вспомогательных трубопроводов низкого давления

Стадия	Лист	Листов
Р	3	

PI-Диаграмма вспомогательных трубопроводов низкого давления. Система РСВ

АКЦИОНЕРНОЕ ОБЩЕСТВО ИНСТИТУТ ТЕПЛОЭЛЕКТРОПРОЕКТ Г. МОСКВА

Согласовано

ОАСУ

Взам. инв. №

Подпись и дата

Инв. № подл.

Формат А2