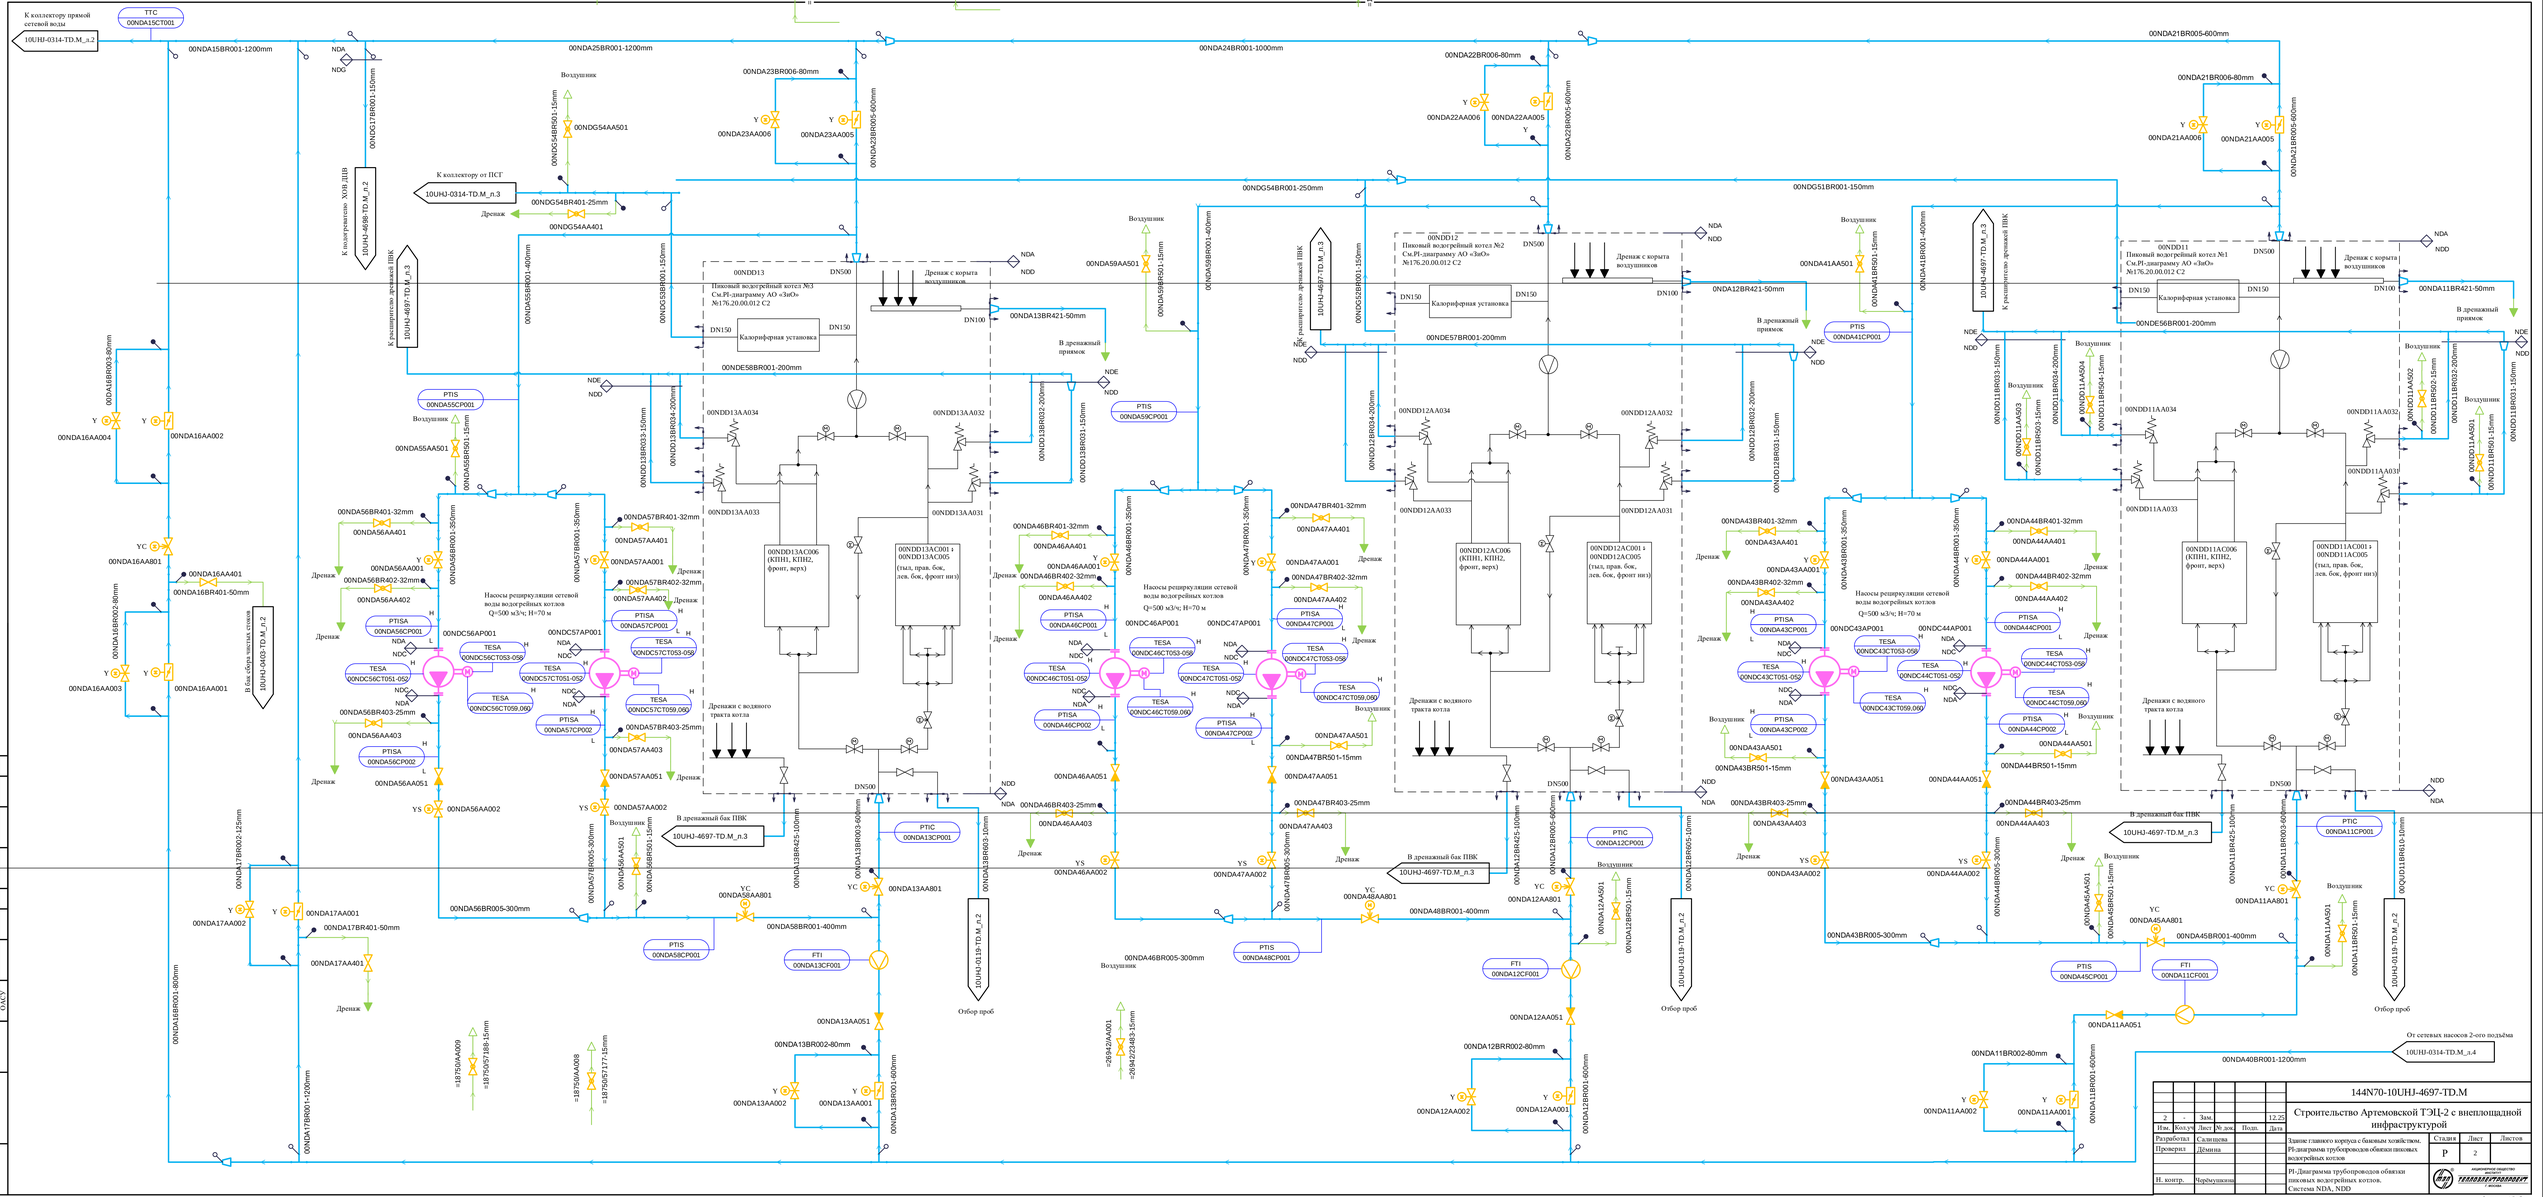
К коллектору прямой сетевой воды
10UHJ-0314-TD.M_л.2
TTC
00NDA15CT001
00NDA15BR001-1200mm
00NDA25BR001-1200mm
00NDA24BR001-1000mm
00NDA21BR005-600mm
00NDA21BR006-80mm
00NDA22BR006-80mm
00NDA23BR006-80mm
Воздушник
00NDG54AA501
К коллектору от ПСГ
10UHJ-0314-TD.M_л.3
Дренаж
00NDG54BR401-25mm
00NDG54AA401
00NDG51BR001-150mm
00NDG54BR001-250mm
К энергоблоку ХОВ ДПВ
10UHJ-4698-TD.M_л.2
К расширителю дренажей ПВК
10UHJ-4697-TD.M_л.3
00NDD13
Пиковый водогрейный котел №3
См.PI-диаграмму АО «ЗиО»
№176.20.00.012 С2
Калориферная установка
00NDE58BR001-200mm
00NDD12
Пиковый водогрейный котел №2
См.PI-диаграмму АО «ЗиО»
№176.20.00.012 С2
00NDE57BR001-200mm
00NDD11
Пиковый водогрейный котел №1
См.PI-диаграмму АО «ЗиО»
№176.20.00.012 С2
00NDE56BR001-200mm
Дренаж с корыта воздушников
00NDA13BR421-50mm
00NDA12BR421-50mm
00NDA11BR421-50mm
В дренажный приямок
00NDA41AA501
00NDA59AA501
PTIS
00NDA55CP001
00NDA59CP001
00NDA41CP001
00NDA16AA004
00NDA16AA002
00NDA16AA801
00NDA16AA401
00NDA16BR401-50mm
00NDA16BR003-80mm
00NDA16BR002-80mm
00NDA16AA003
00NDA16AA001
К блок сборки чистых конденсатов
10UHJ-0465-TD.M_л.2
00NDA56BR401-32mm
00NDA56AA401
00NDA56AA001
00NDA58BR402-32mm
00NDA56AA402
00NDA56BR403-25mm
00NDA56AA403
00NDA56AA051
00NDA56AA002
00NDA57BR401-32mm
00NDA57AA401
00NDA57AA001
00NDA57BR402-32mm
00NDA57AA402
00NDA57BR403-25mm
00NDA57AA403
00NDA57AA051
00NDA57AA002
Насосы рециркуляции сетевой воды водогрейных котлов
Q=500 м3/ч; H=70 м
00NDC56AP001
00NDC57AP001
00NDC46AP001
00NDC47AP001
00NDC43AP001
00NDC44AP001
00NDD13AC006 (КПН1, КПН2, фронт, верх)
00NDD13AC001 и 00NDD13AC005 (тыл, прав. бок, лев. бок, фронт низ)
00NDD12AC006 (КПН1, КПН2, фронт, верх)
00NDD12AC001 и 00NDD12AC005 (тыл, прав. бок, лев. бок, фронт низ)
00NDD11AC006 (КПН1, КПН2, фронт, верх)
00NDD11AC001 и 00NDD11AC005 (тыл, прав. бок, лев. бок, фронт низ)
Дренажи с водяного тракта котла
00NDA46BR401-32mm
00NDA46AA401
00NDA46AA001
00NDA46BR402-32mm
00NDA46AA402
00NDA46BR403-25mm
00NDA46AA403
00NDA46AA051
00NDA46AA002
00NDA47BR401-32mm
00NDA47AA401
00NDA47AA001
00NDA47BR402-32mm
00NDA47AA402
00NDA47BR403-25mm
00NDA47AA403
00NDA47AA051
00NDA47AA002
00NDA47AA501
00NDA47BR501-15mm
00NDA43BR401-32mm
00NDA43AA401
00NDA43AA001
00NDA43BR402-32mm
00NDA43AA402
00NDA43BR403-25mm
00NDA43AA403
00NDA43AA051
00NDA43AA002
00NDA43AA501
00NDA43BR501-15mm
00NDA44BR401-32mm
00NDA44AA401
00NDA44AA001
00NDA44BR402-32mm
00NDA44AA402
00NDA44BR403-25mm
00NDA44AA403
00NDA44AA051
00NDA44AA002
00NDA44AA501
00NDA44BR501-15mm
В дренажный бак ПВК
10UHJ-4697-TD.M_л.3
00NDA17AA001
00NDA17AA002
00NDA17BR401-50mm
00NDA17AA401
00NDA17BR001-1200mm
00NDA18BR001-800mm
00NDA56BR005-300mm
00NDA58BR001-400mm
00NDA58AA801
00NDA13AA801
00NDA13AA051
00NDA13BR002-80mm
00NDA13AA002
00NDA13AA001
00NDA13BR001-600mm
00NDA46BR005-300mm
00NDA48BR001-400mm
00NDA48AA801
00NDA12AA801
00NDA12AA051
00NDA12BR002-80mm
00NDA12AA002
00NDA12AA001
00NDA12BR001-600mm
00NDA43BR005-300mm
00NDA45AA801
00NDA45BR001-400mm
00NDA11AA051
00NDA11BR002-80mm
00NDA11AA002
00NDA11AA001
00NDA11BR001-600mm
00NDA40BR001-1200mm
От сетевых насосов 2-ого подъёма
10UHJ-0314-TD.M_л.4
PTIS
00NDA58CP001
00NDA48CP001
00NDA12CF001
00NDA45CP001
00NDA11CF001
FTI
00NDA13CF001
PTIC
00NDA13CP001
00NDA12CP001
00NDA11CP001
10UHJ-0119-TD.M_л.2
Отбор проб
=187509AA009
=187509/189-15mm
=187509AA008
=187509/177-15mm
=269423AA001
=269423/483-15mm
144N70-10UHJ-4697-TD.M
Строительство Артемовской ТЭЦ-2 с внеплощадной инфраструктурой
Здание главного корпуса с банным хозяйством.
PI-диаграмма трубопроводов обвязки пиковых водогрейных котлов
PI-Диаграмма трубопроводов обвязки пиковых водогрейных котлов.
Система NDA, NDD
Стадия
Лист
Листов
Р
2
Разработал
Проверил
Н. контр.
Согласовано
Взам. инв. №
Подпись и дата
Инв. № подл.
Формат А2х3