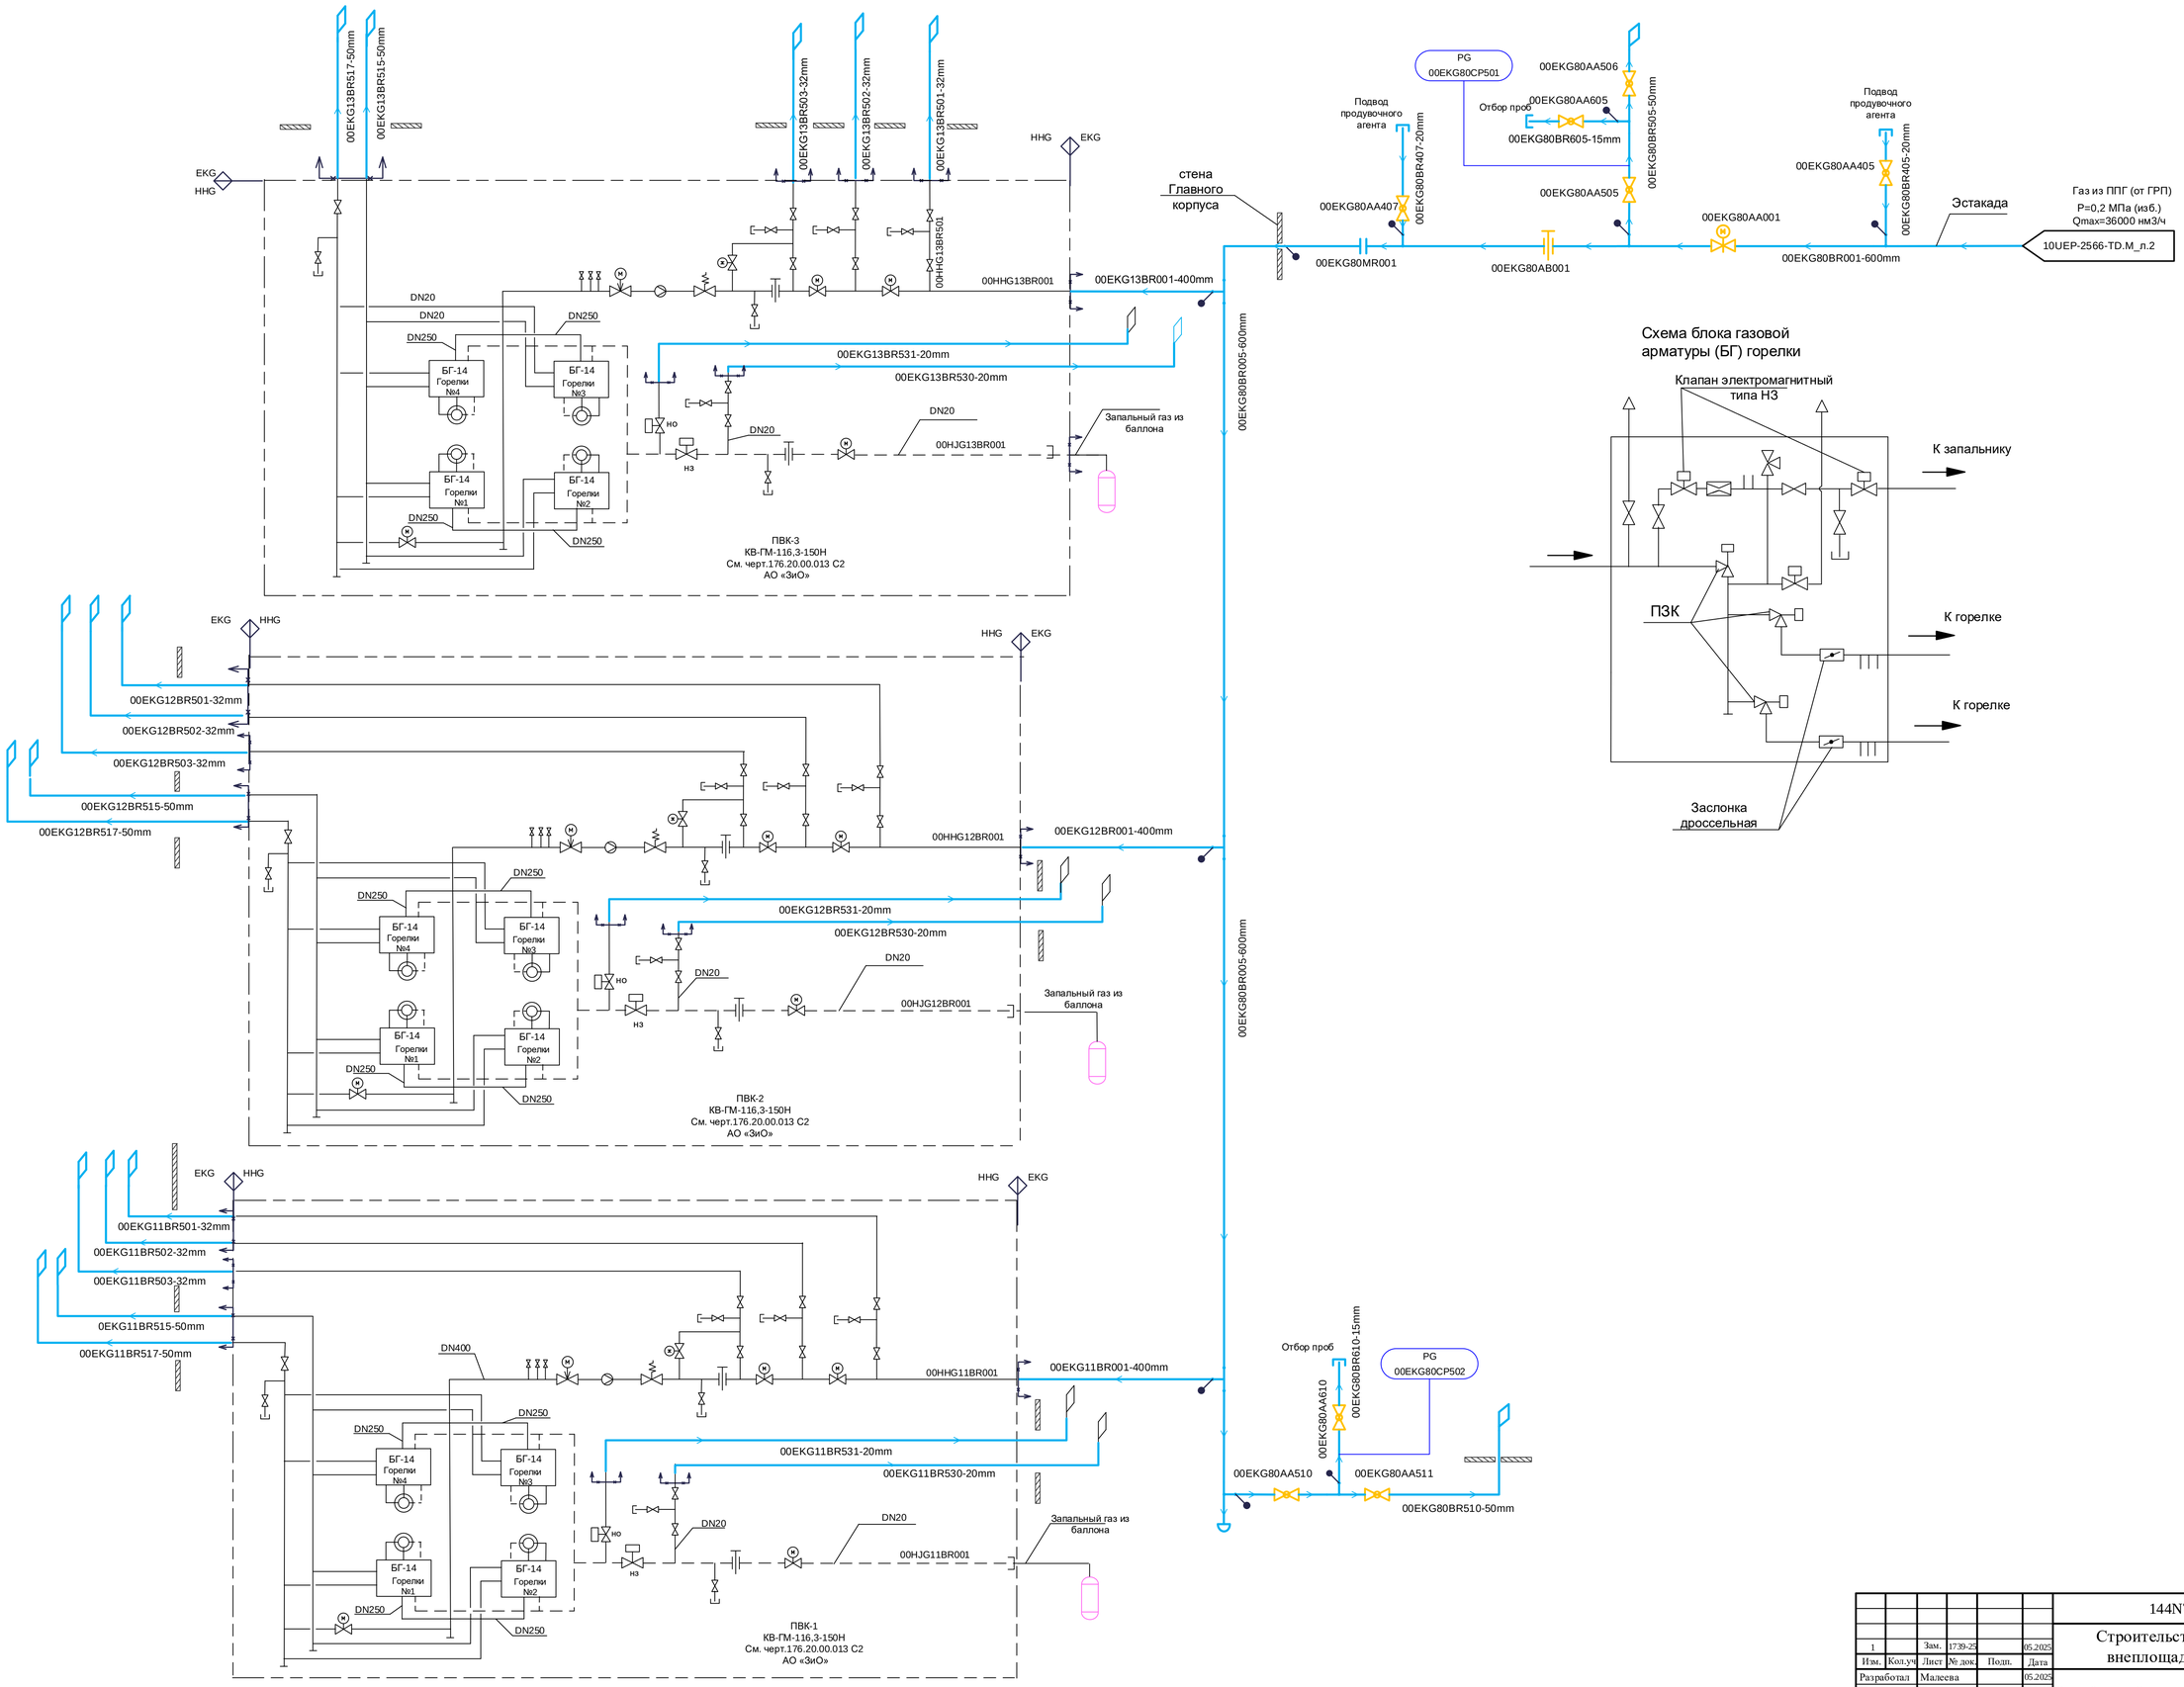

1		Зам.	17.39-25		05.2025	144N70-10UHJ-4778-TD.M
Изм.	Кол.уч	Лист	№ док.	Подп.	Дата	Строительство Артемовской ТЭЦ-2 с внеплощадочной инфраструктурой
Разработал		Малеева			05.2025	Главный корпус. Газопроводы
Проверил		Смирнова			05.2025	Стадия: Р; Лист: 2; Листов:
Нач. отдела		Мухаммадеев			05.2025	
Н. контр.		Черемушкина			05.2025	Р-I Диаграмма трубопроводов газового топлива. Газопроводы к ПВК

АКЦИОНЕРНОЕ ОБЩЕСТВО ИНСТИТУТ ТЕПЛОЭЛЕКТРОПРОЕКТ г. МОСКВА

Согласовано

Взам. инв. №

Подпись и дата

Инв. № подл.

Формат А1