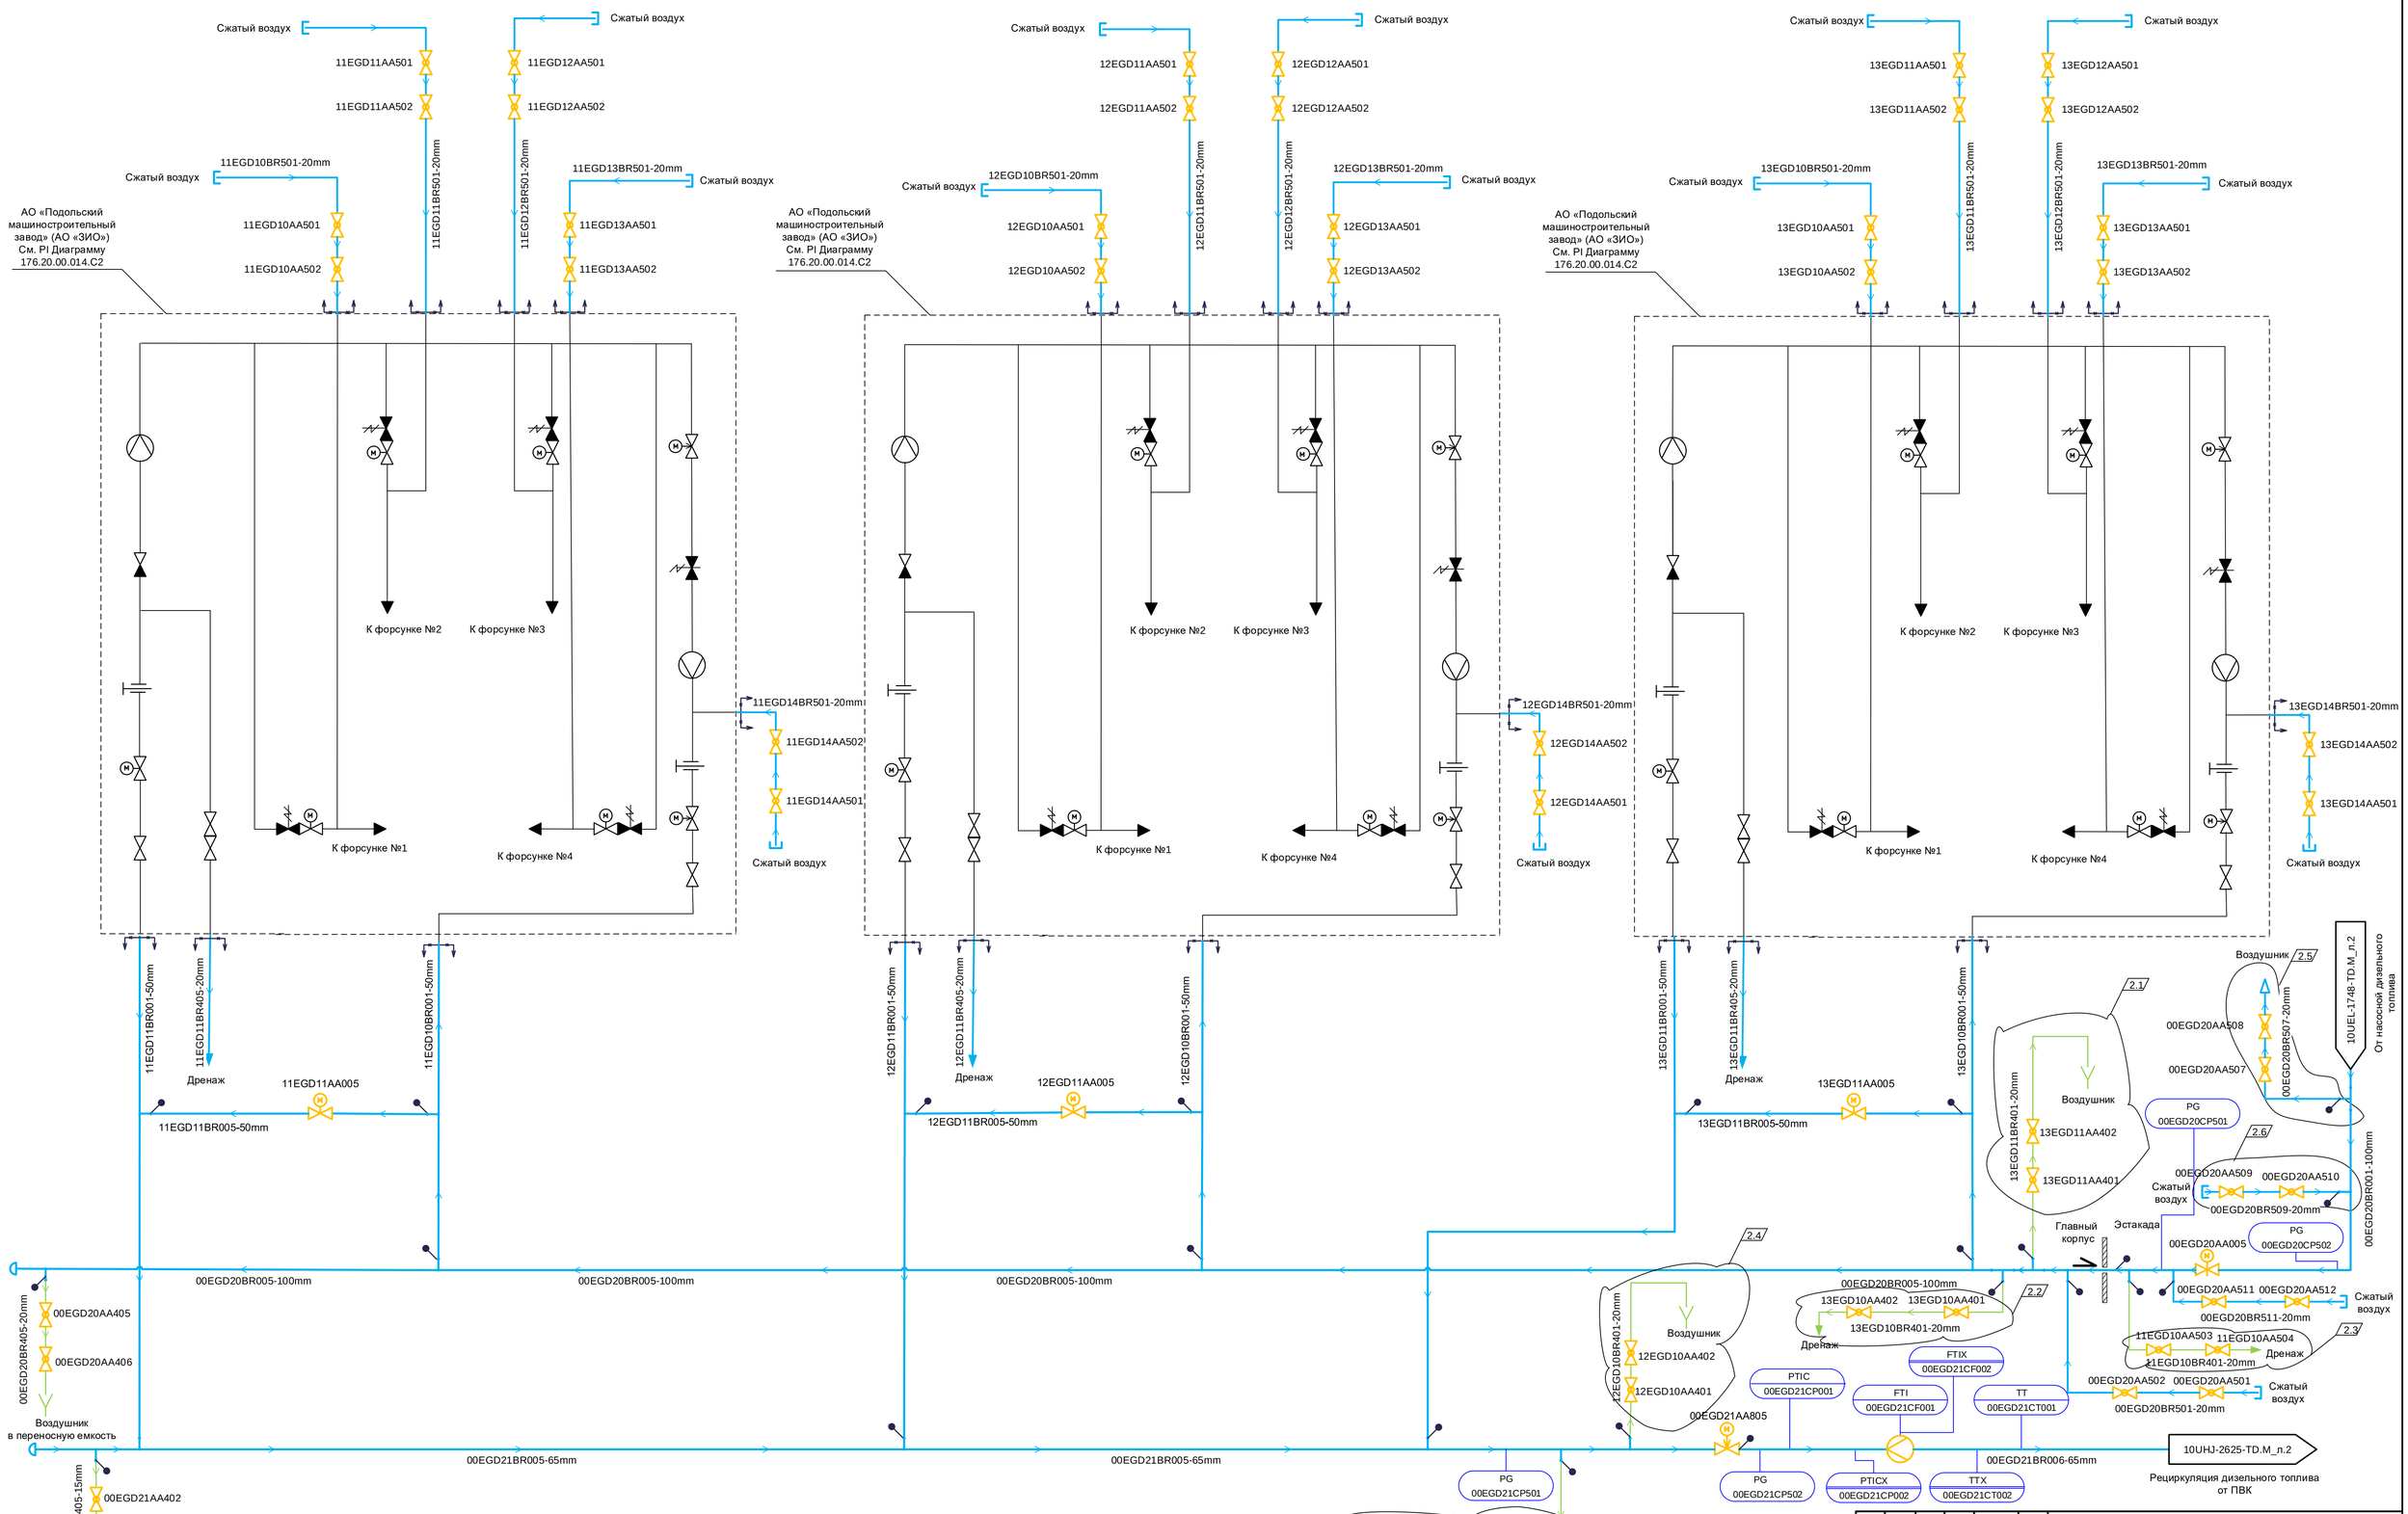

2	6	Зам	4488-25		10.2025	144N70 – 10UHJ – 4781 – TD.M
Изм.	Кол.уч	Лист	№ док.	Подп.	Дата	Строительство Артемовской ТЭЦ-2 с внеплощадочной инфраструктурой
Разработал		Полянская			10.2025	Здание главного корпуса с баковым хозяйством. PI-диаграмма трубопроводов дизельного топлива на ПВК.
Проверил		Смирнова			10.2025	Стадия: Р; Лист: 2; Листов:
Н. контр.		Черемушкина			10.2025	PI-диаграмма трубопроводов дизельного топлива на ПВК. Система EGD.

АКЦИОНЕРНОЕ ОБЩЕСТВО ИНСТИТУТ ТЕПЛОЭЛЕКТРОПРОЕКТ г. МОСКВА

Согласовано

ОАСУ	Доценцева

Взам. инв. №

Подпись и дата

Инв. № подл.

Формат А1