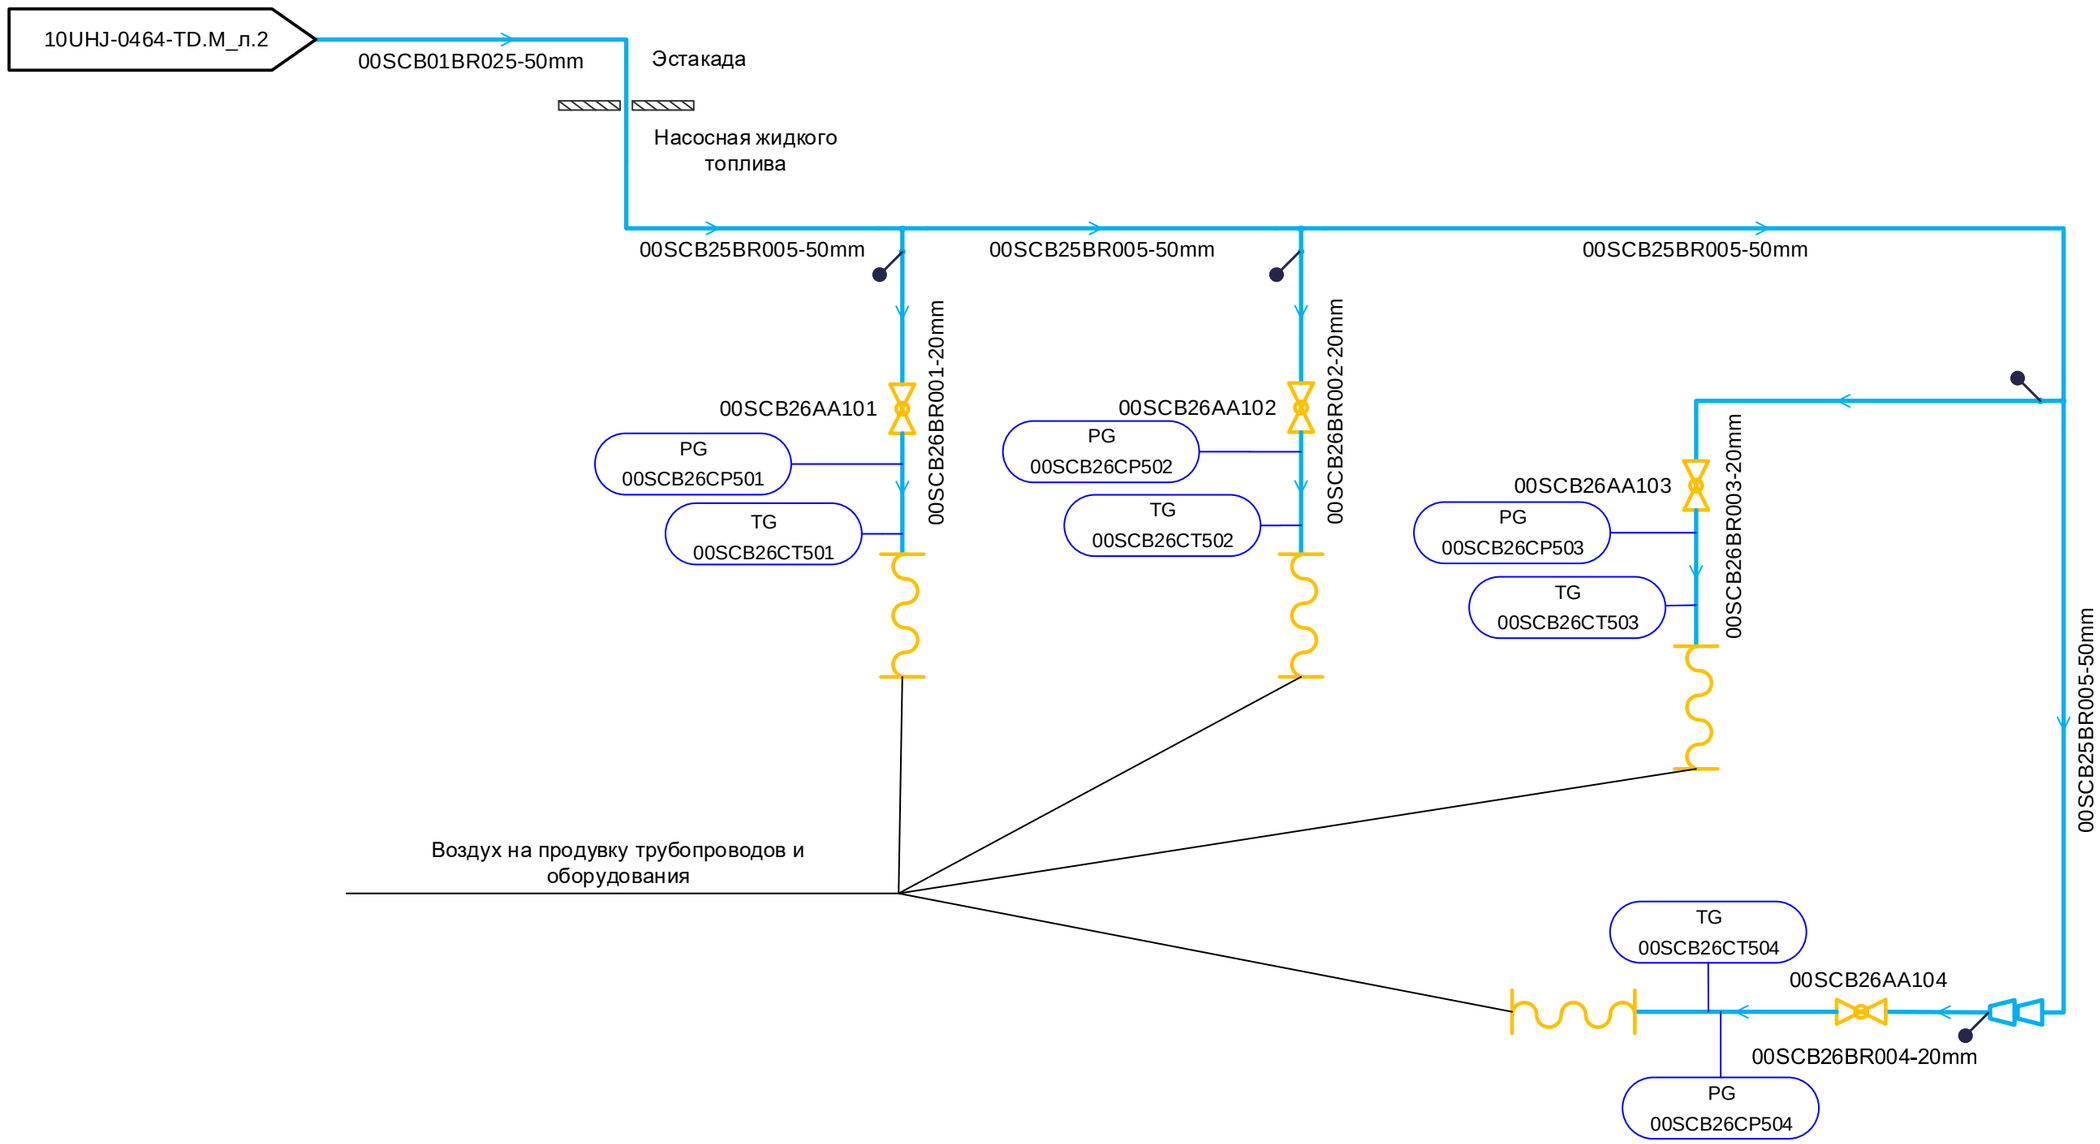

Примечание:
Температура воздуха от компрессорной не должна превышать 40°С

Изм.	Кол.уч	Лист	№ док.	Подп.	Дата
Разработал		Полянская			
Проверил		Смирнова			
Н. контр.		Черемушкина			

144N70-10UEL-5229-TD.M

Артемовская ТЭЦ-2 с внеплощадочной инфраструктурой

Насосная станция жидкого топлива со складом масла в мелкой таре.
PI-диаграмма трубопроводов сжатого воздуха

Стадия	Лист	Листов
Р	2	

PI-диаграмма трубопроводов сжатого воздуха. Система SCB.

АКЦИОНЕРНОЕ ОБЩЕСТВО ИНСТИТУТ ТЕПЛОЭЛЕКТРОПРОЕКТ Г. МОСКВА

Согласовано
Додельцева
ОАСУ
Взам. инв. №
Подпись и дата
Инв. № подл.

Формат А3