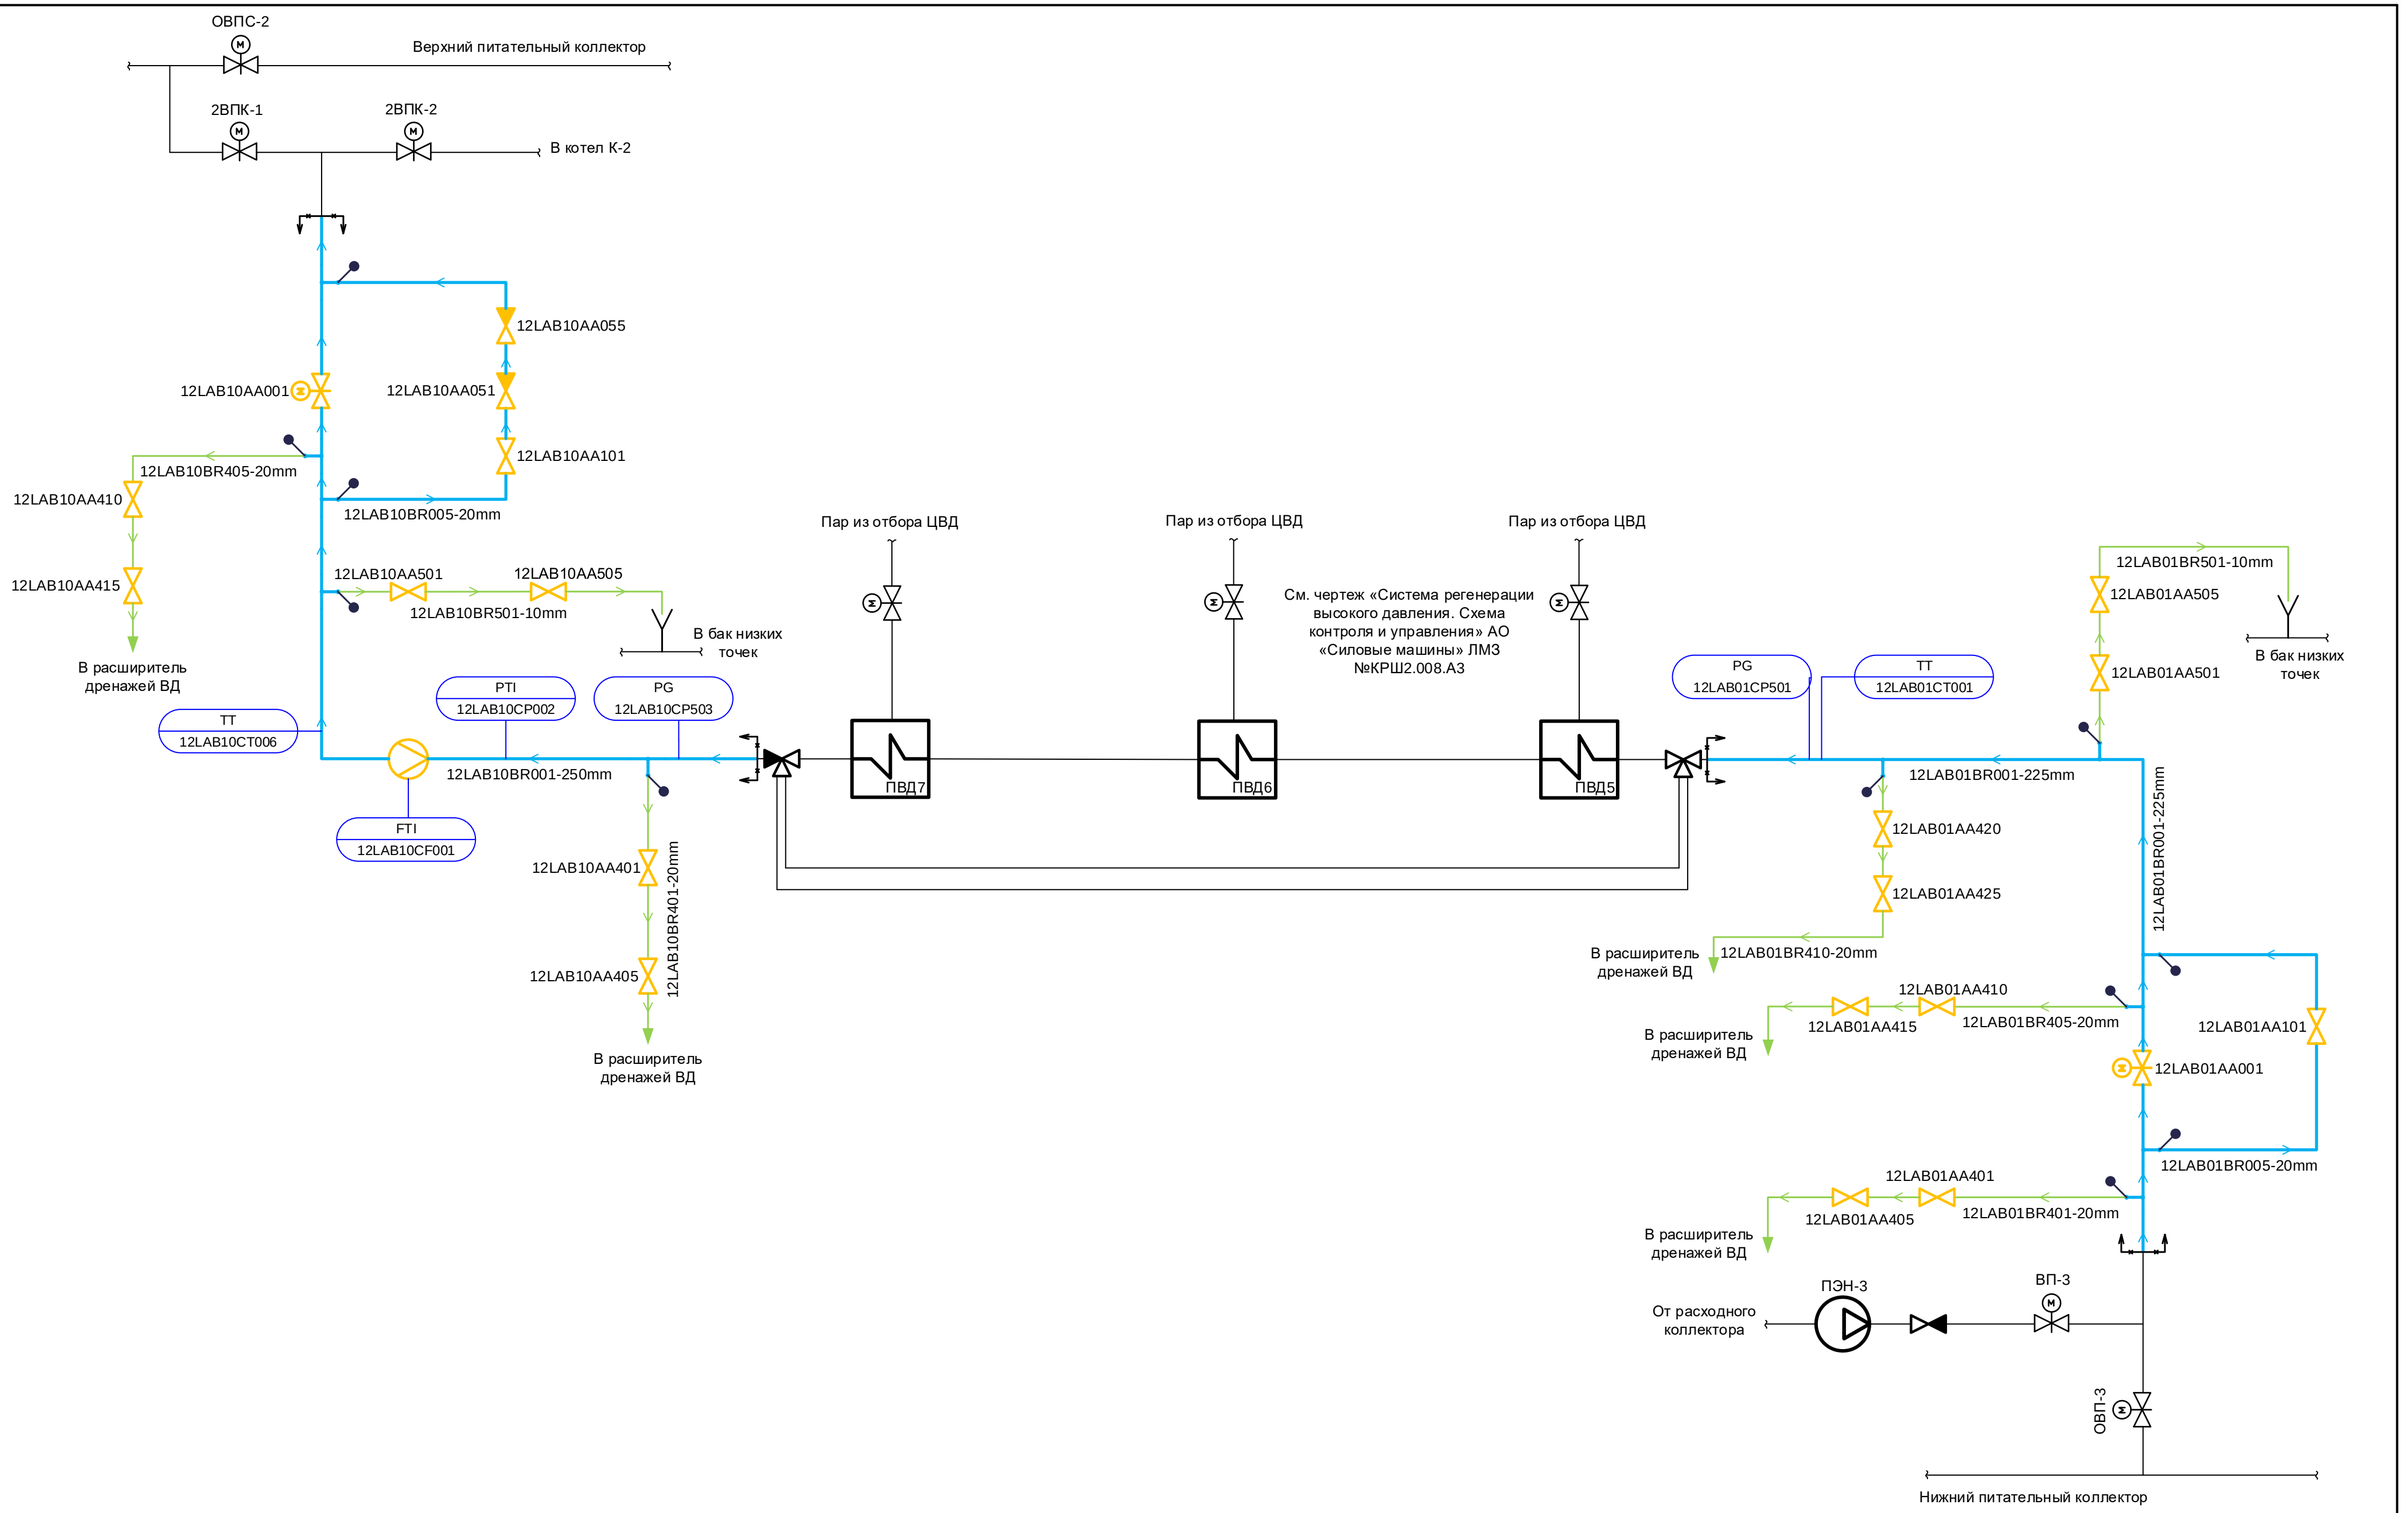

Изм.	Кол.уч	Лист	№ док.	Подп.	Дата	181M1D – 10UHJ – 1353 – TD.M
						Модернизация генерирующего объекта Киришская ГРЭС (Г-2т)
Разработал		Брылева				Главный корпус. PI-диаграмма трубопроводов питательной воды
Проверил		Супонина				Стадия: Р; Лист: 2; Листов:
Н. контр.		Гридчина				PI-диаграмма трубопроводов питательной воды. Система LAB
						АКЦИОНЕРНОЕ ОБЩЕСТВО ИНСТИТУТ ТЕПЛОЭЛЕКТРОПРОЕКТ Г. МОСКВА

Согласовано

ОАСУ

Взам. инв. №

Подпись и дата

Инв. № подл.

Формат А2