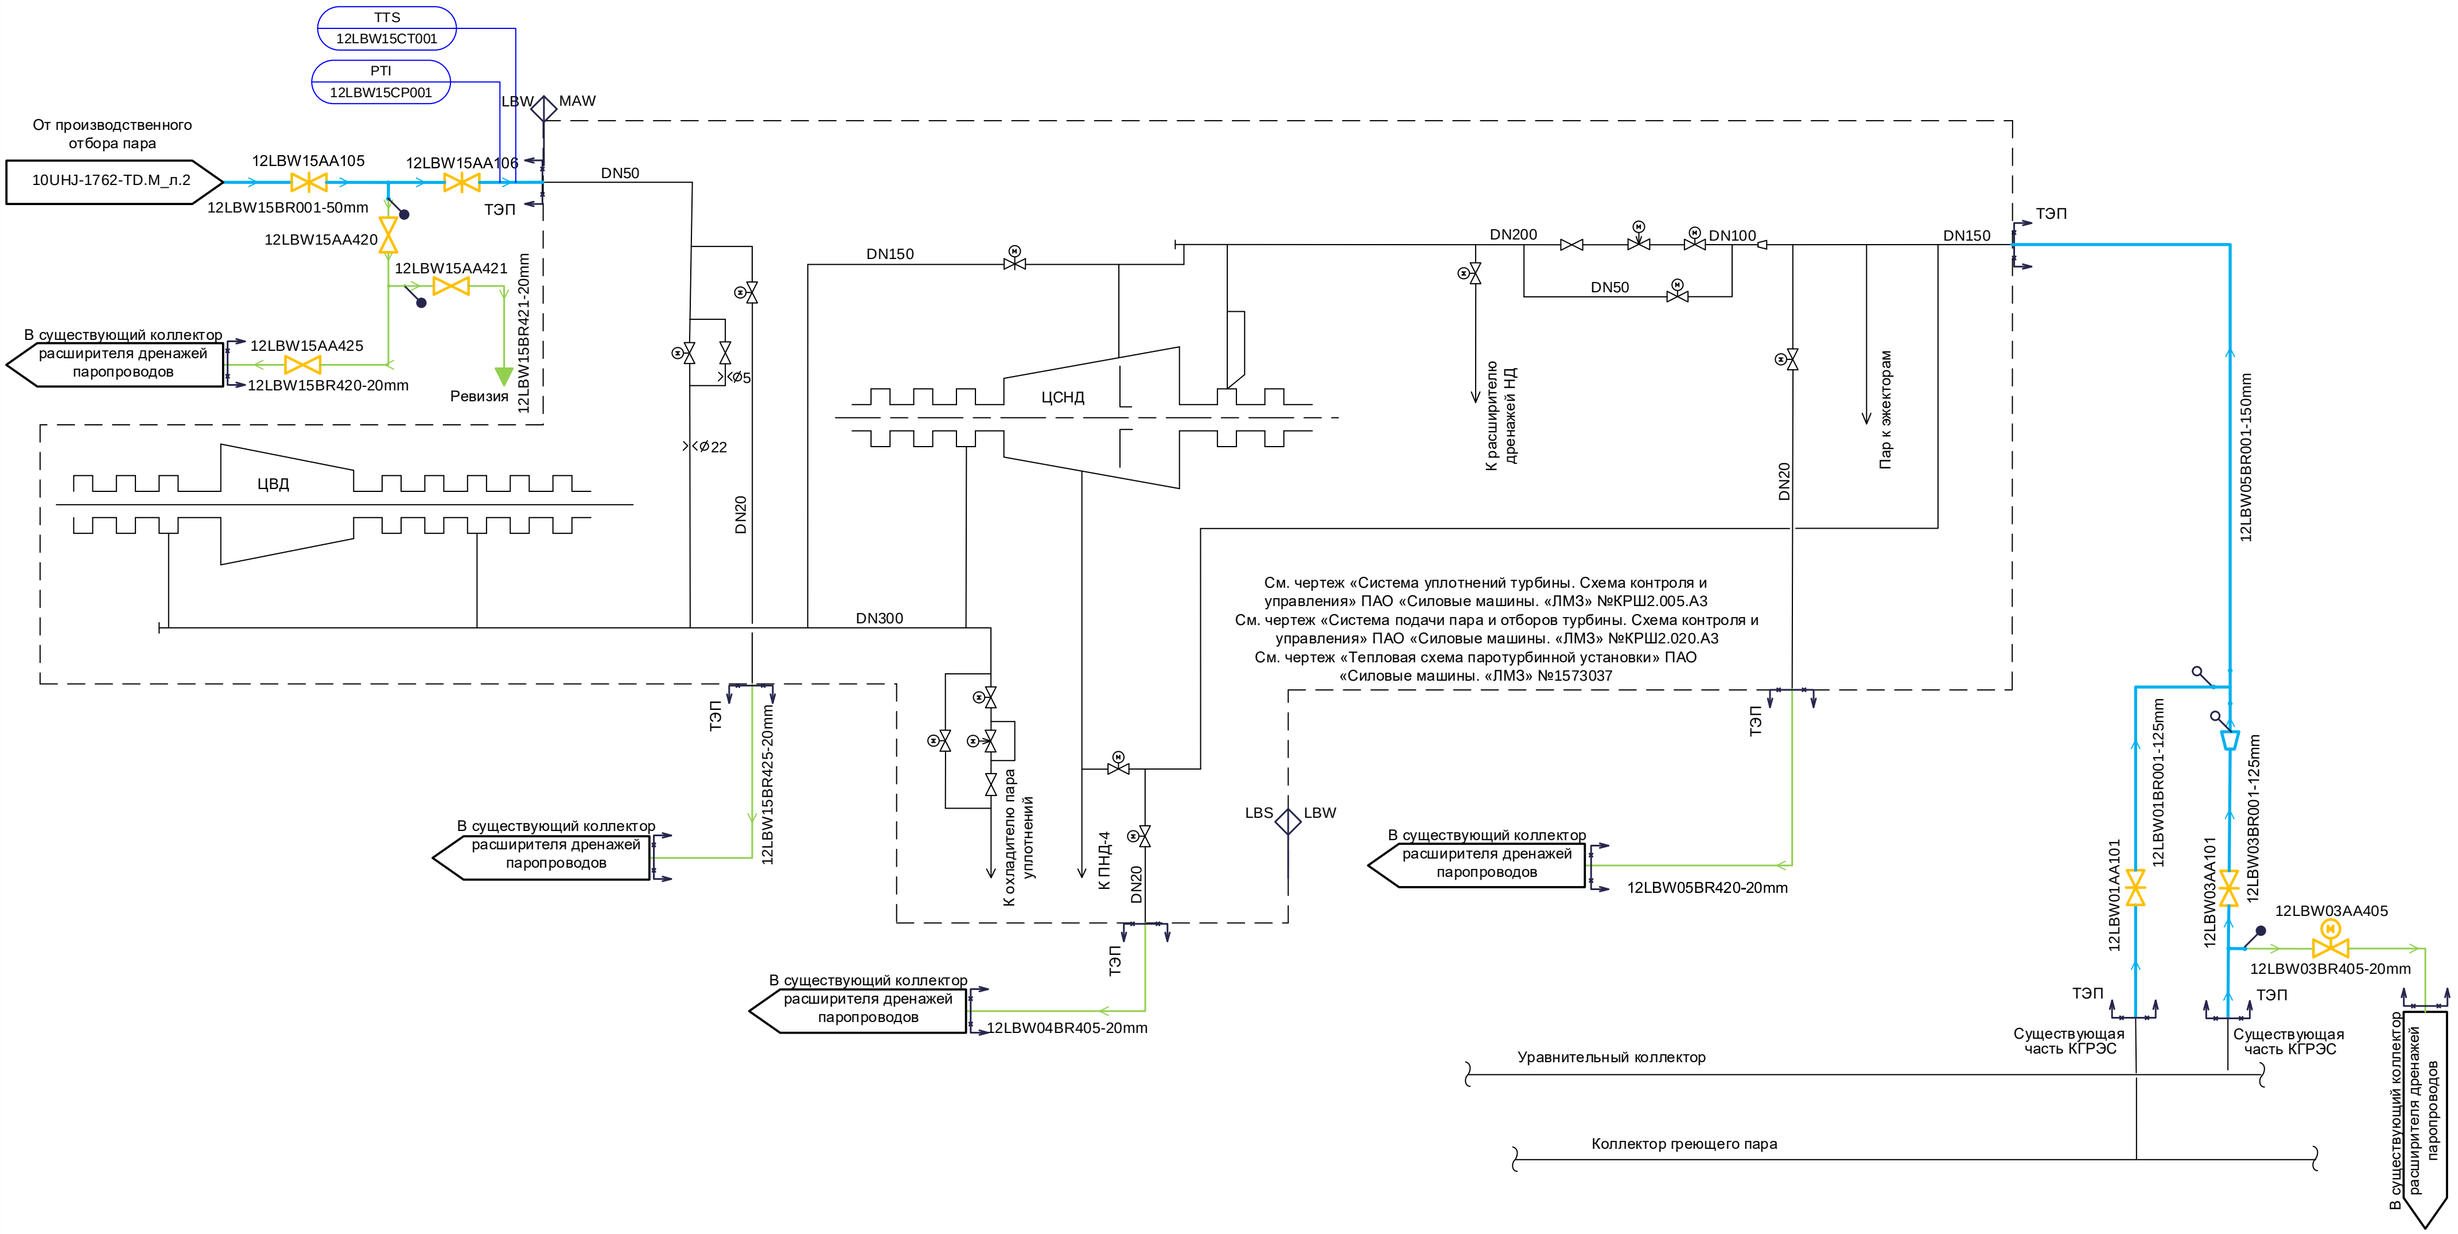

ТЭП

- граница проектирования

2	-	Зам.	487-21			
Изм.	Кол.уч	Лист	№ док.	Подп.	Дата	
Разработал		Архипова				
Проверил		Супонина				
Н. контр.		Астраханцев				

181M1D – 10UHJ – 1355 – TD.M

Модернизация генерирующего объекта Киришская ГРЭС (Г-2т)

Главный корпус. PI-Диаграмма. Система уплотняющего пара.

Стадия	Лист	Листов
Р	2	

PI-диаграмма трубопроводов подачи пара на уплотнения турбоагрегата. Система LBW

АКЦИОНЕРНОЕ ОБЩЕСТВО ИНСТИТУТ ТЕПЛОЭЛЕКТРОПРОЕКТ Г. МОСКВА

Согласовано

ОАСУ Соболева

Взам. инв. №

Подпись и дата

Инв. № подл.

Формат А2