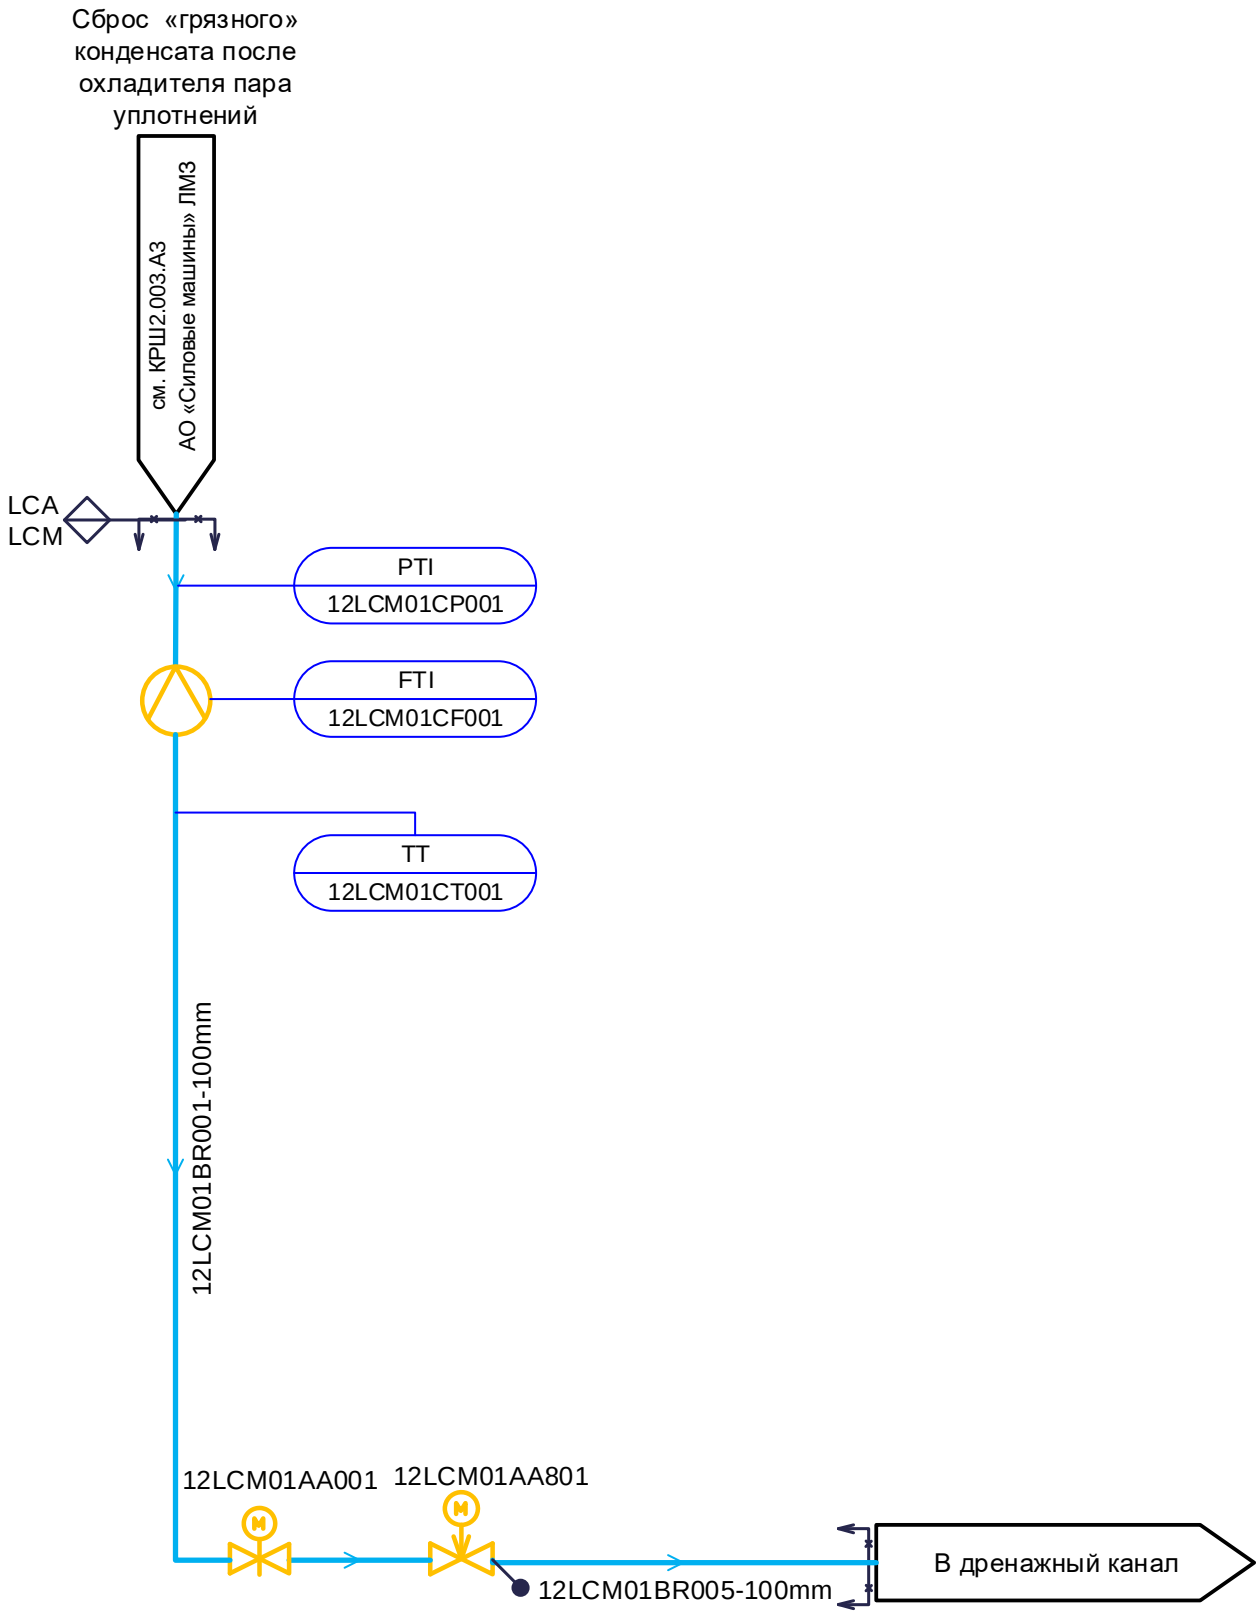

Согласовано

ОАСУ Соболева

Взам. инв. №

Подпись и дата

Инв. № подл.

Изм.	Кол.уч	Лист	№ док.	Подп.	Дата
1	-	Зам	187-21		

181M1D – 10UHJ – 1357 – TD.M

Модернизация генерирующего объекта Киришская ГРЭС (Г-2т)

Разработал	Сиворонова	
Проверил	Супонина	
Н. контр.	Астраханцев	

Главный корпус. PI-диаграмма трубопроводов подачи основного конденсата на вспомогательное оборудование и «грязный сброс».

Стадия	Лист	Листов
Р	3	

PI-диаграмма трубопроводов подачи основного конденсата на "грязный сброс". Система LCM.

АКЦИОНЕРНОЕ ОБЩЕСТВО ИНСТИТУТ ТЕПЛОЭЛЕКТРОПРОЕКТ Г. МОСКВА

Формат А4