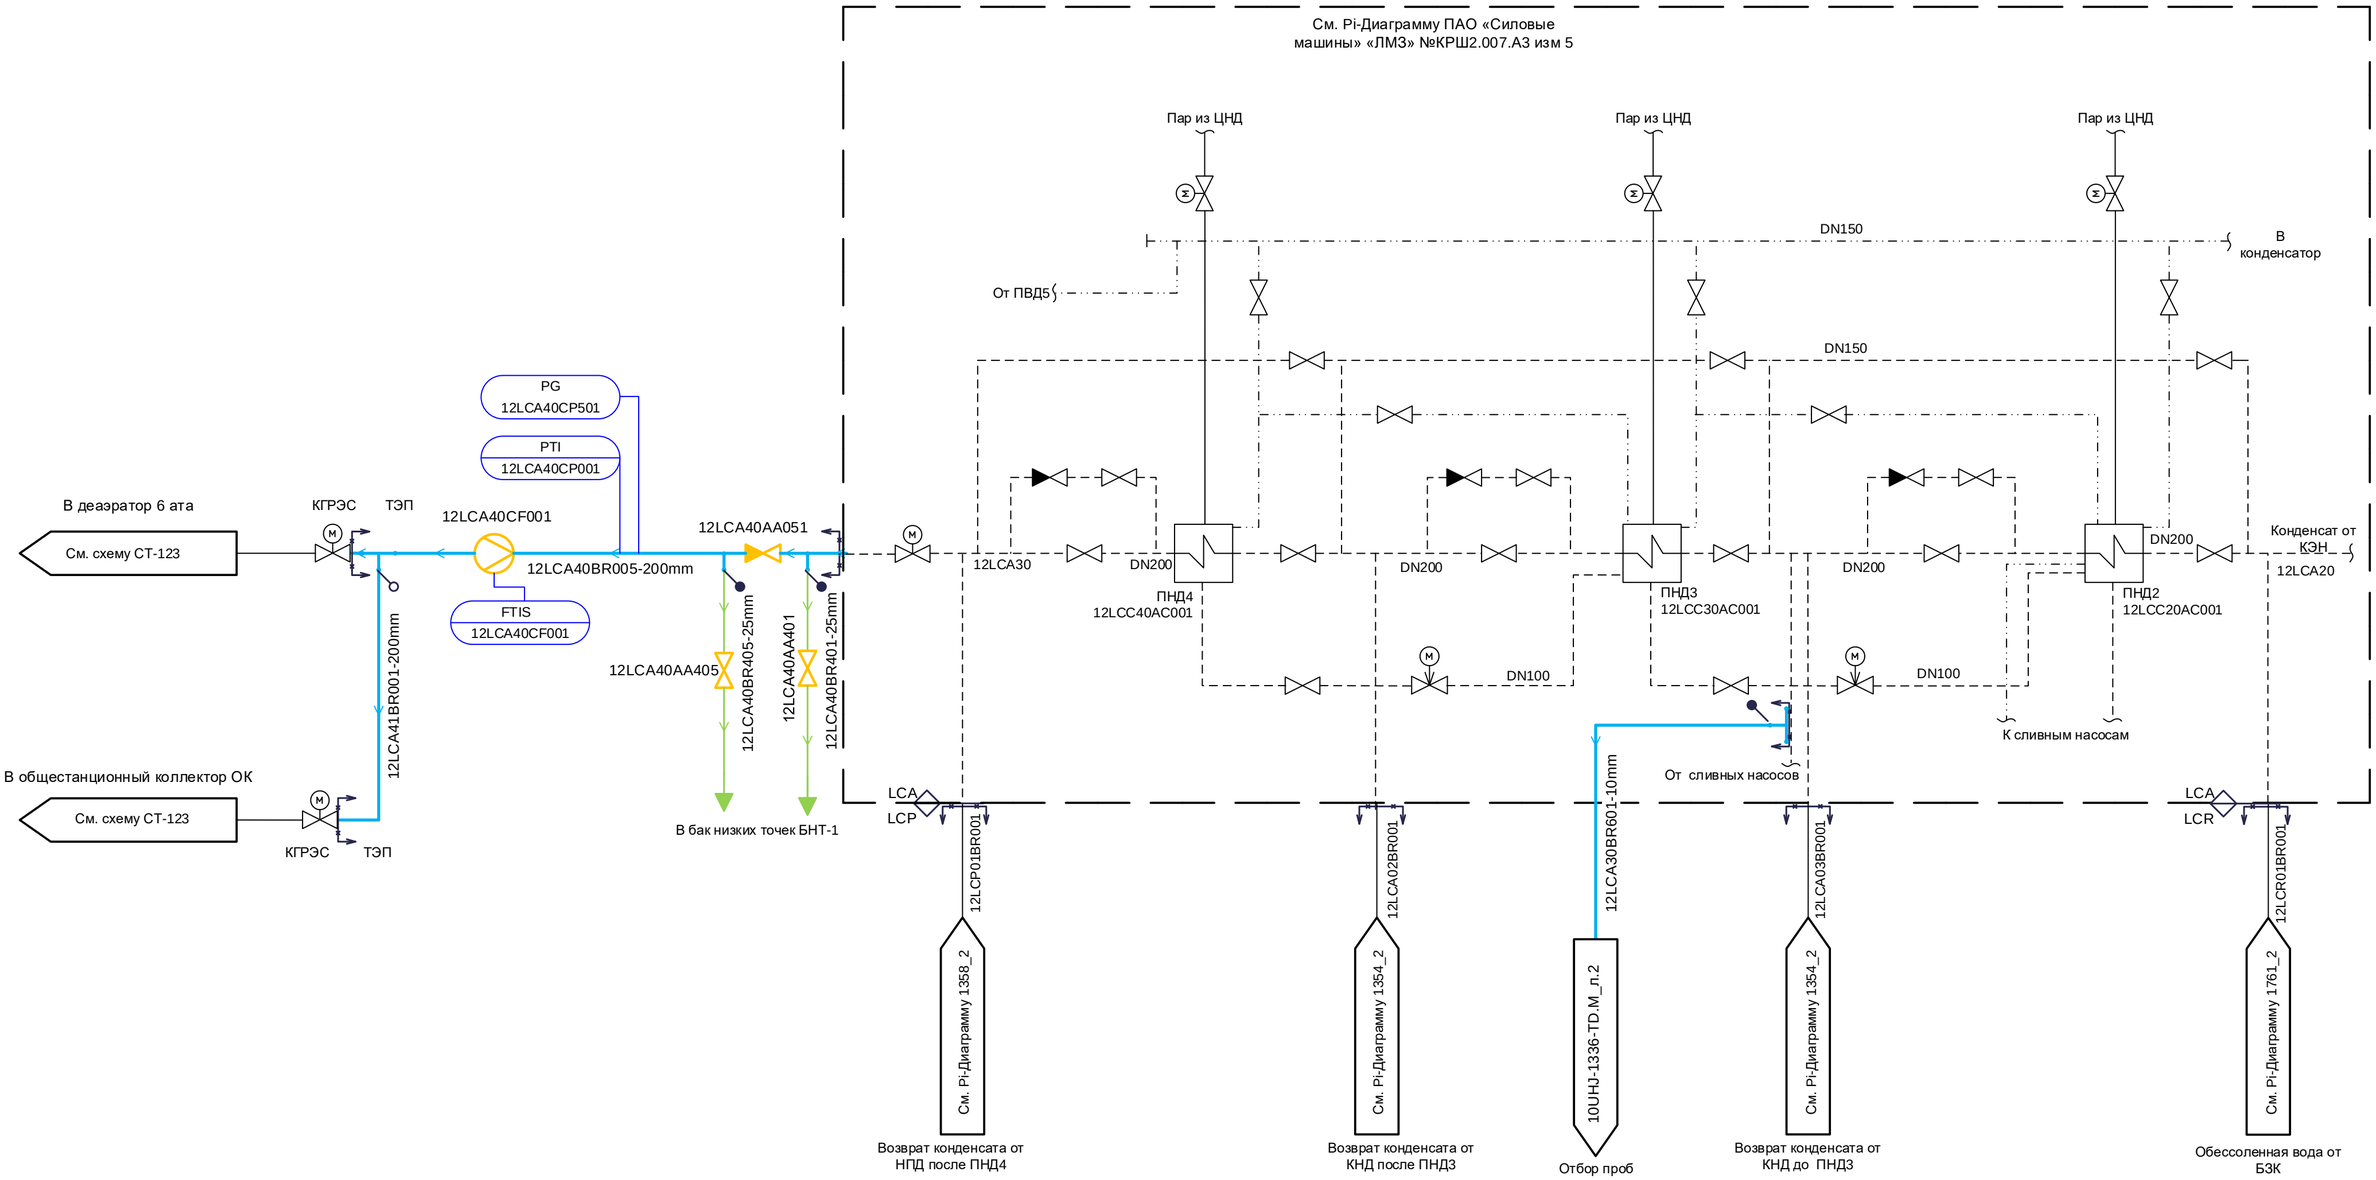

2	-	Зам	450-21			181M1D – 10UHJ – 1357 – TD.M
Изм.	Кол.уч	Лист	№ док.	Подп.	Дата	Модернизация генерирующего объекта Киришская ГРЭС (Г-2т)
Разработал		Сиворонова				Главный корпус. PI-диаграмма трубопроводов подачи основного конденсата на вспомогательное оборудование и «грязный сброс».
Проверил		Супонина				Стадия: Р; Лист: 4; Листов:
Н. контр.		Астраханцев				PI-диаграмма трубопроводов подачи основного конденсата от группы ПНД. Система LCA.

АКЦИОНЕРНОЕ ОБЩЕСТВО ИНСТИТУТ ТЕПЛОЭЛЕКТРОПРОЕКТ Г. МОСКВА

Согласовано
ОАСУ Соболева

Взам. инв. №
Подпись и дата
Инв. № подл.

Формат А2