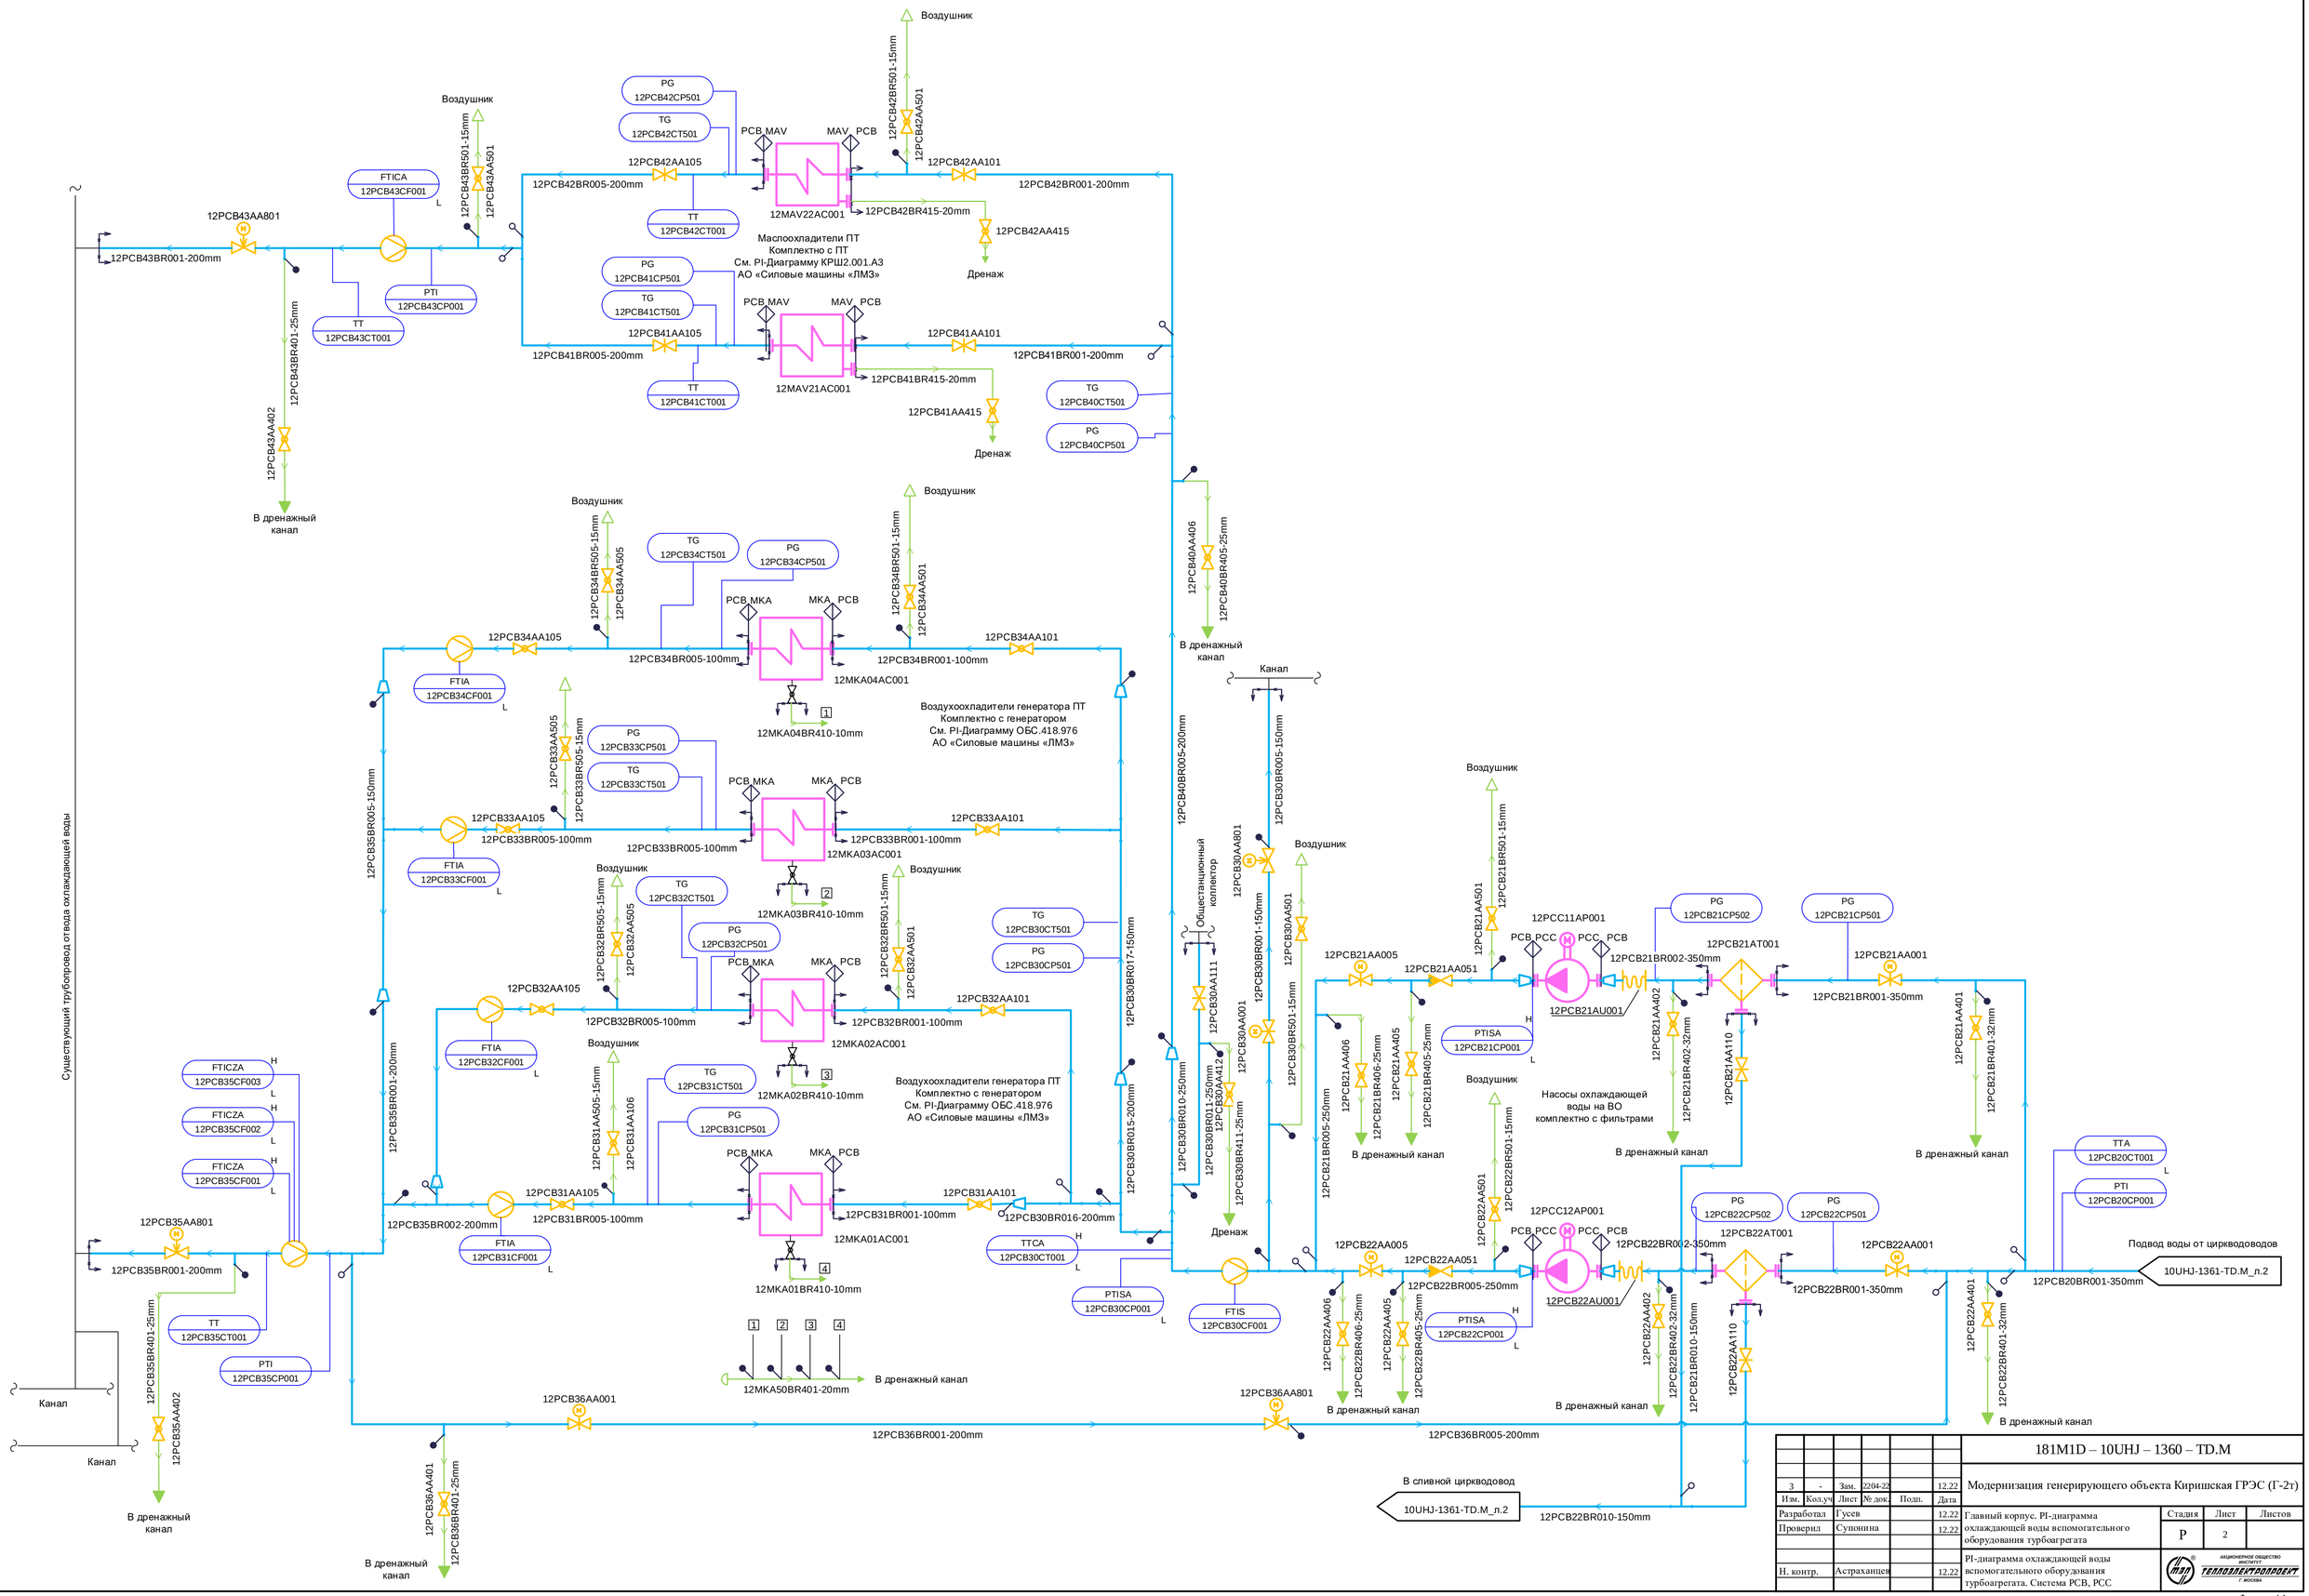

						181M1D – 10UHJ – 1360 – TD.M		
3	-	Зам.	2204-22		12.22	Модернизация генерирующего объекта Киришская ГРЭС (Г-2т)		
Изм.	Кол.уч	Лист	№ док.	Подп.	Дата			
Разработал		Гусев			12.22	Главный корпус. PI-диаграмма охлаждающей воды вспомогательного оборудования турбоагрегата	Стадия	Лист	Листов
Проверил		Супонина			12.22		Р	2	
Н. контр.		Астраханцев			12.22	PI-диаграмма охлаждающей воды вспомогательного оборудования турбоагрегата. Система PCB, PCC	АКЦИОНЕРНОЕ ОБЩЕСТВО ИНСТИТУТ ТЕПЛОЭЛЕКТРОПРОЕКТ Г. МОСКВА	

Согласовано

Взам. инв. № | Подпись и дата | Инв. № подл.

ОАСУ | Соболева

Формат А1