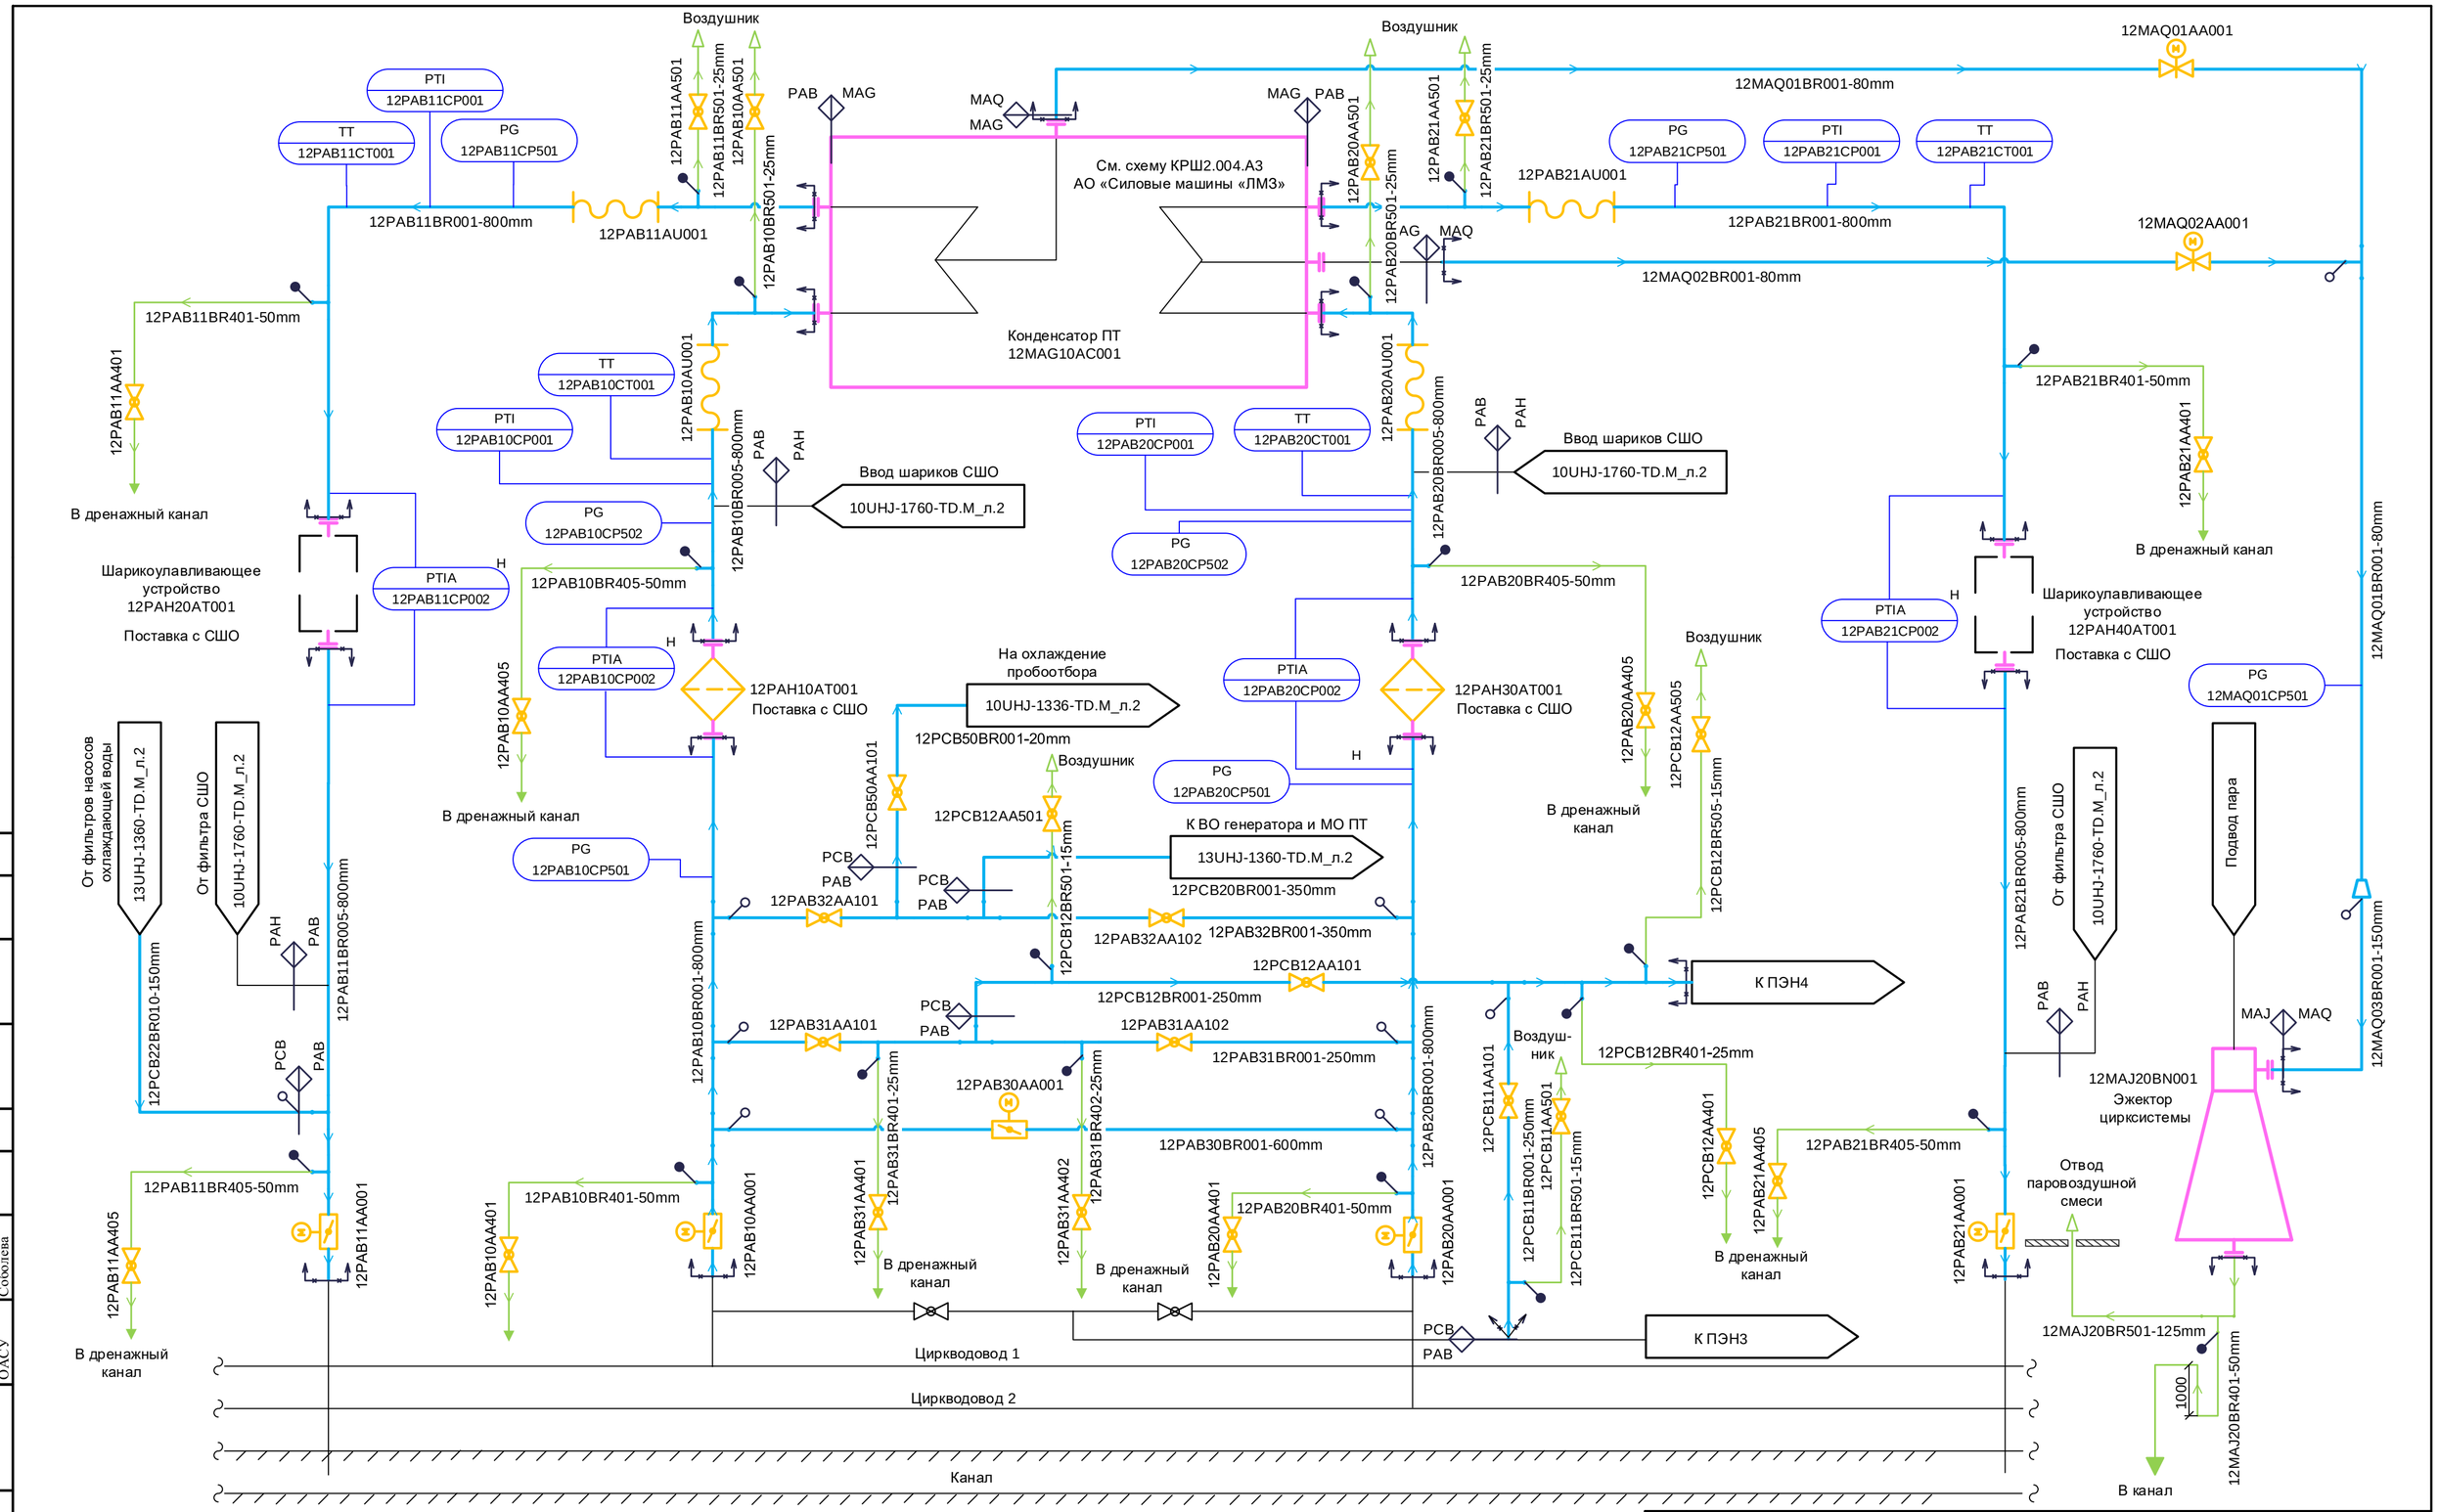

Примечание: Система шариковой очистки конденсатора см. PI-Диаграмму 10UHJ-1760-TD.M

1	-	Зам.	886-21		10.21	
Изм.	Кол.уч	Лист	№ док.	Подп.	Дата	
Разработал		Дёмина				
Проверил		Супонина				
Н. контр.		Астраханцев				

181M1D – 10UHJ – 1361 – TD.M

Модернизация генерирующего объекта Киришская ГРЭС (Г-2т)

Главный корпус. PI-диаграмма трубопроводов охлаждающей воды конденсатора турбоагрегата

PI-диаграмма трубопроводов охлаждающей воды конденсатора турбоагрегата. Система PAB

Стадия	Лист	Листов
Р	2	

АКЦИОНЕРНОЕ ОБЩЕСТВО ИНСТИТУТ ТЕПЛОЭЛЕКТРОПРОЕКТ Г. МОСКВА

Согласовано

ОАСУ Соболева

Взам. инв. №

Подпись и дата

Инв. № подл.

Формат А2