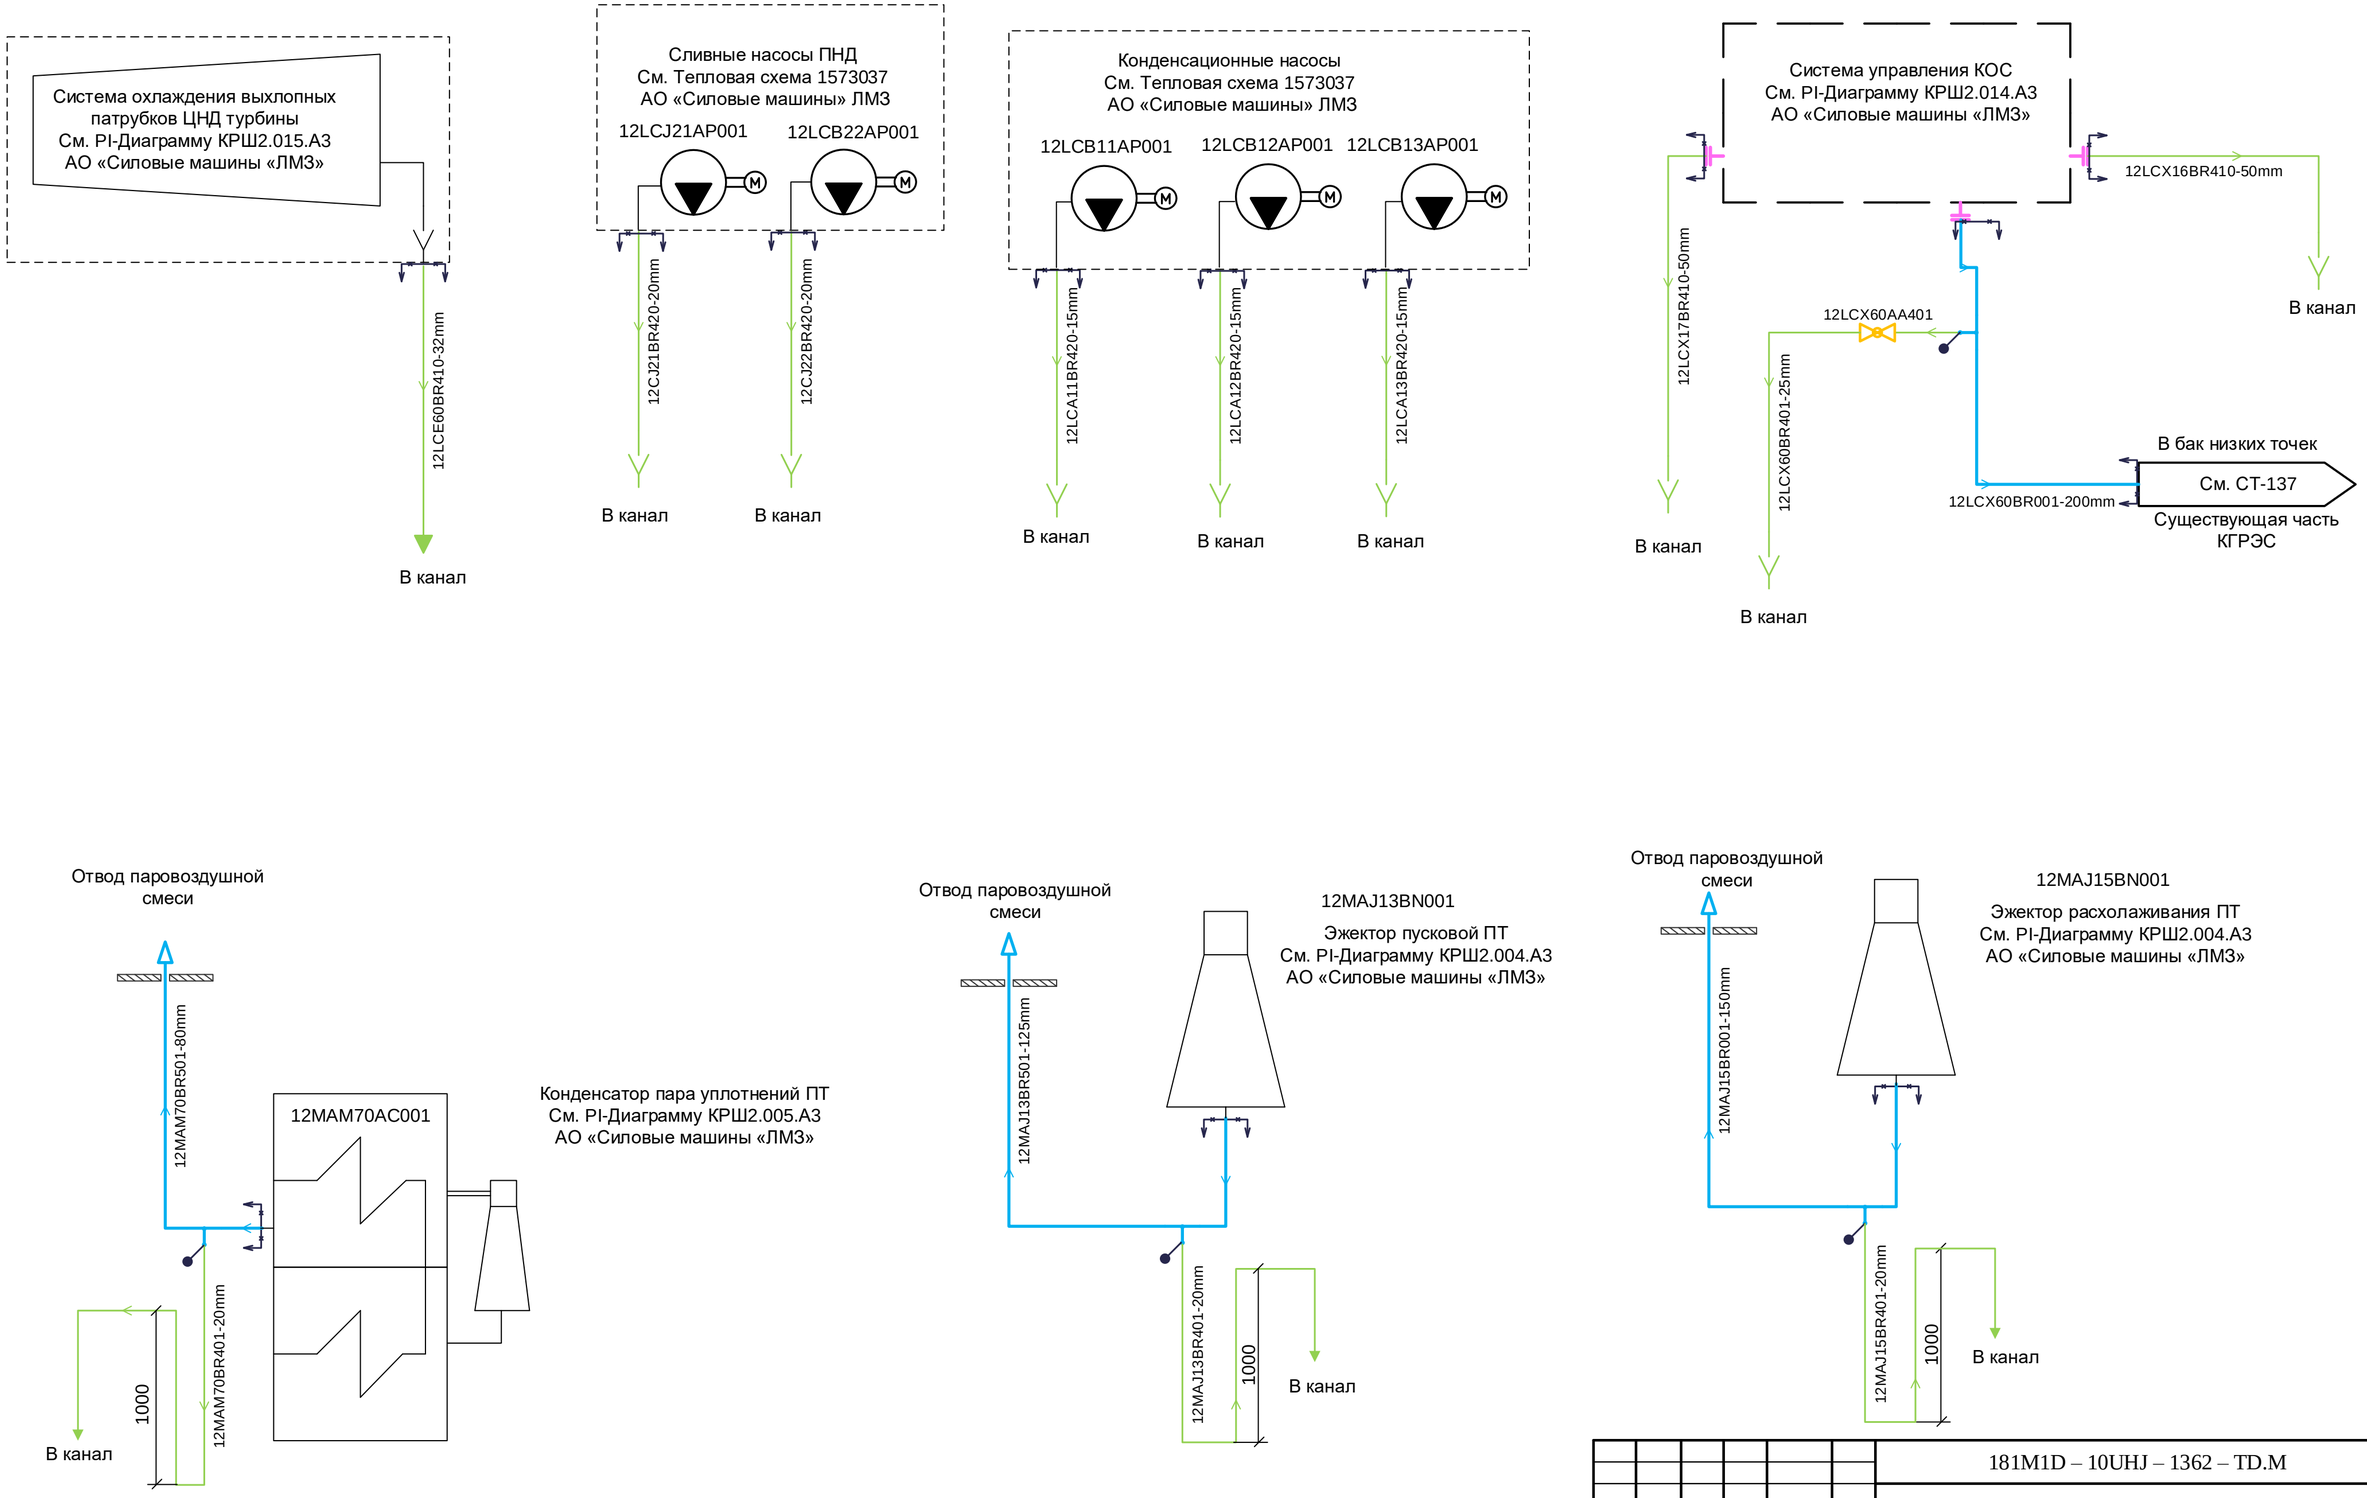

1	-	Зам.	886-21		10.21	181M1D – 10UHJ – 1362 – TD.M
Изм.	Кол.уч	Лист	№ док.	Подп.	Дата	Модернизация генерирующего объекта Киришская ГРЭС (Г-2т)
Разработал		Дёмина				Главный корпус. PI-диаграмма дренажей, воздушников и вспомогательных трубопроводов турбоагрегата
Проверил		Супонина				Стадия: Р; Лист: 2; Листов:
Н. контр.		Астраханцев				PI-диаграмма дренажей, воздушников и вспомогательных трубопроводов турбоагрегата

АКЦИОНЕРНОЕ ОБЩЕСТВО ИНСТИТУТ ТЕПЛОЭЛЕКТРОПРОЕКТ Г. МОСКВА

Согласовано

Взам. инв. №

Подпись и дата

Инв. № подл.

Формат А2