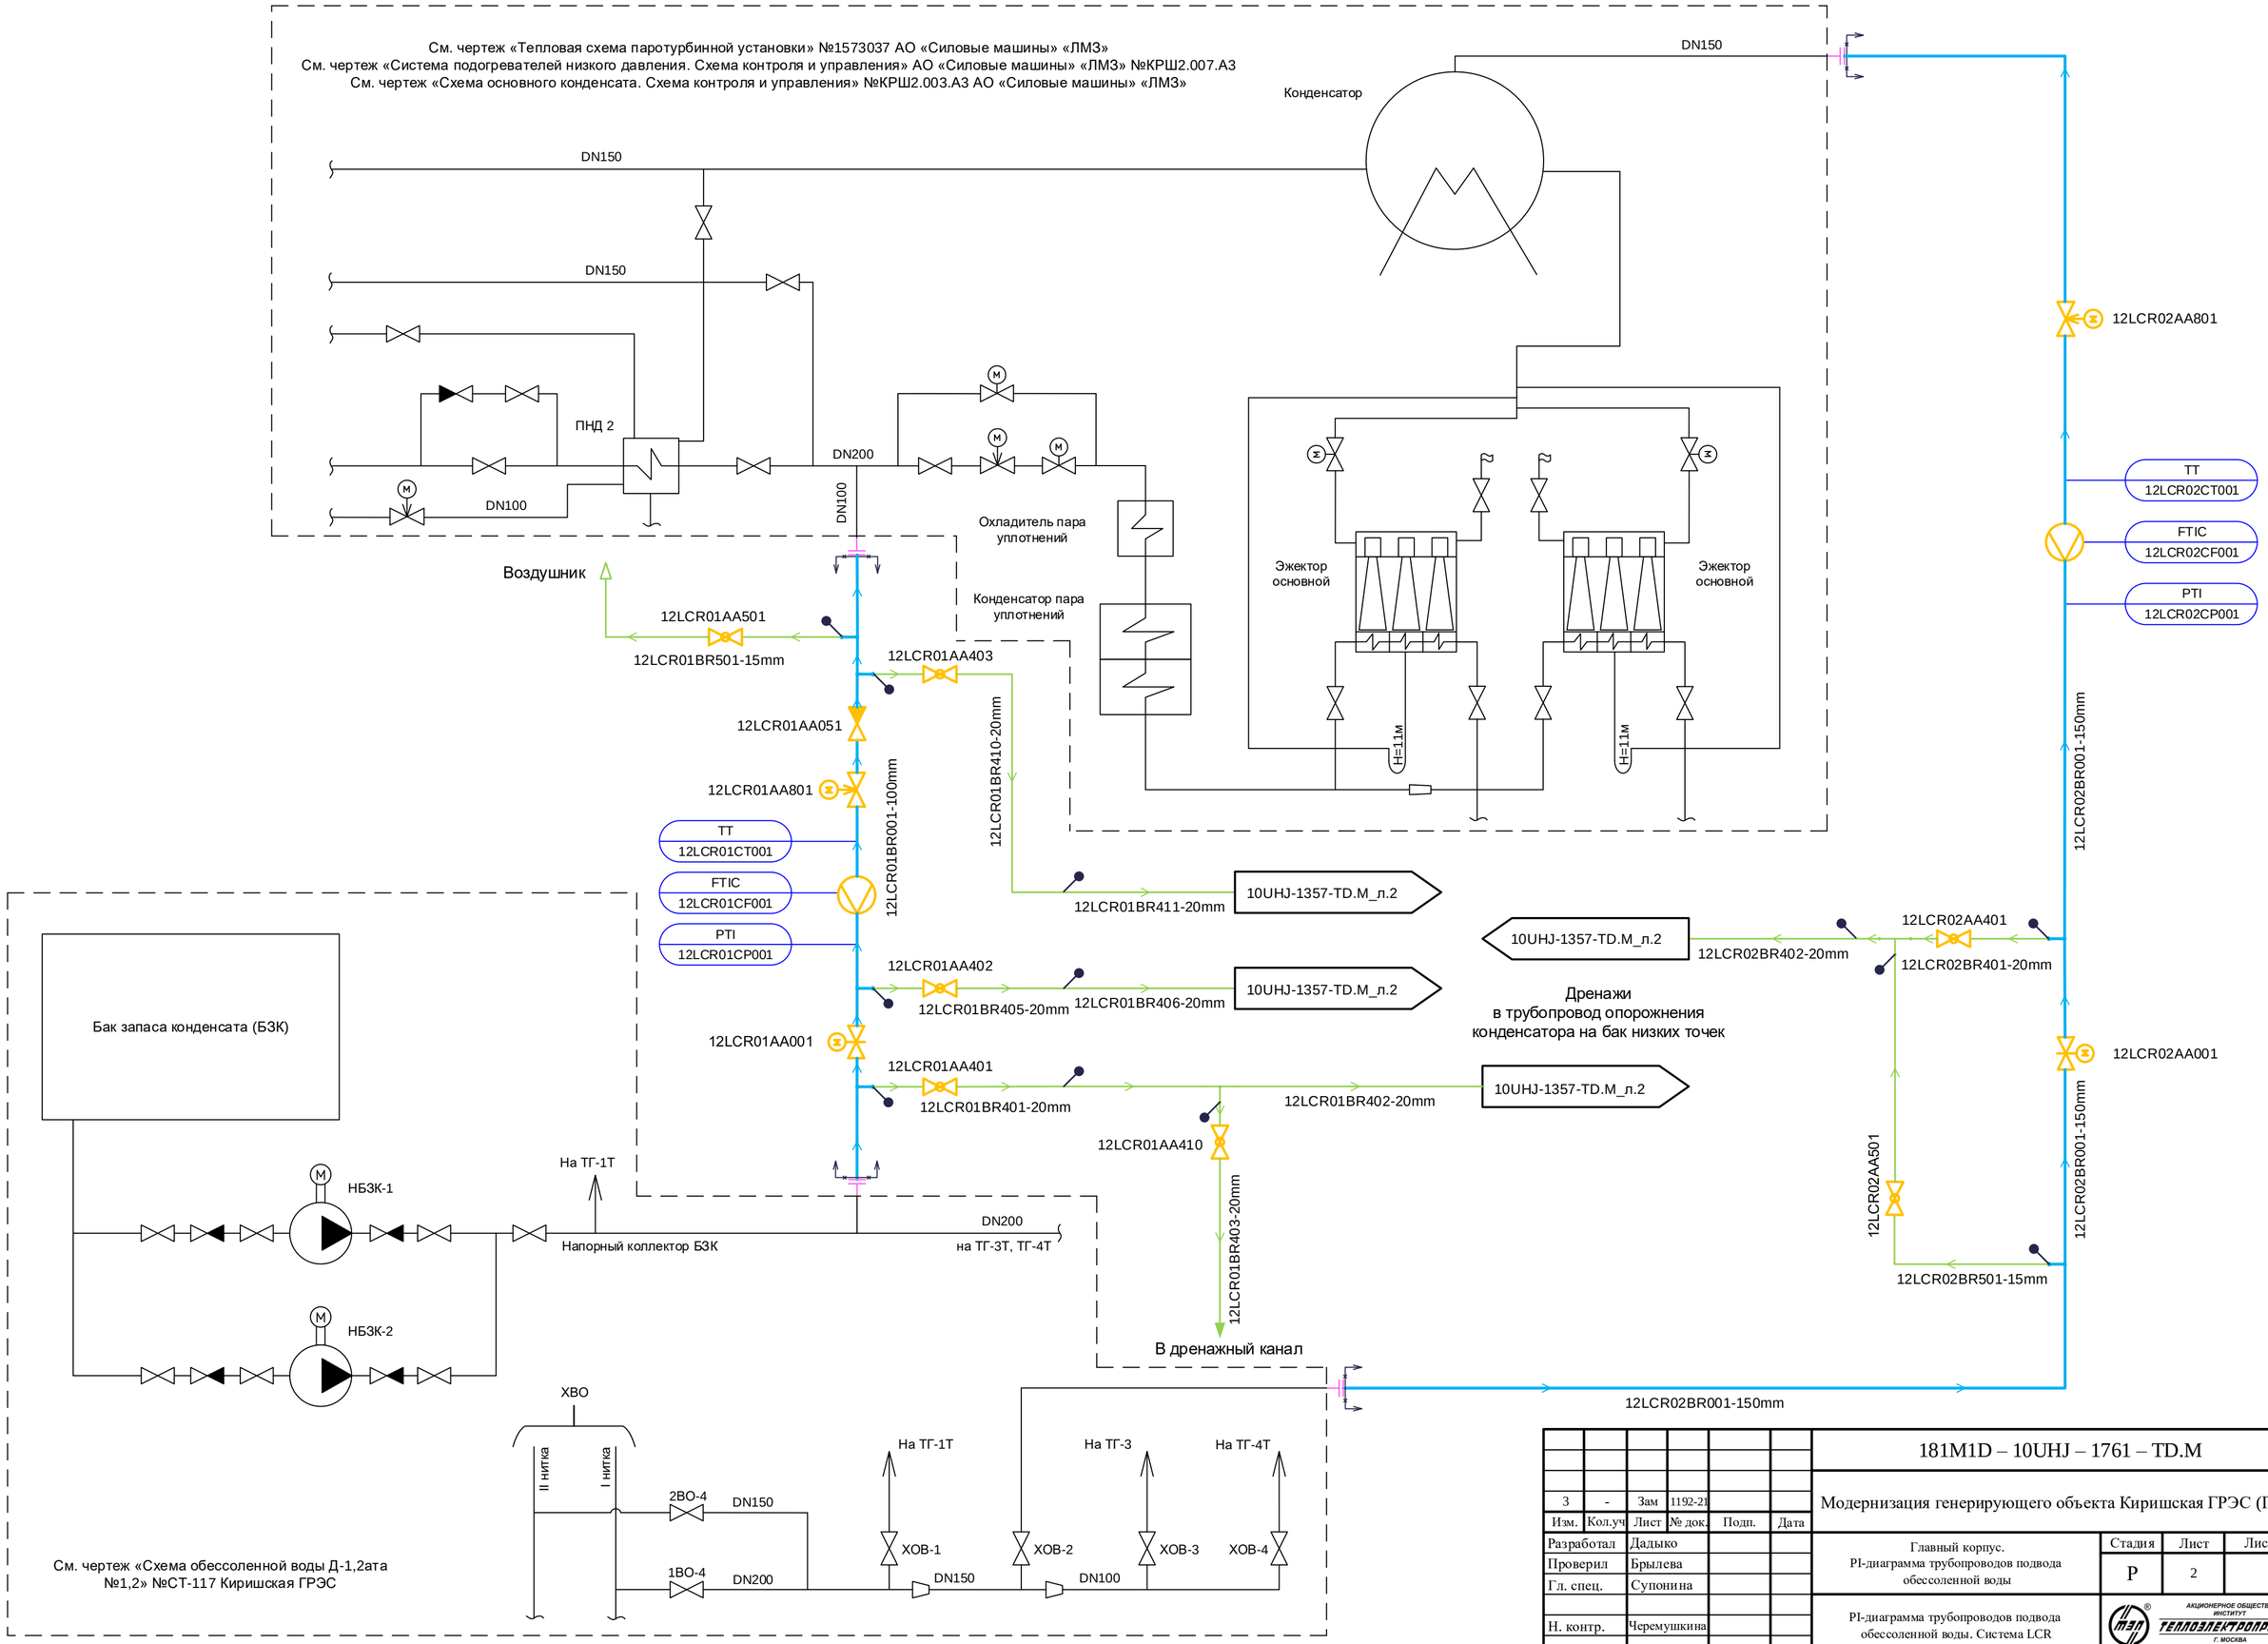

3	-	Зам	1192-21			
Изм.	Кол.уч	Лист	№ док.	Подп.	Дата	
Разработал		Дадыко				
Проверил		Брылева				
Гл. спец.		Супонина				
Н. контр.		Черемушкина				

181M1D – 10UHJ – 1761 – TD.M

Модернизация генерирующего объекта Киришская ГРЭС (Г-2т)

Главный корпус.
PI-диаграмма трубопроводов подвода обессоленной воды

Стадия	Лист	Листов
Р	2	

PI-диаграмма трубопроводов подвода обессоленной воды. Система LCR

АКЦИОНЕРНОЕ ОБЩЕСТВО ИНСТИТУТ ТЕПЛОЭЛЕКТРОПРОЕКТ Г. МОСКВА

Согласовано
ОАСУ Соболева

Взам. инв. №

Подпись и дата

Инв. № подл.

Формат А2