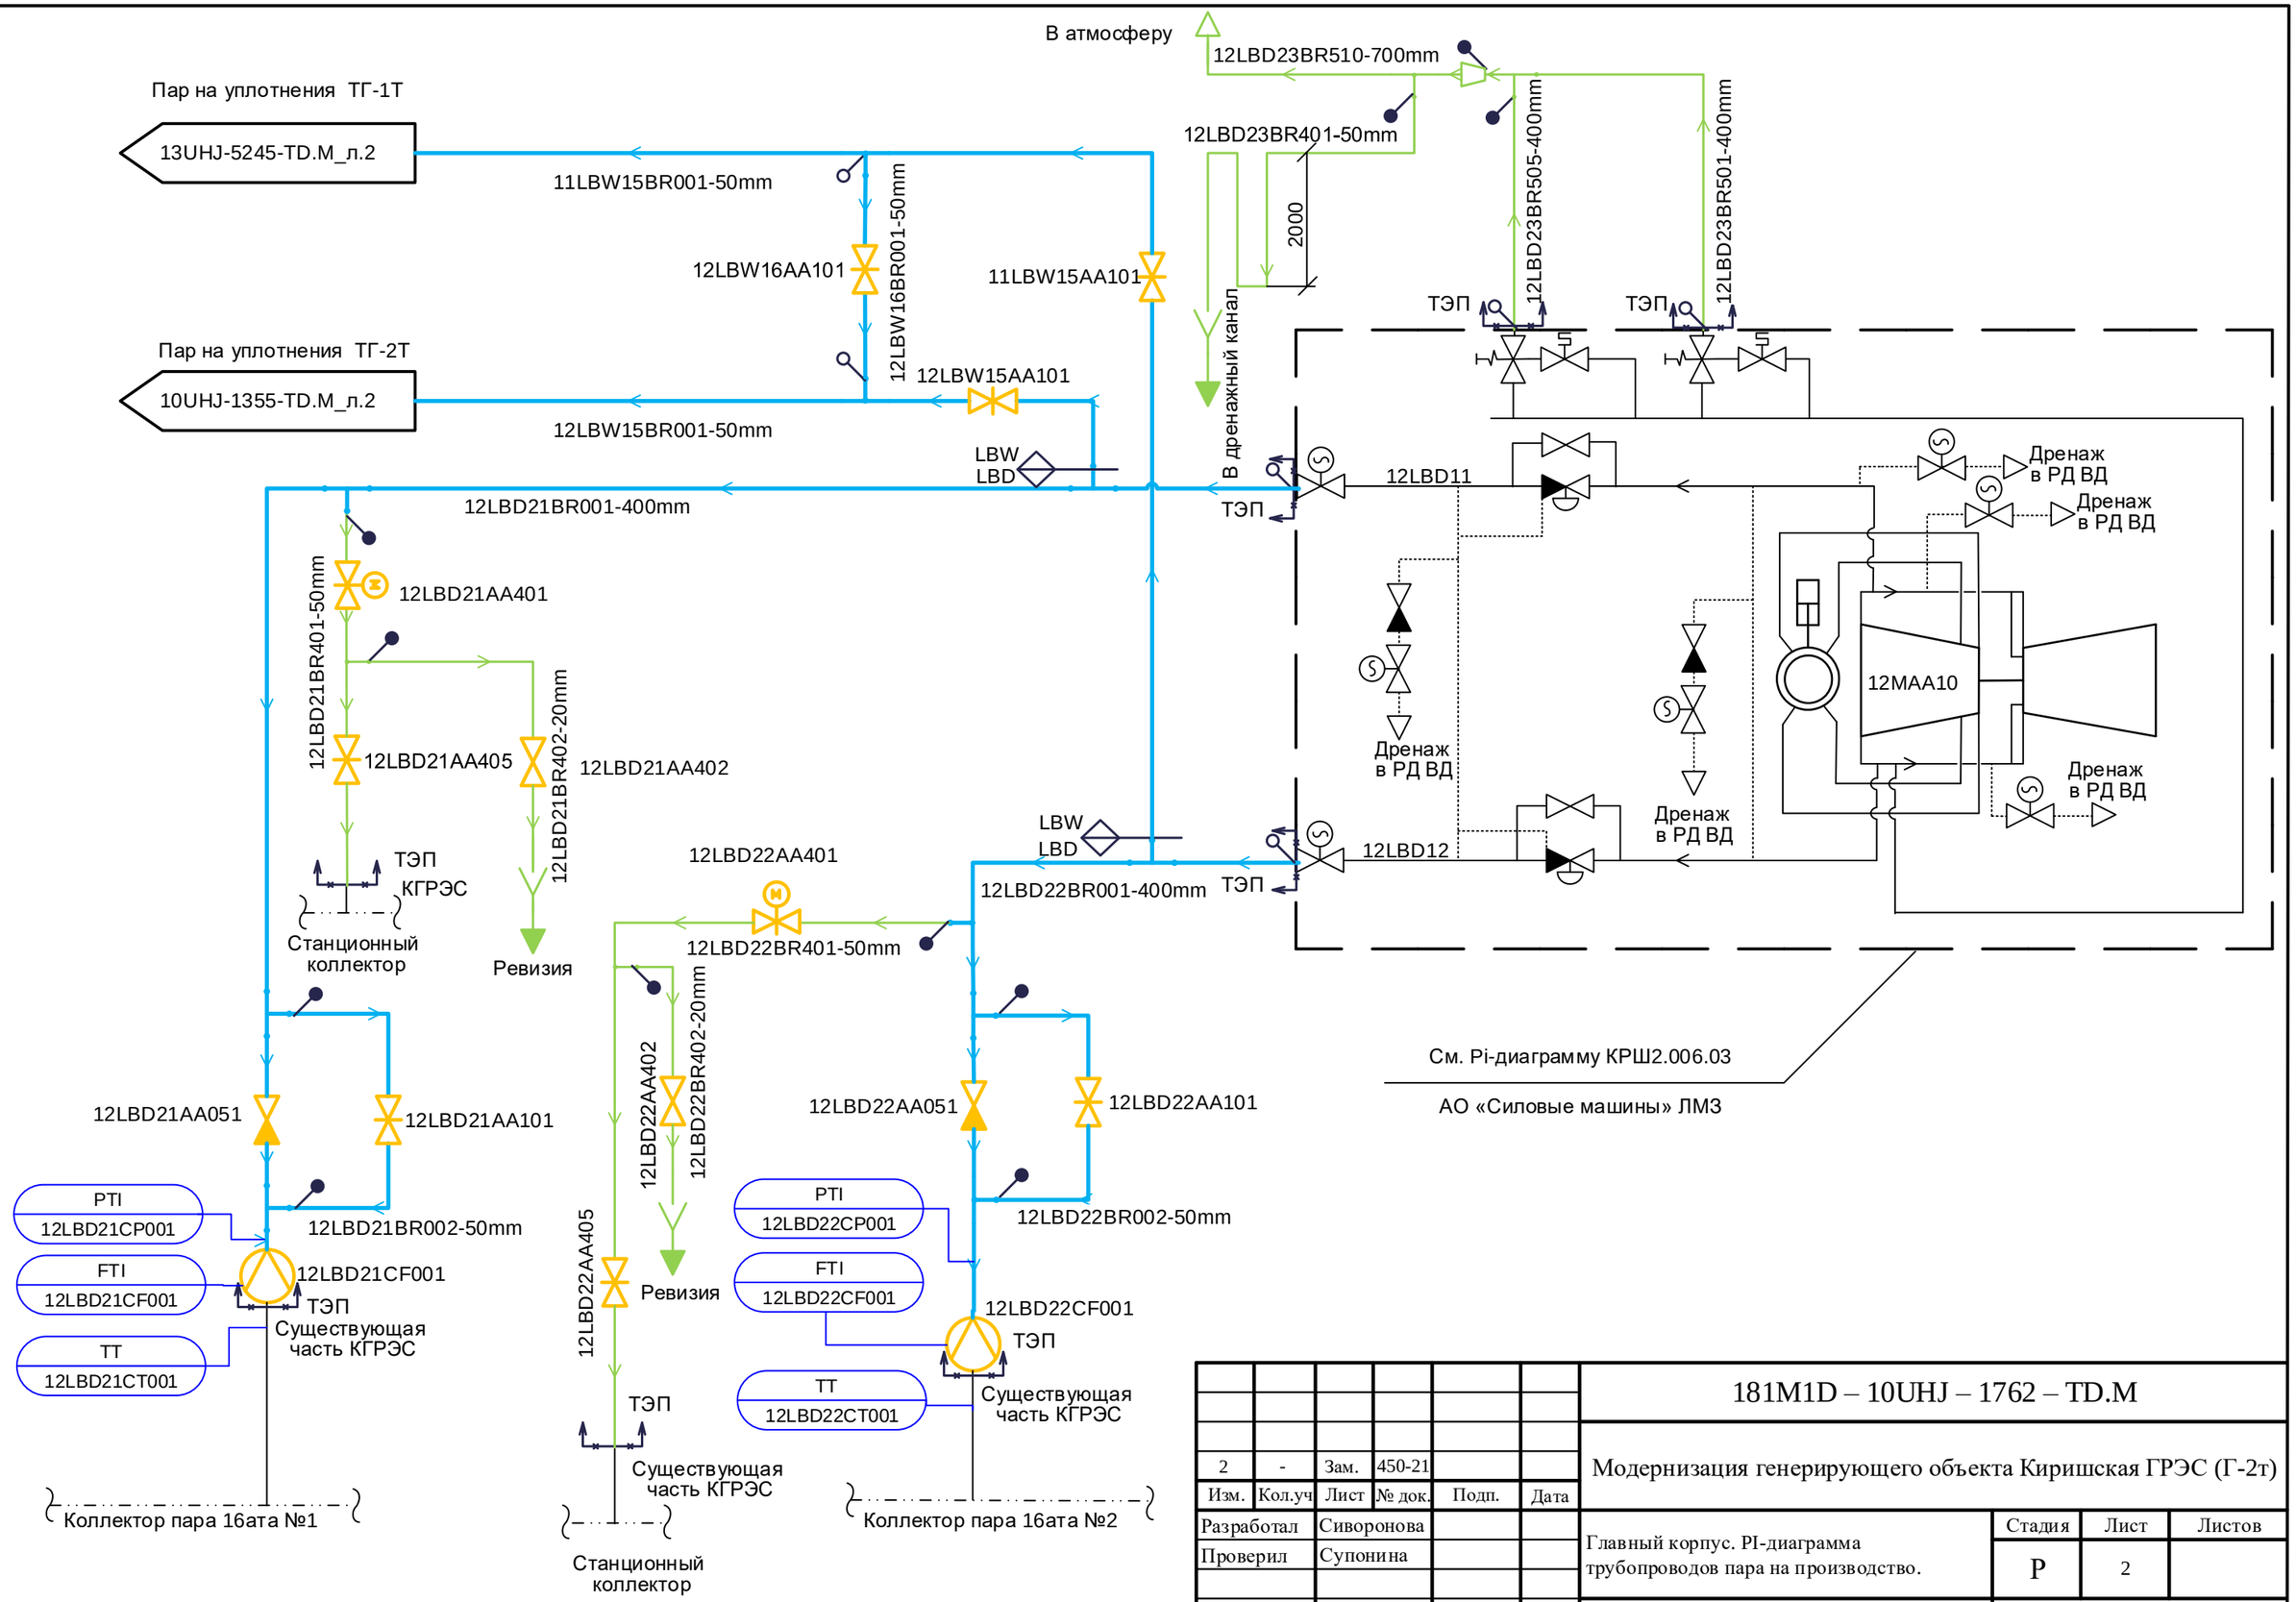

2	-	Зам.	450-21			
Изм.	Кол.уч	Лист	№ док.	Подп.	Дата	
Разработал		Сиворонова				
Проверил		Супонина				
Н. контр.		Астраханцев				

181M1D – 10UHJ – 1762 – TD.M

Модернизация генерирующего объекта Киришская ГРЭС (Г-2т)

Главный корпус. PI-диаграмма трубопроводов пара на производство.

Стадия	Лист	Листов
Р	2	

PI-диаграмма трубопроводов отборов пара на производство. Система LBD, LBW.

АКЦИОНЕРНОЕ ОБЩЕСТВО ИНСТИТУТ ТЕПЛОЭЛЕКТРОПРОЕКТ Г. МОСКВА

Согласовано

Соболева

ОАСУ

Взам. инв. №

Подпись и дата

Инв. № подл.

Формат А3