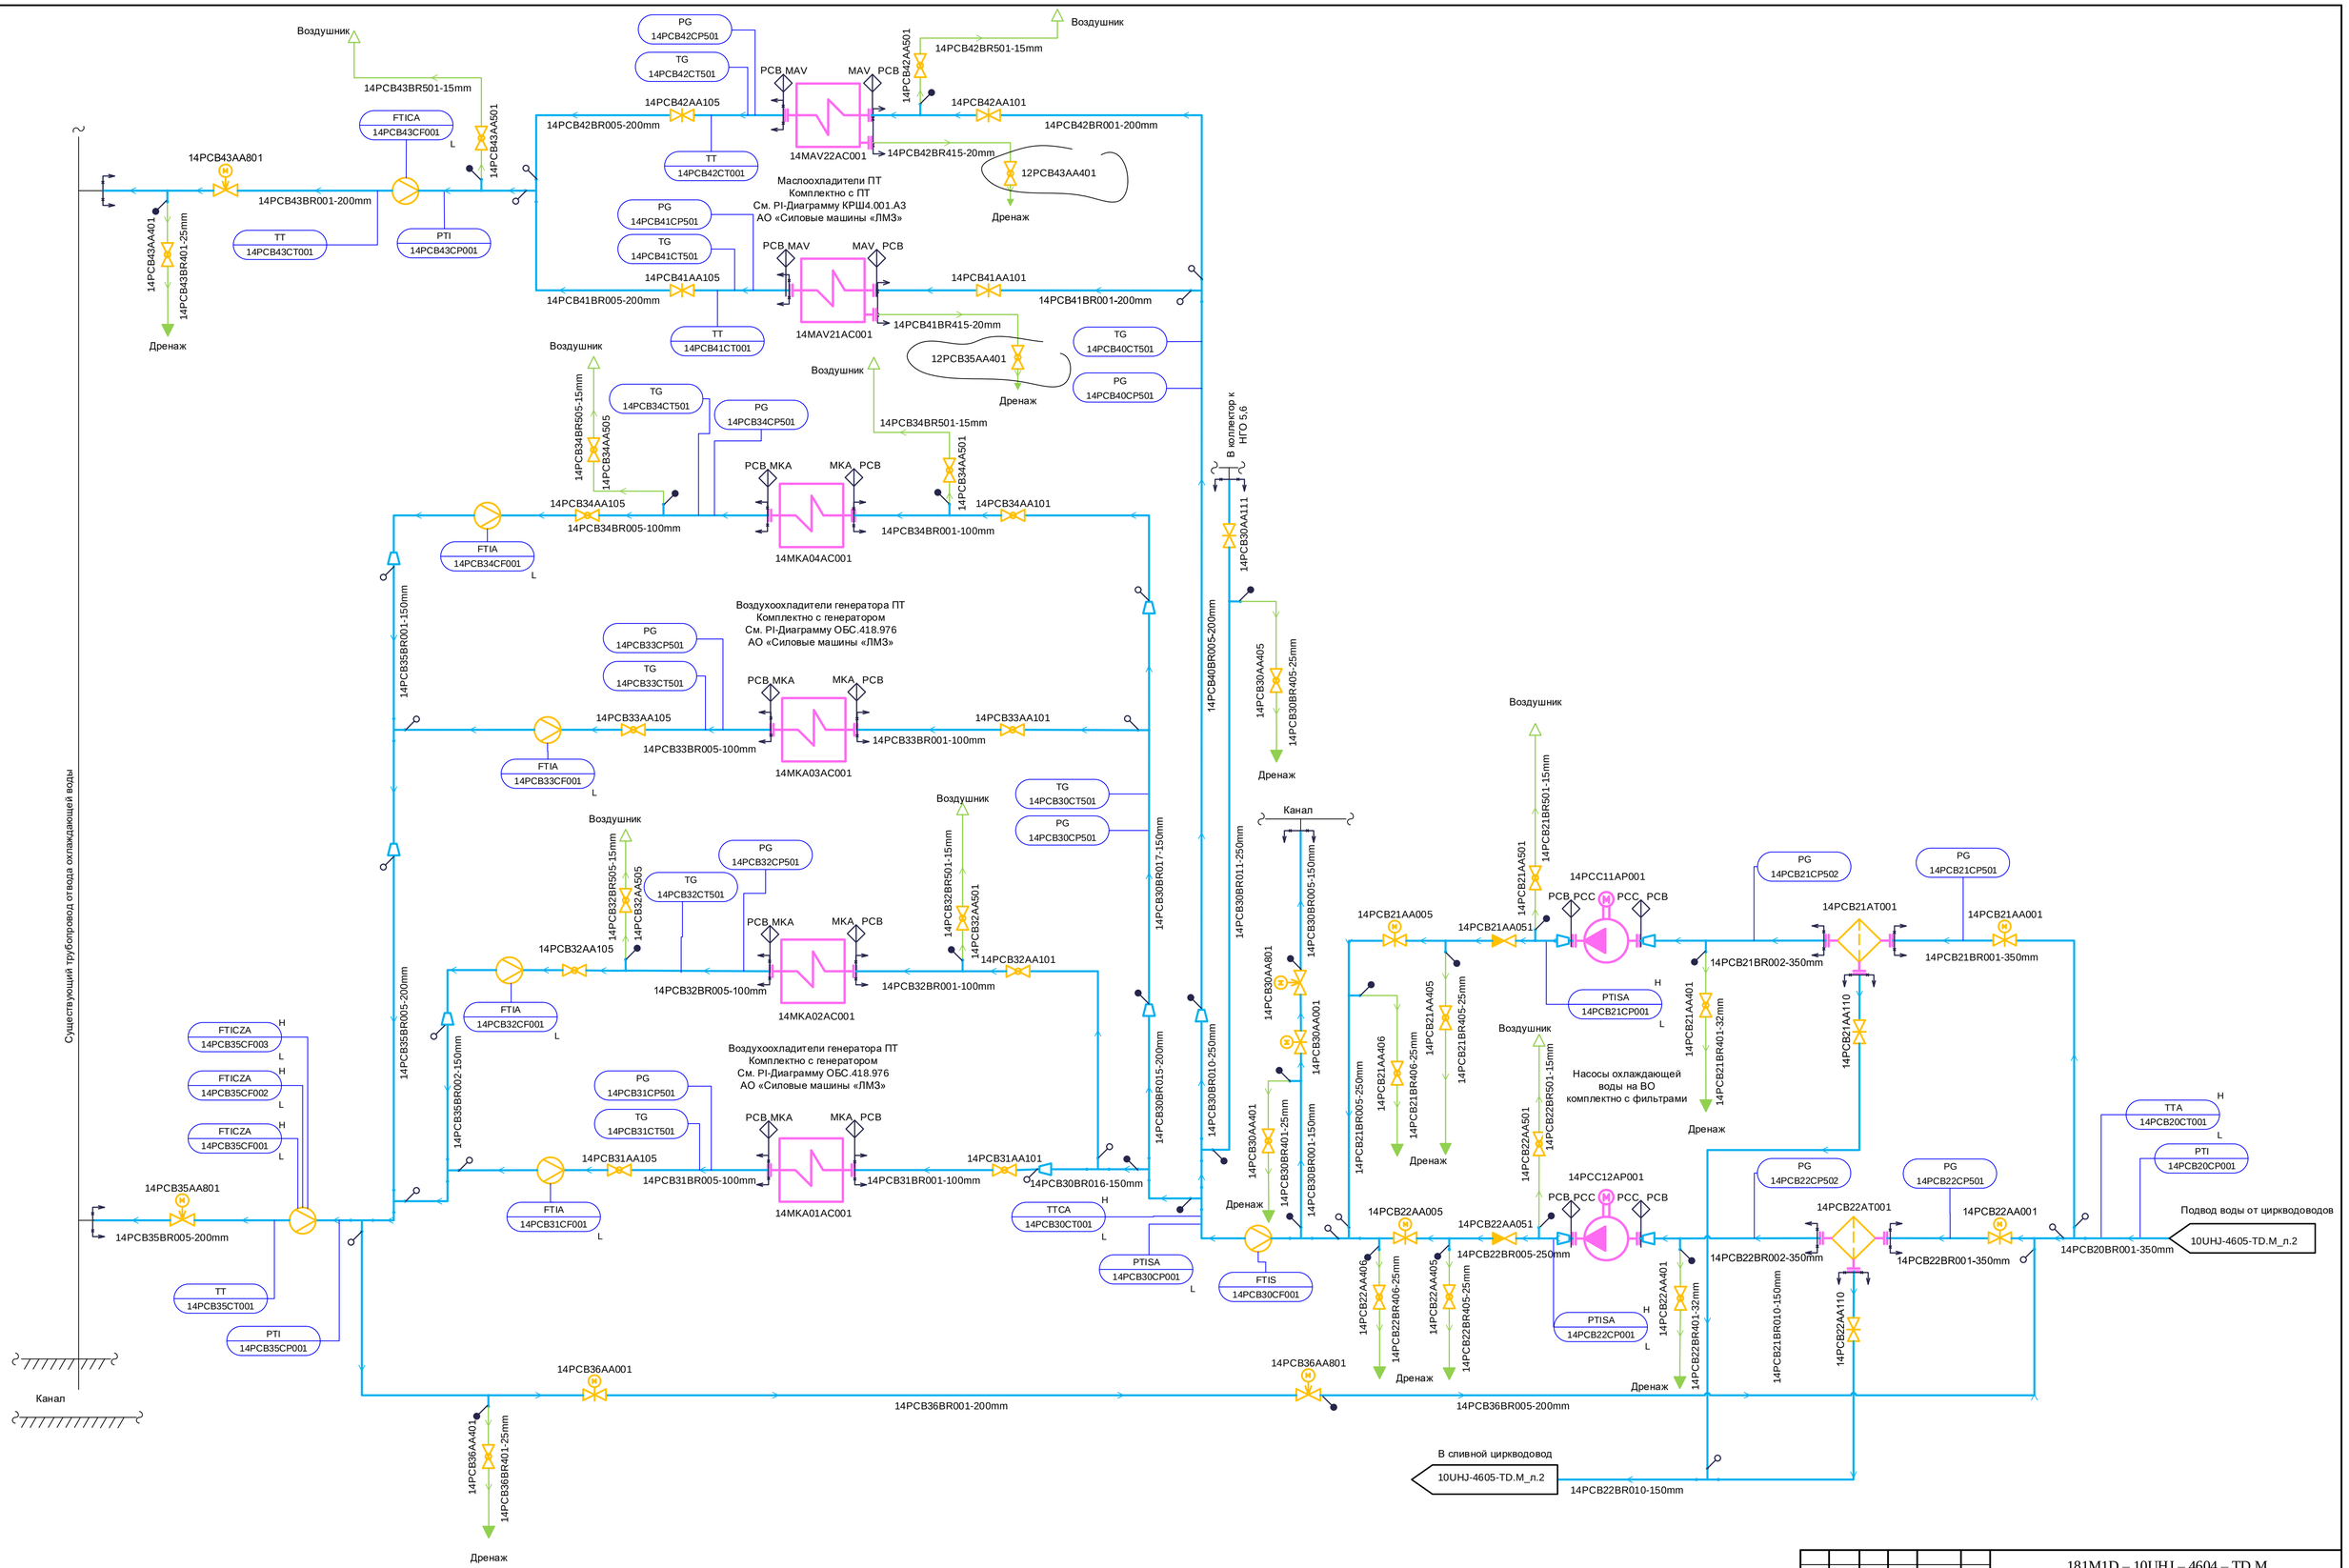

Изм.	Кол.уч	Лист	№ док.	Подп.	Дата	181M1D – 10UHJ – 4604 – TD.M
						Модернизация генерирующего объекта Киришская ГРЭС (Г-4т)
Разработал		Дёмина				Главный корпус. PI-диаграмма охлаждающей воды вспомогательного оборудования турбоагрегата
Проверил		Супонина				Стадия: Р · Лист: 2 · Листов:
Н. контр.		Астраханцев				PI-диаграмма охлаждающей воды вспомогательного оборудования турбоагрегата. Система PCB, PCC

АКЦИОНЕРНОЕ ОБЩЕСТВО «ИНСТИТУТ ТЕПЛОЭЛЕКТРОПРОЕКТ» Г. МОСКВА

Согласовано: ОАСУ Соболева

Взам. инв. № · Подпись и дата · Инв. № подл.

Формат А1