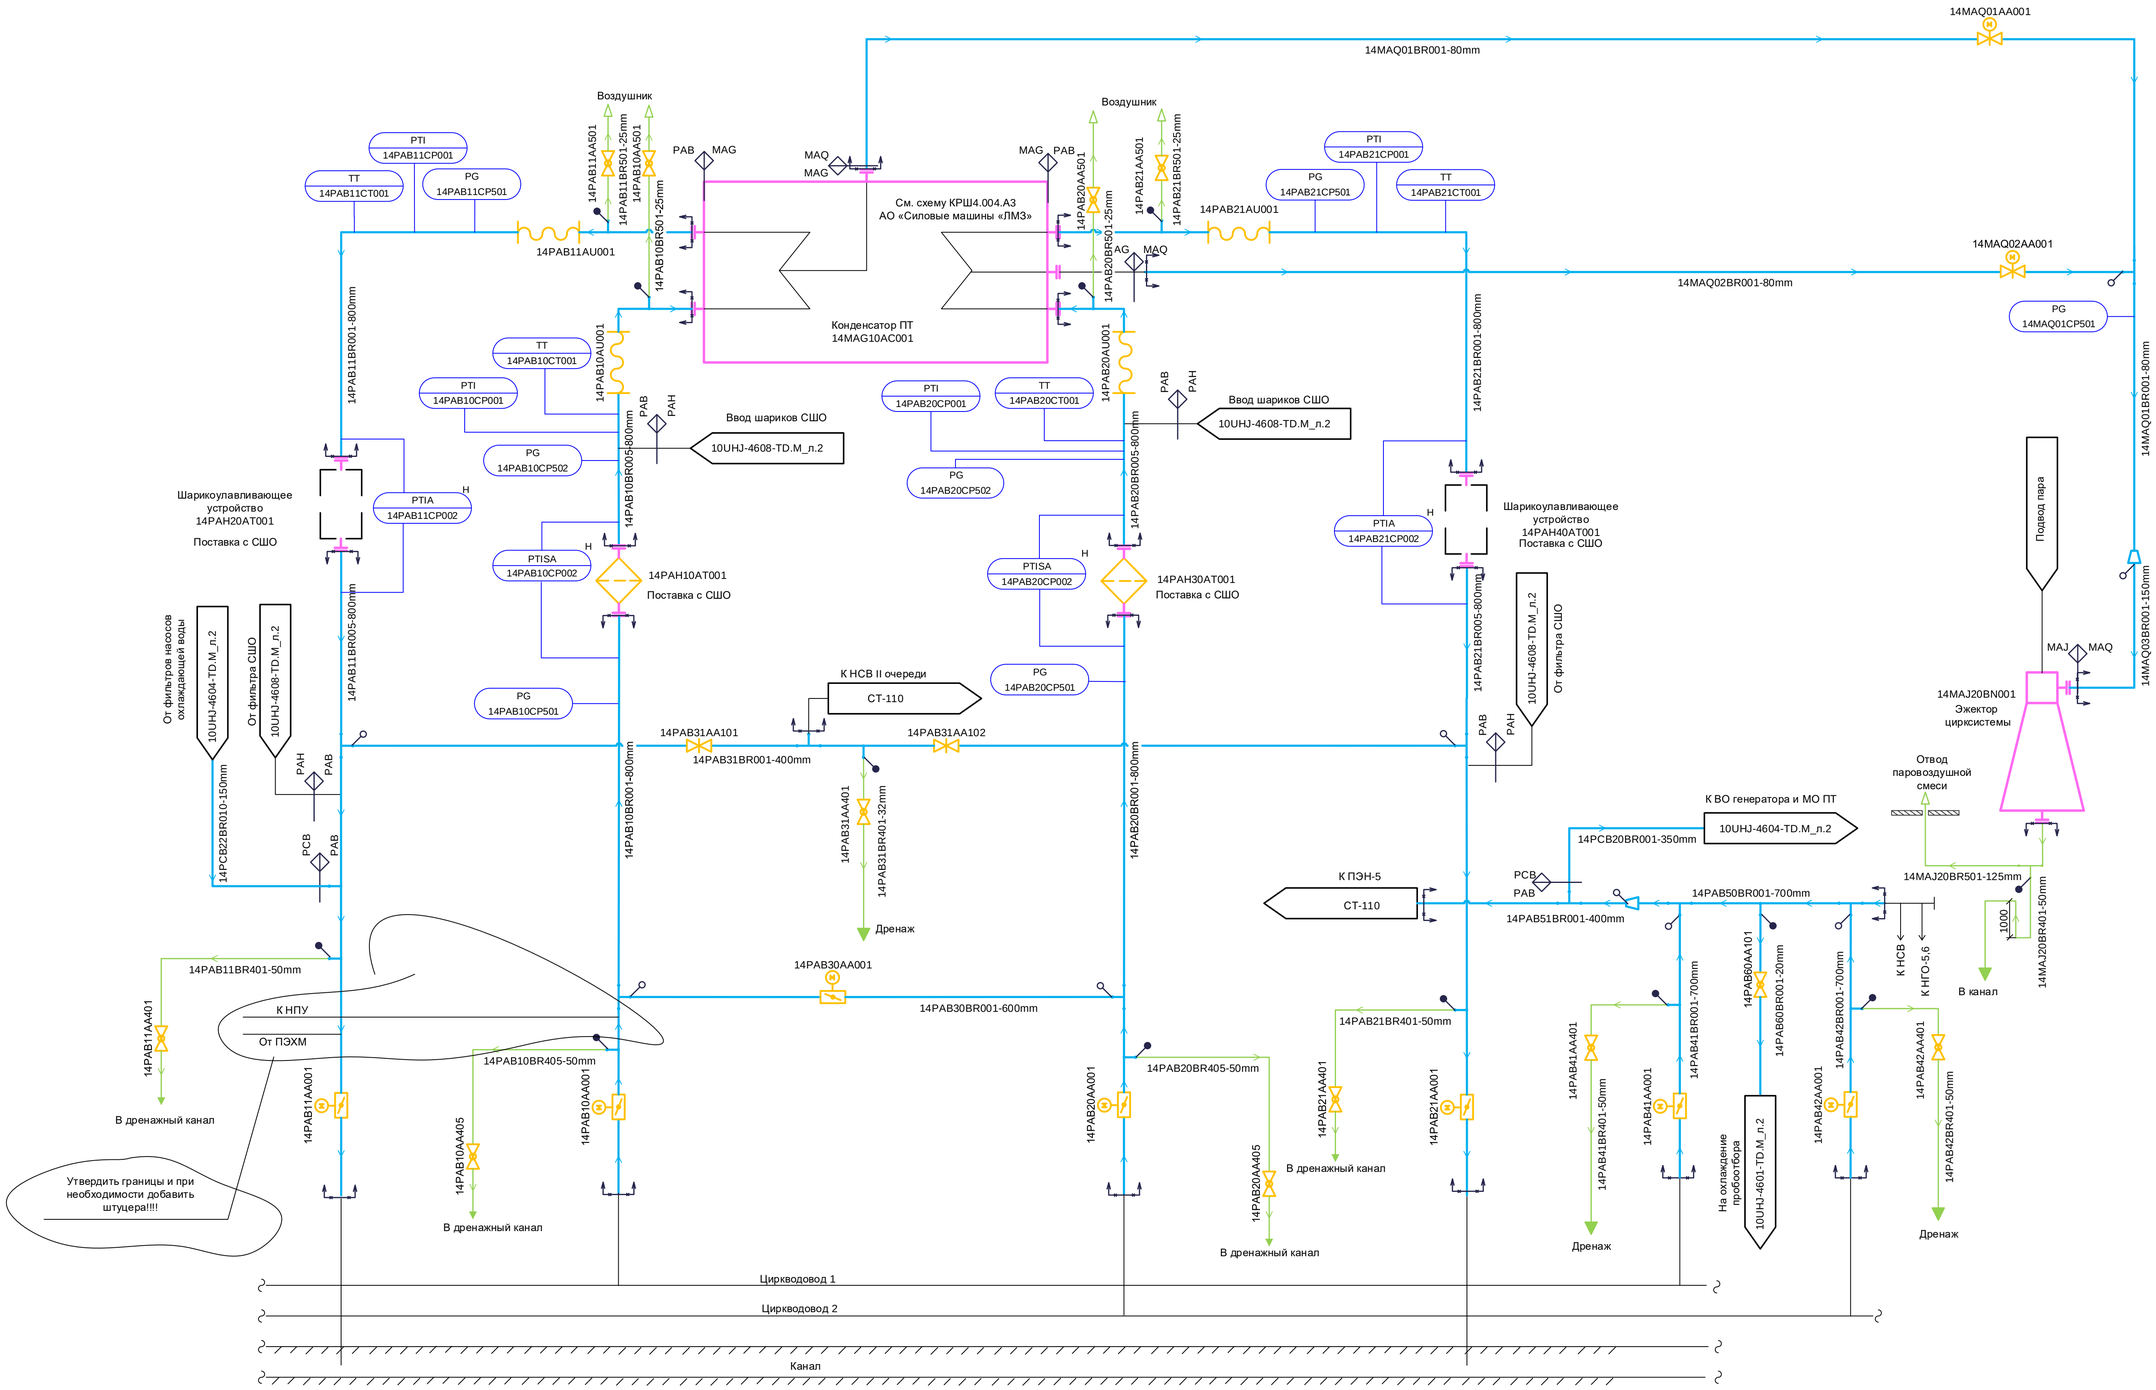

Изм.	Кол.уч	Лист	№ док.	Подп.	Дата	181M1D – 10UHJ – 4605 – TD.M
						Модернизация генерирующего объекта Киришская ГРЭС (Г-4т)
Разработал		Дёмина				Главный корпус. PI-диаграмма трубопроводов охлаждающей воды конденсатора турбоагрегата
Проверил		Супонина				Стадия: Р; Лист: 2; Листов:
Н. контр.		Астраханцев				PI-диаграмма трубопроводов охлаждающей воды конденсатора турбоагрегата. Система PAB

АКЦИОНЕРНОЕ ОБЩЕСТВО ИНСТИТУТ ТЕПЛОЭЛЕКТРОПРОЕКТ г. МОСКВА

Согласовано

ОАСУ Соболева

Взам. инв. №

Подпись и дата

Инв. № подл.

Формат А1