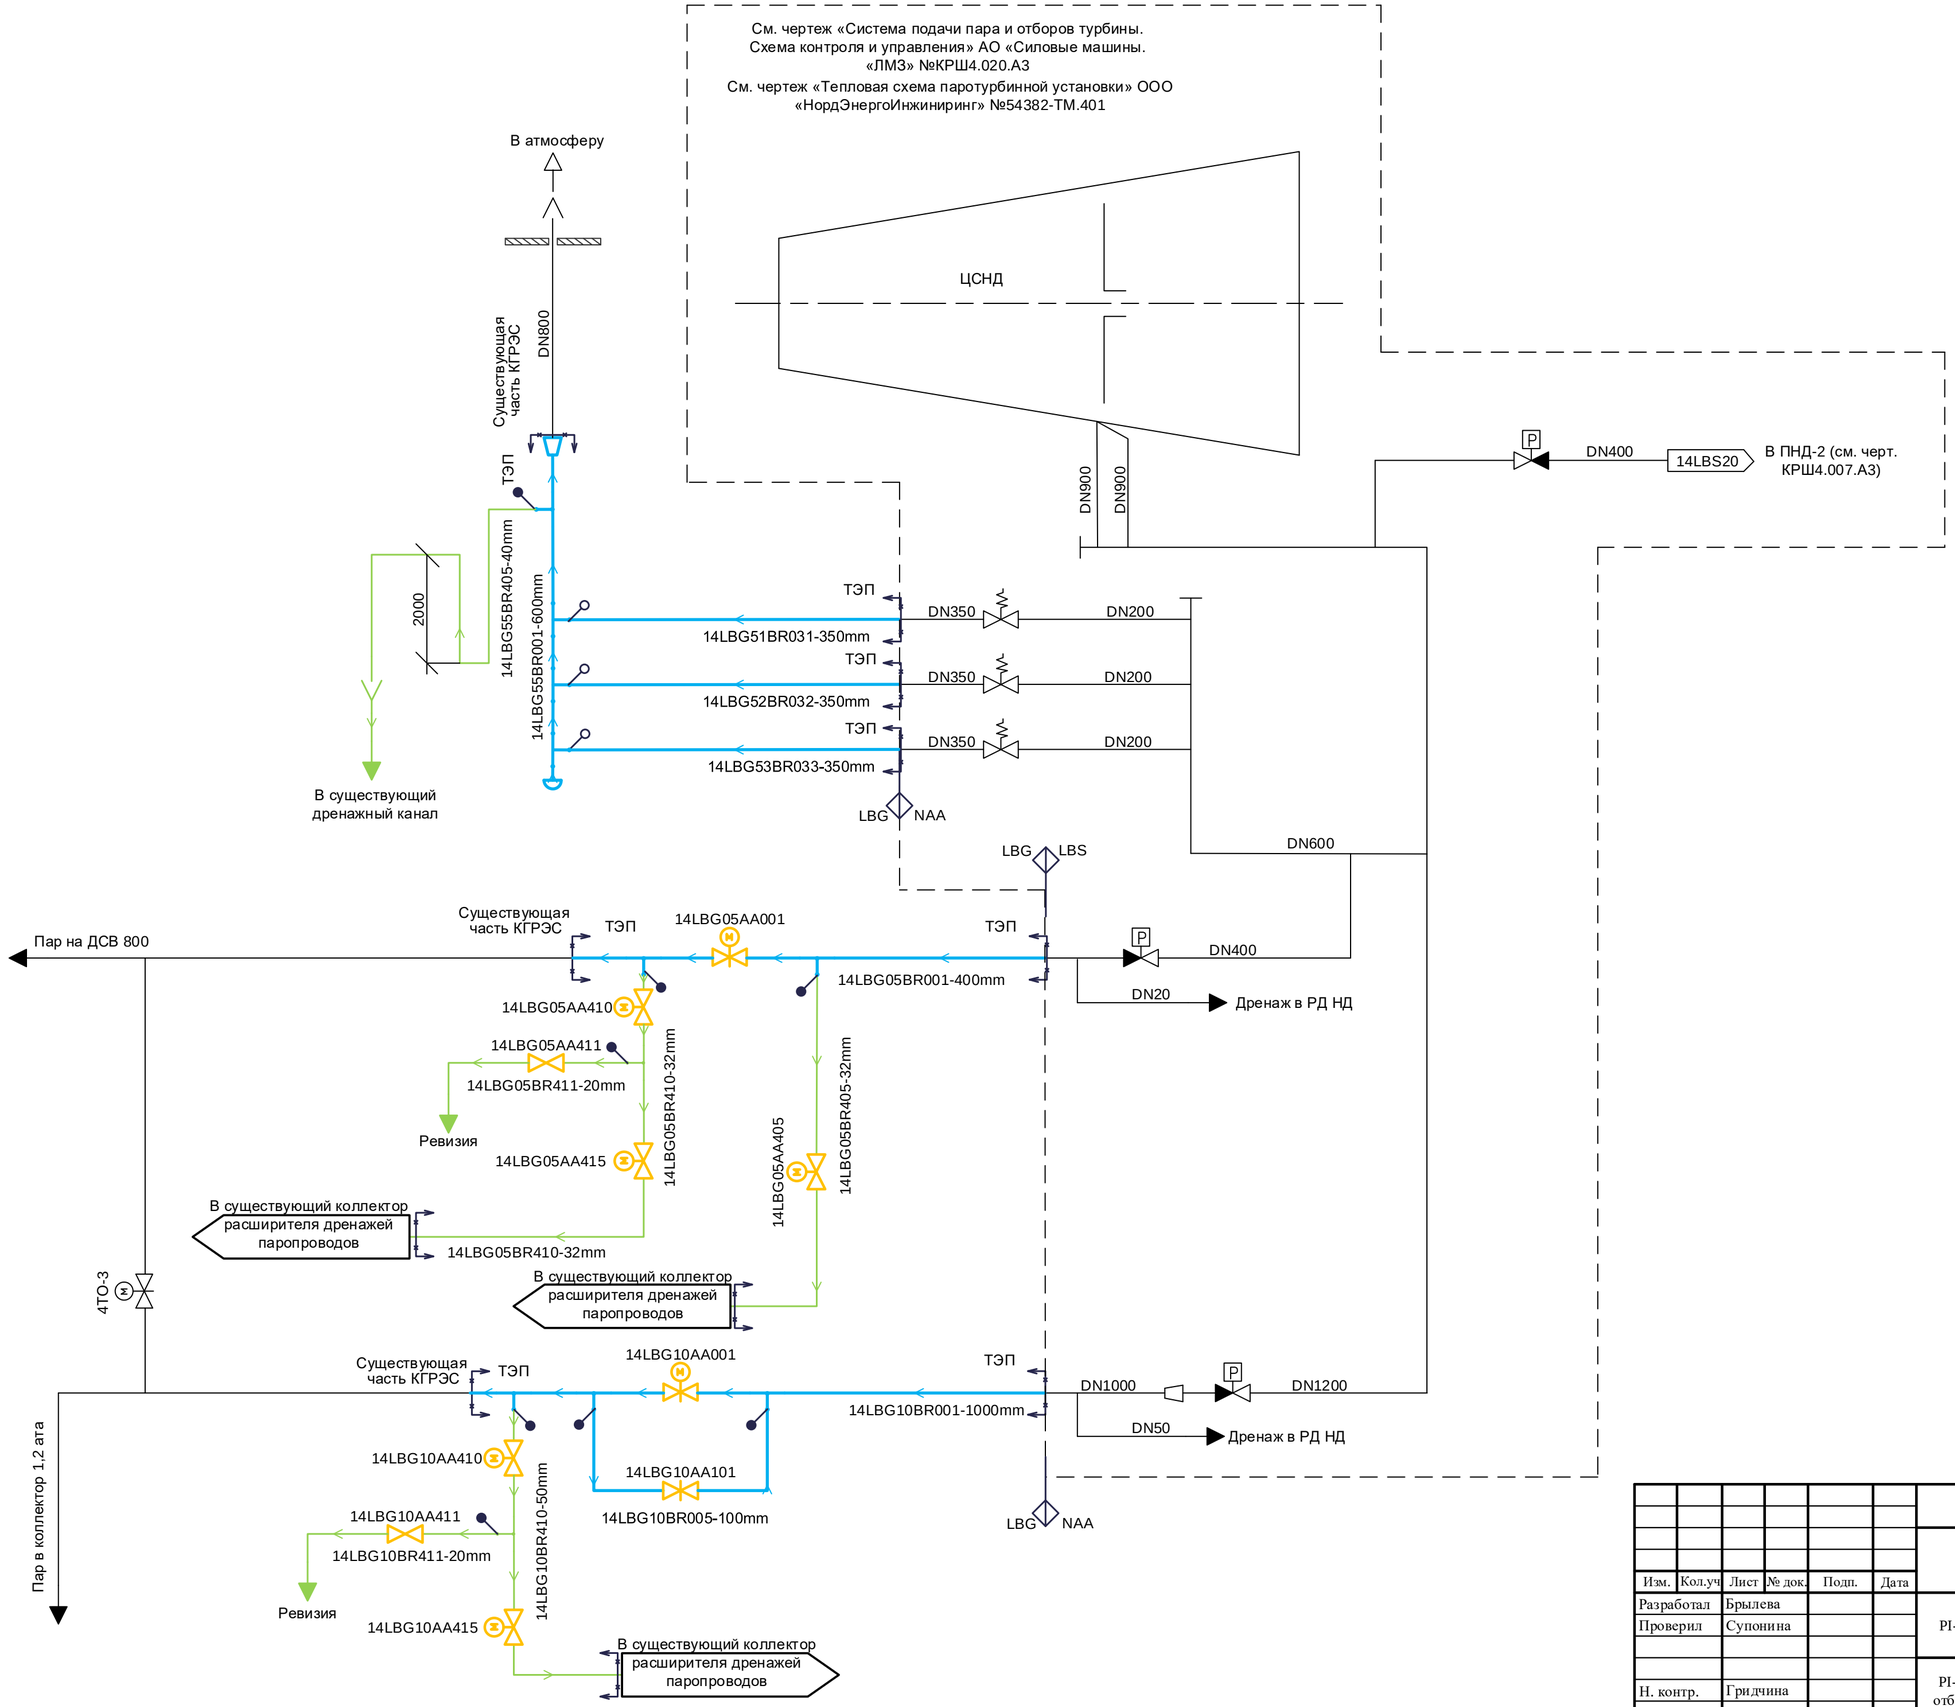

Изм.	Кол.уч	Лист	№ док.	Подп.	Дата	181M1D-10UHJ-4607-TD.M
						Модернизация генерирующего объекта "Киришская ГРЭС (Г-4т)"
Разработал		Брылева				Главный корпус PI-диаграмма пара теплофикационного отбора собственных нужд
Проверил		Супонина				Стадия: Р; Лист: 2; Листов:
Н. контр.		Гридчина				PI-диаграмма пара теплофикационного отбора собственных нужд. Система LBG
						АКЦИОНЕРНОЕ ОБЩЕСТВО ИНСТИТУТ ТЕПЛОЭЛЕКТРОПРОЕКТ Г. МОСКВА

Согласовано
ОАСУ Соболева
Взам. инв. №
Подпись и дата
Инв. № подл.

Формат А2