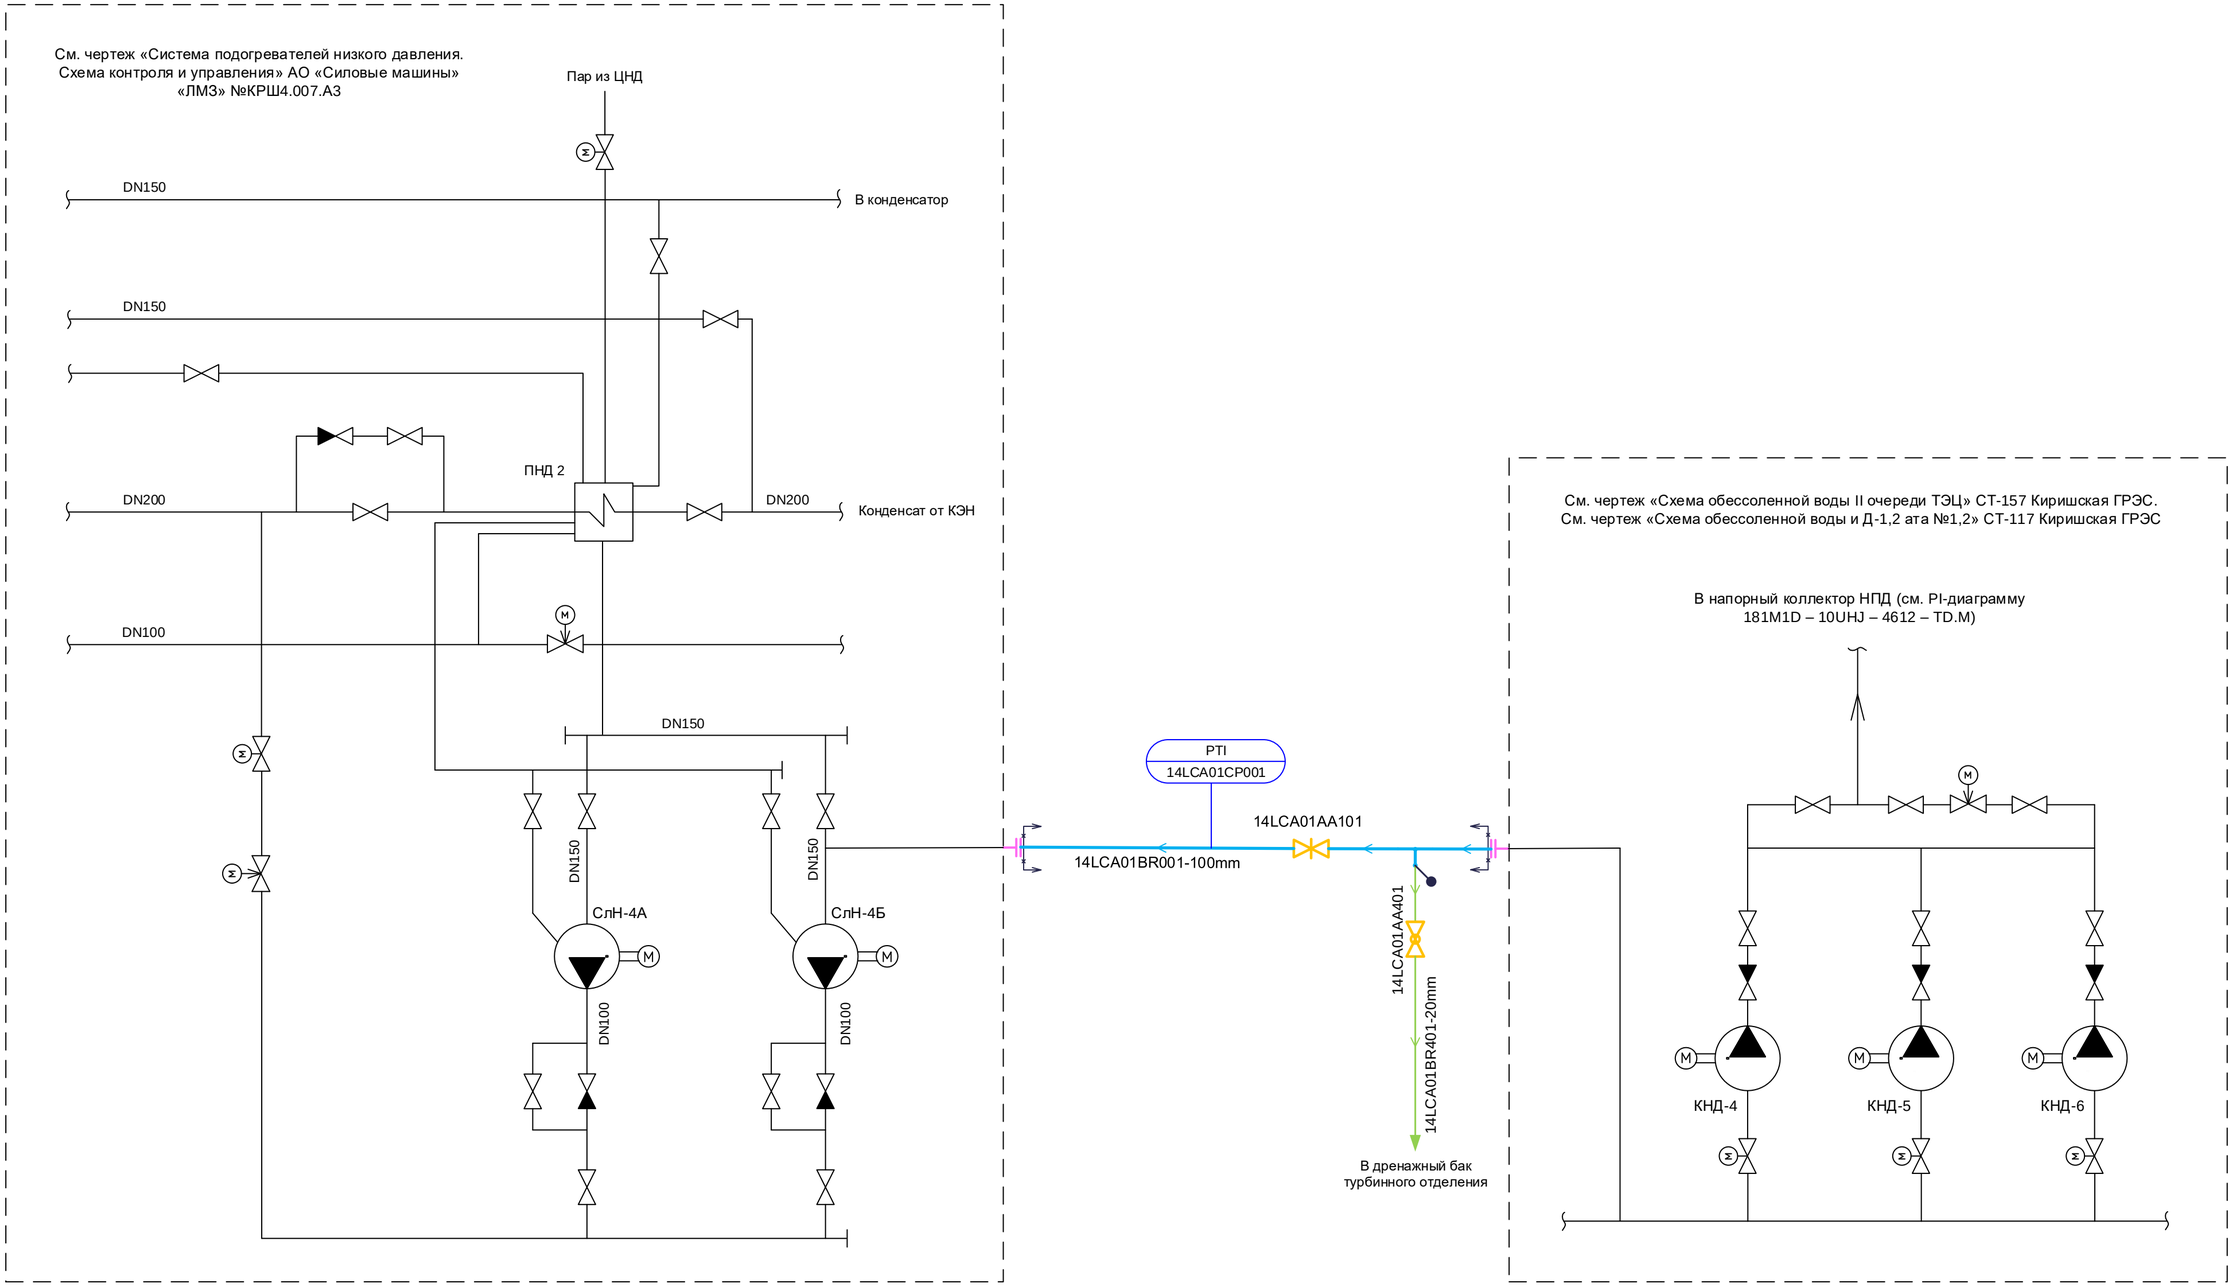

Существующая часть КГРЭС

ТЭП

- граница проектирования

1	-	Зам	1326-22			
Изм.	Кол.уч	Лист	№ док.	Подп.	Дата	
Разработал		Дадыко				
Проверил		Супонина				
Н. контр.		Черемушкина				

181M1D – 10UHJ – 4610 – TD.M

Модернизация генерирующего объекта Киришская ГРЭС (Г-4т)

Главный корпус.
PI-диаграмма трубопроводов подачи основного конденсата от КНД в систему регенерации НД

Стадия	Лист	Листов
Р	2	

PI-диаграмма трубопроводов подачи основного конденсата от КНД в систему регенерации НД. Система LCA

АКЦИОНЕРНОЕ ОБЩЕСТВО ИНСТИТУТ ТЕПЛОЭЛЕКТРОПРОЕКТ Г. МОСКВА

Согласовано
ОАСУ Соболева

Взам. инв. №

Подпись и дата

Инв. № подл.

Формат А2