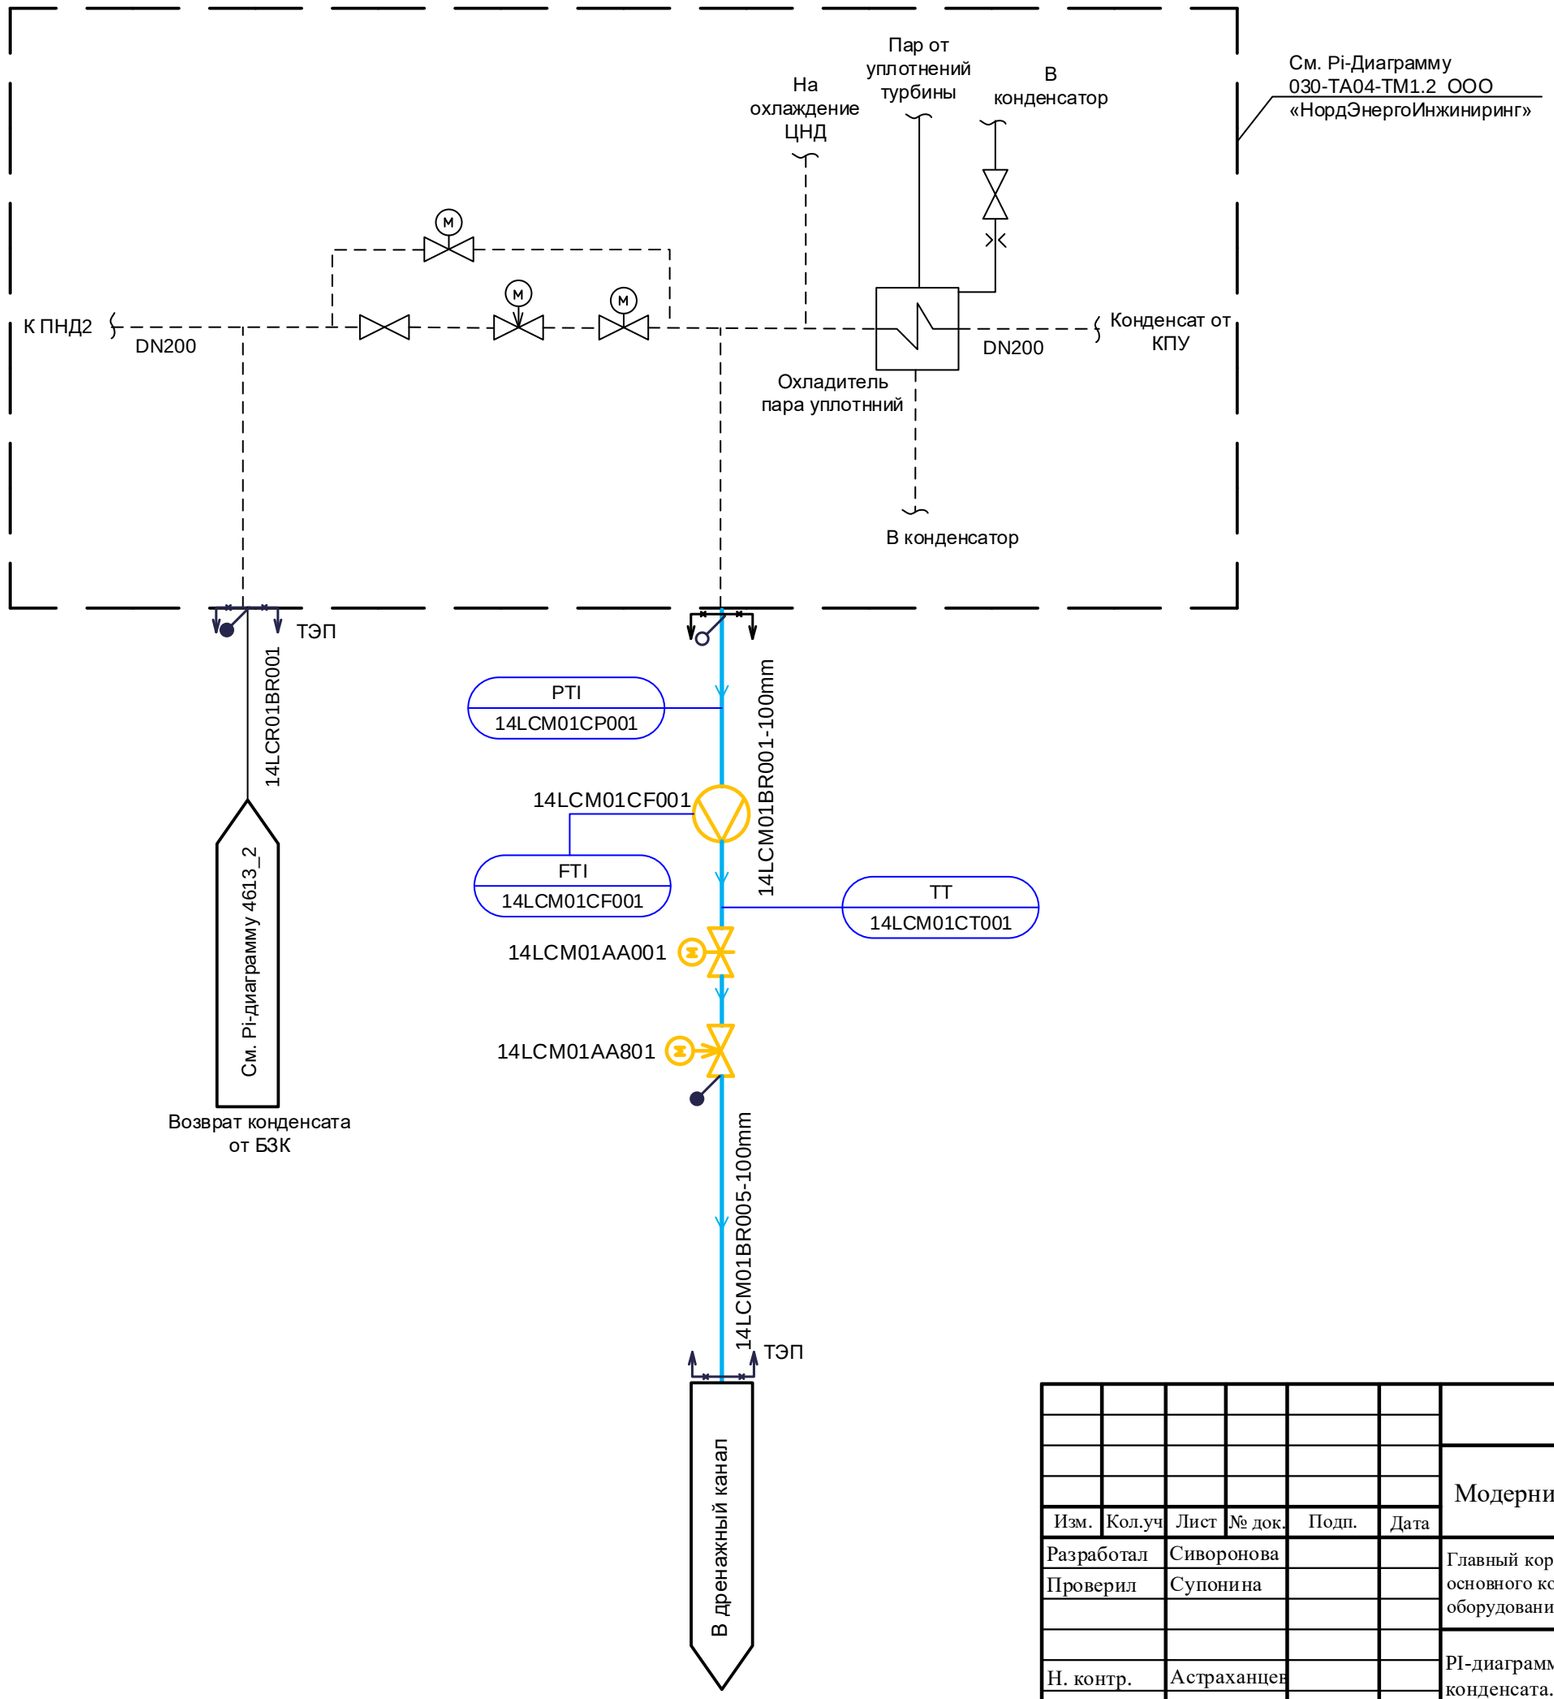

Согласовано

Соболева

ОАСУ

Взам. инв. №

Подпись и дата

Инв. № подл.

Изм.	Кол.уч	Лист	№ док.	Подп.	Дата
Разработал		Сиворонова			
Проверил		Супонина			
Н. контр.		Астраханцев			

181M1D – 10UHJ – 4611 – TD.M

Модернизация генерирующего объекта Киришская ГРЭС (Г-4т)

Главный корпус. PI-диаграмма трубопроводов основного конденсата на вспомогательное оборудование и грязный сброс

Стадия	Лист	Листов
Р	3	

PI-диаграмма трубопроводов «грязного» конденсата. Система LCM

АКЦИОНЕРНОЕ ОБЩЕСТВО ИНСТИТУТ ТЕПЛОЭЛЕКТРОПРОЕКТ Г. МОСКВА

Формат А3