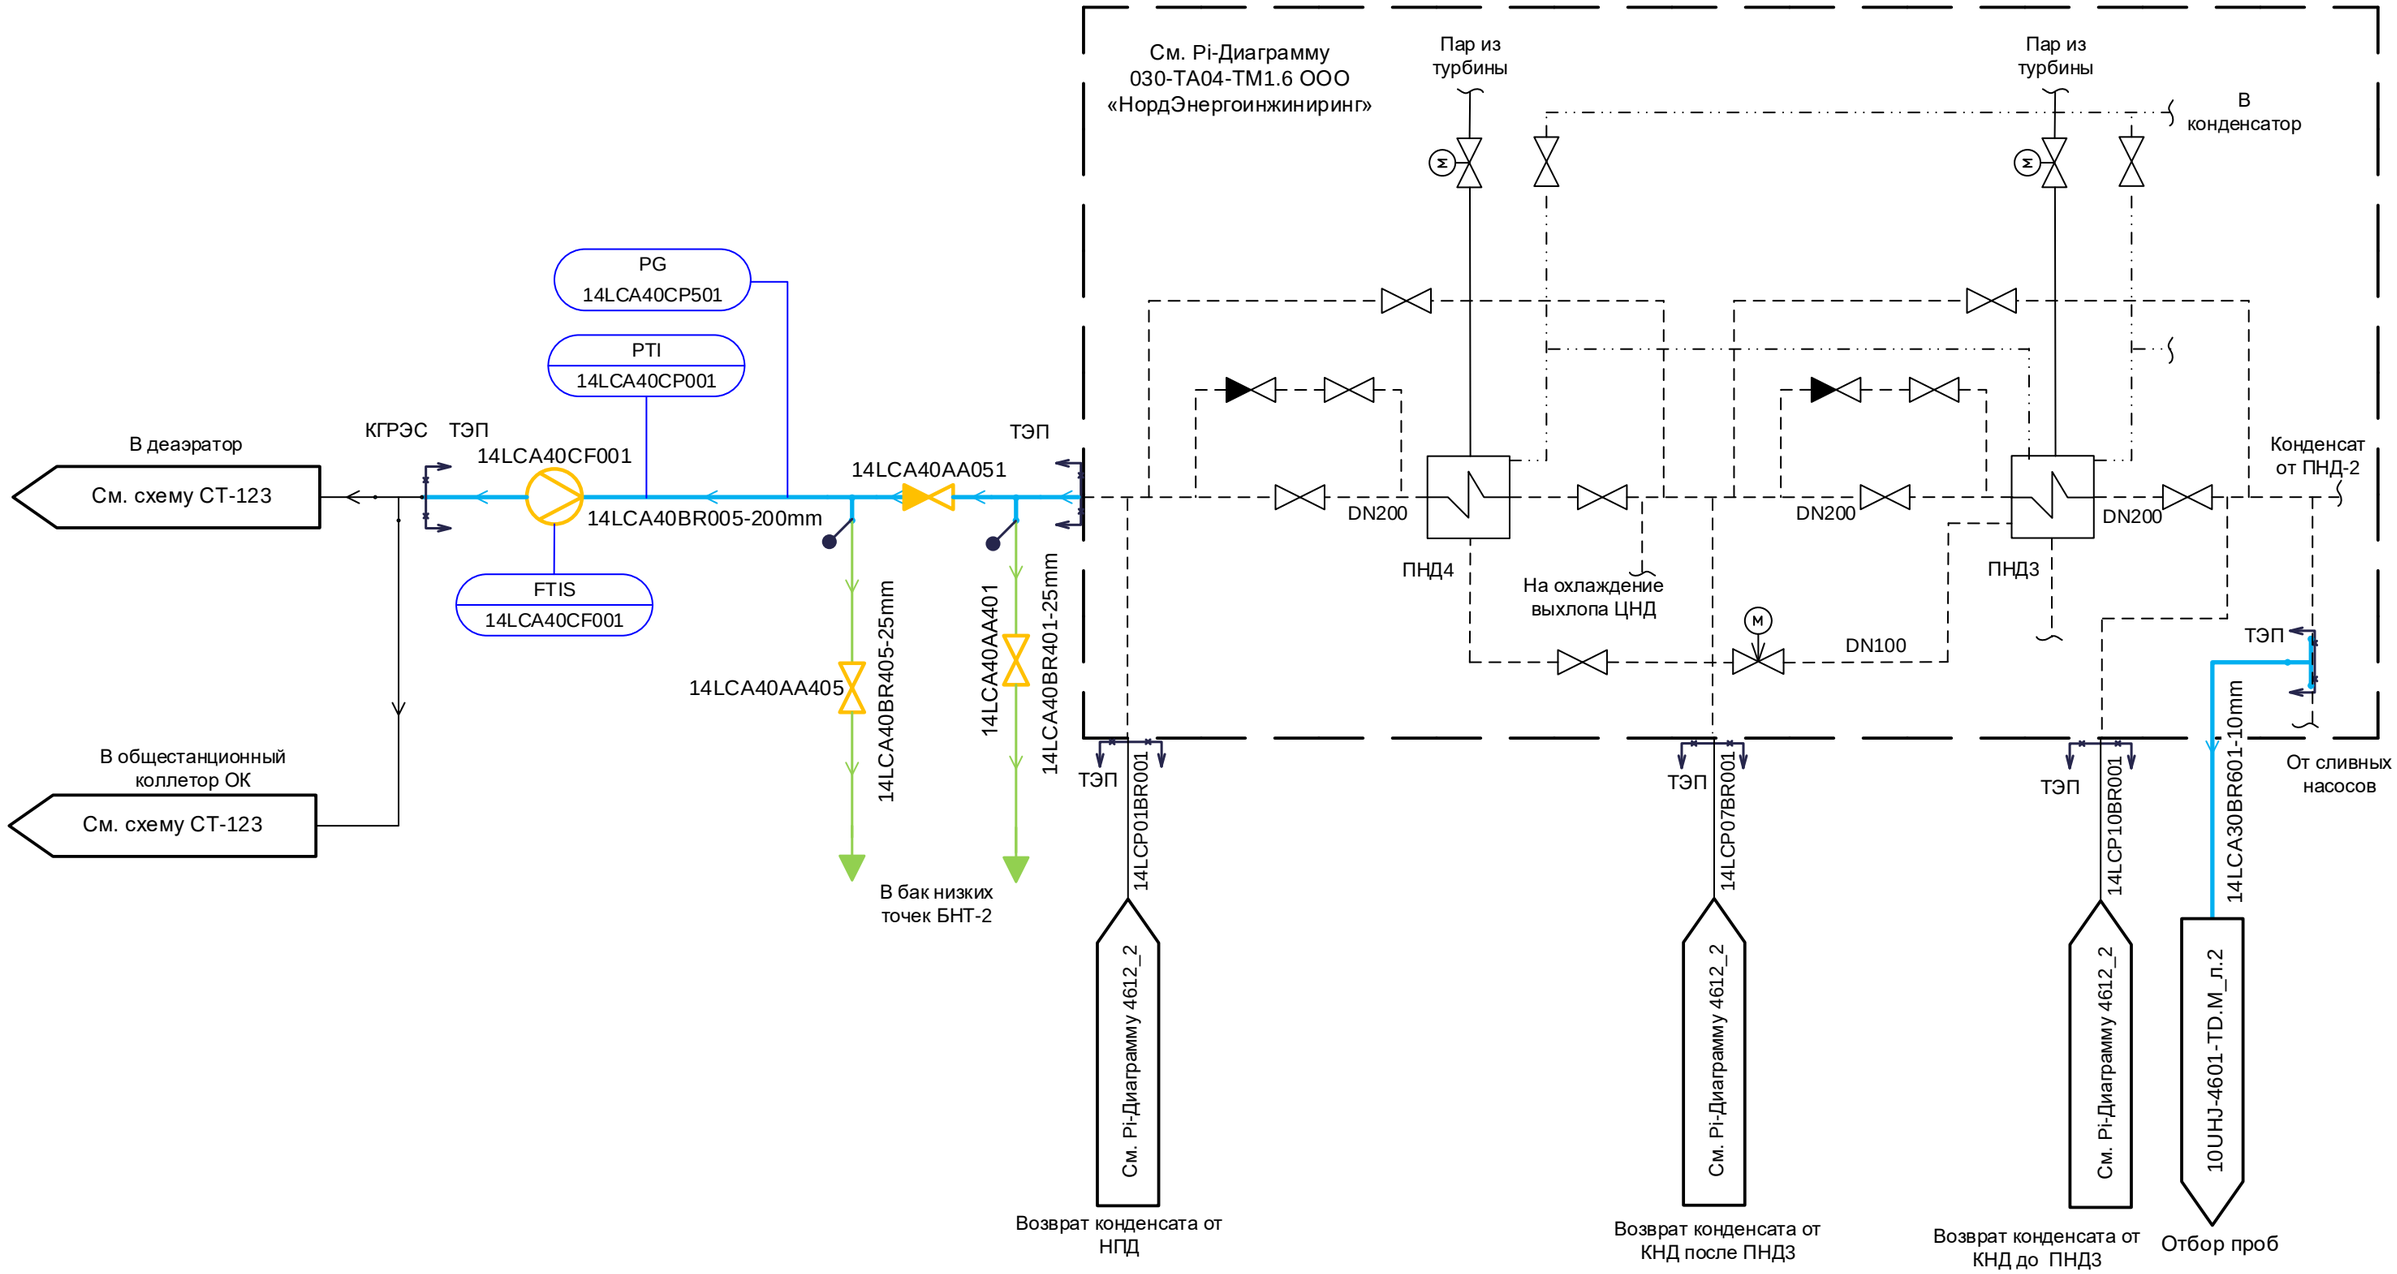

1	-	Зам.	328-22			181M1D – 10UHJ – 4611 – TD.M
Изм.	Кол.уч	Лист	№ док.	Подп.	Дата	Модернизация генерирующего объекта Киришская ГРЭС (Г-4т)
Разработал		Сиворонова				Главный корпус. PI-диаграмма трубопроводов основного конденсата на вспомогательное оборудование и грязный сброс
Проверил		Супонина				Стадия: Р; Лист: 4; Листов:
Н. контр.		Астраханцев				PI-диаграмма трубопроводов подачи основного конденсата от ПНД4. Система LCA

АКЦИОНЕРНОЕ ОБЩЕСТВО ИНСТИТУТ ТЕПЛОЭЛЕКТРОПРОЕКТ Г. МОСКВА

Согласовано
Соболева
ОАСУ
Взам. инв. №
Подпись и дата
Инв. № подл.

Формат А3