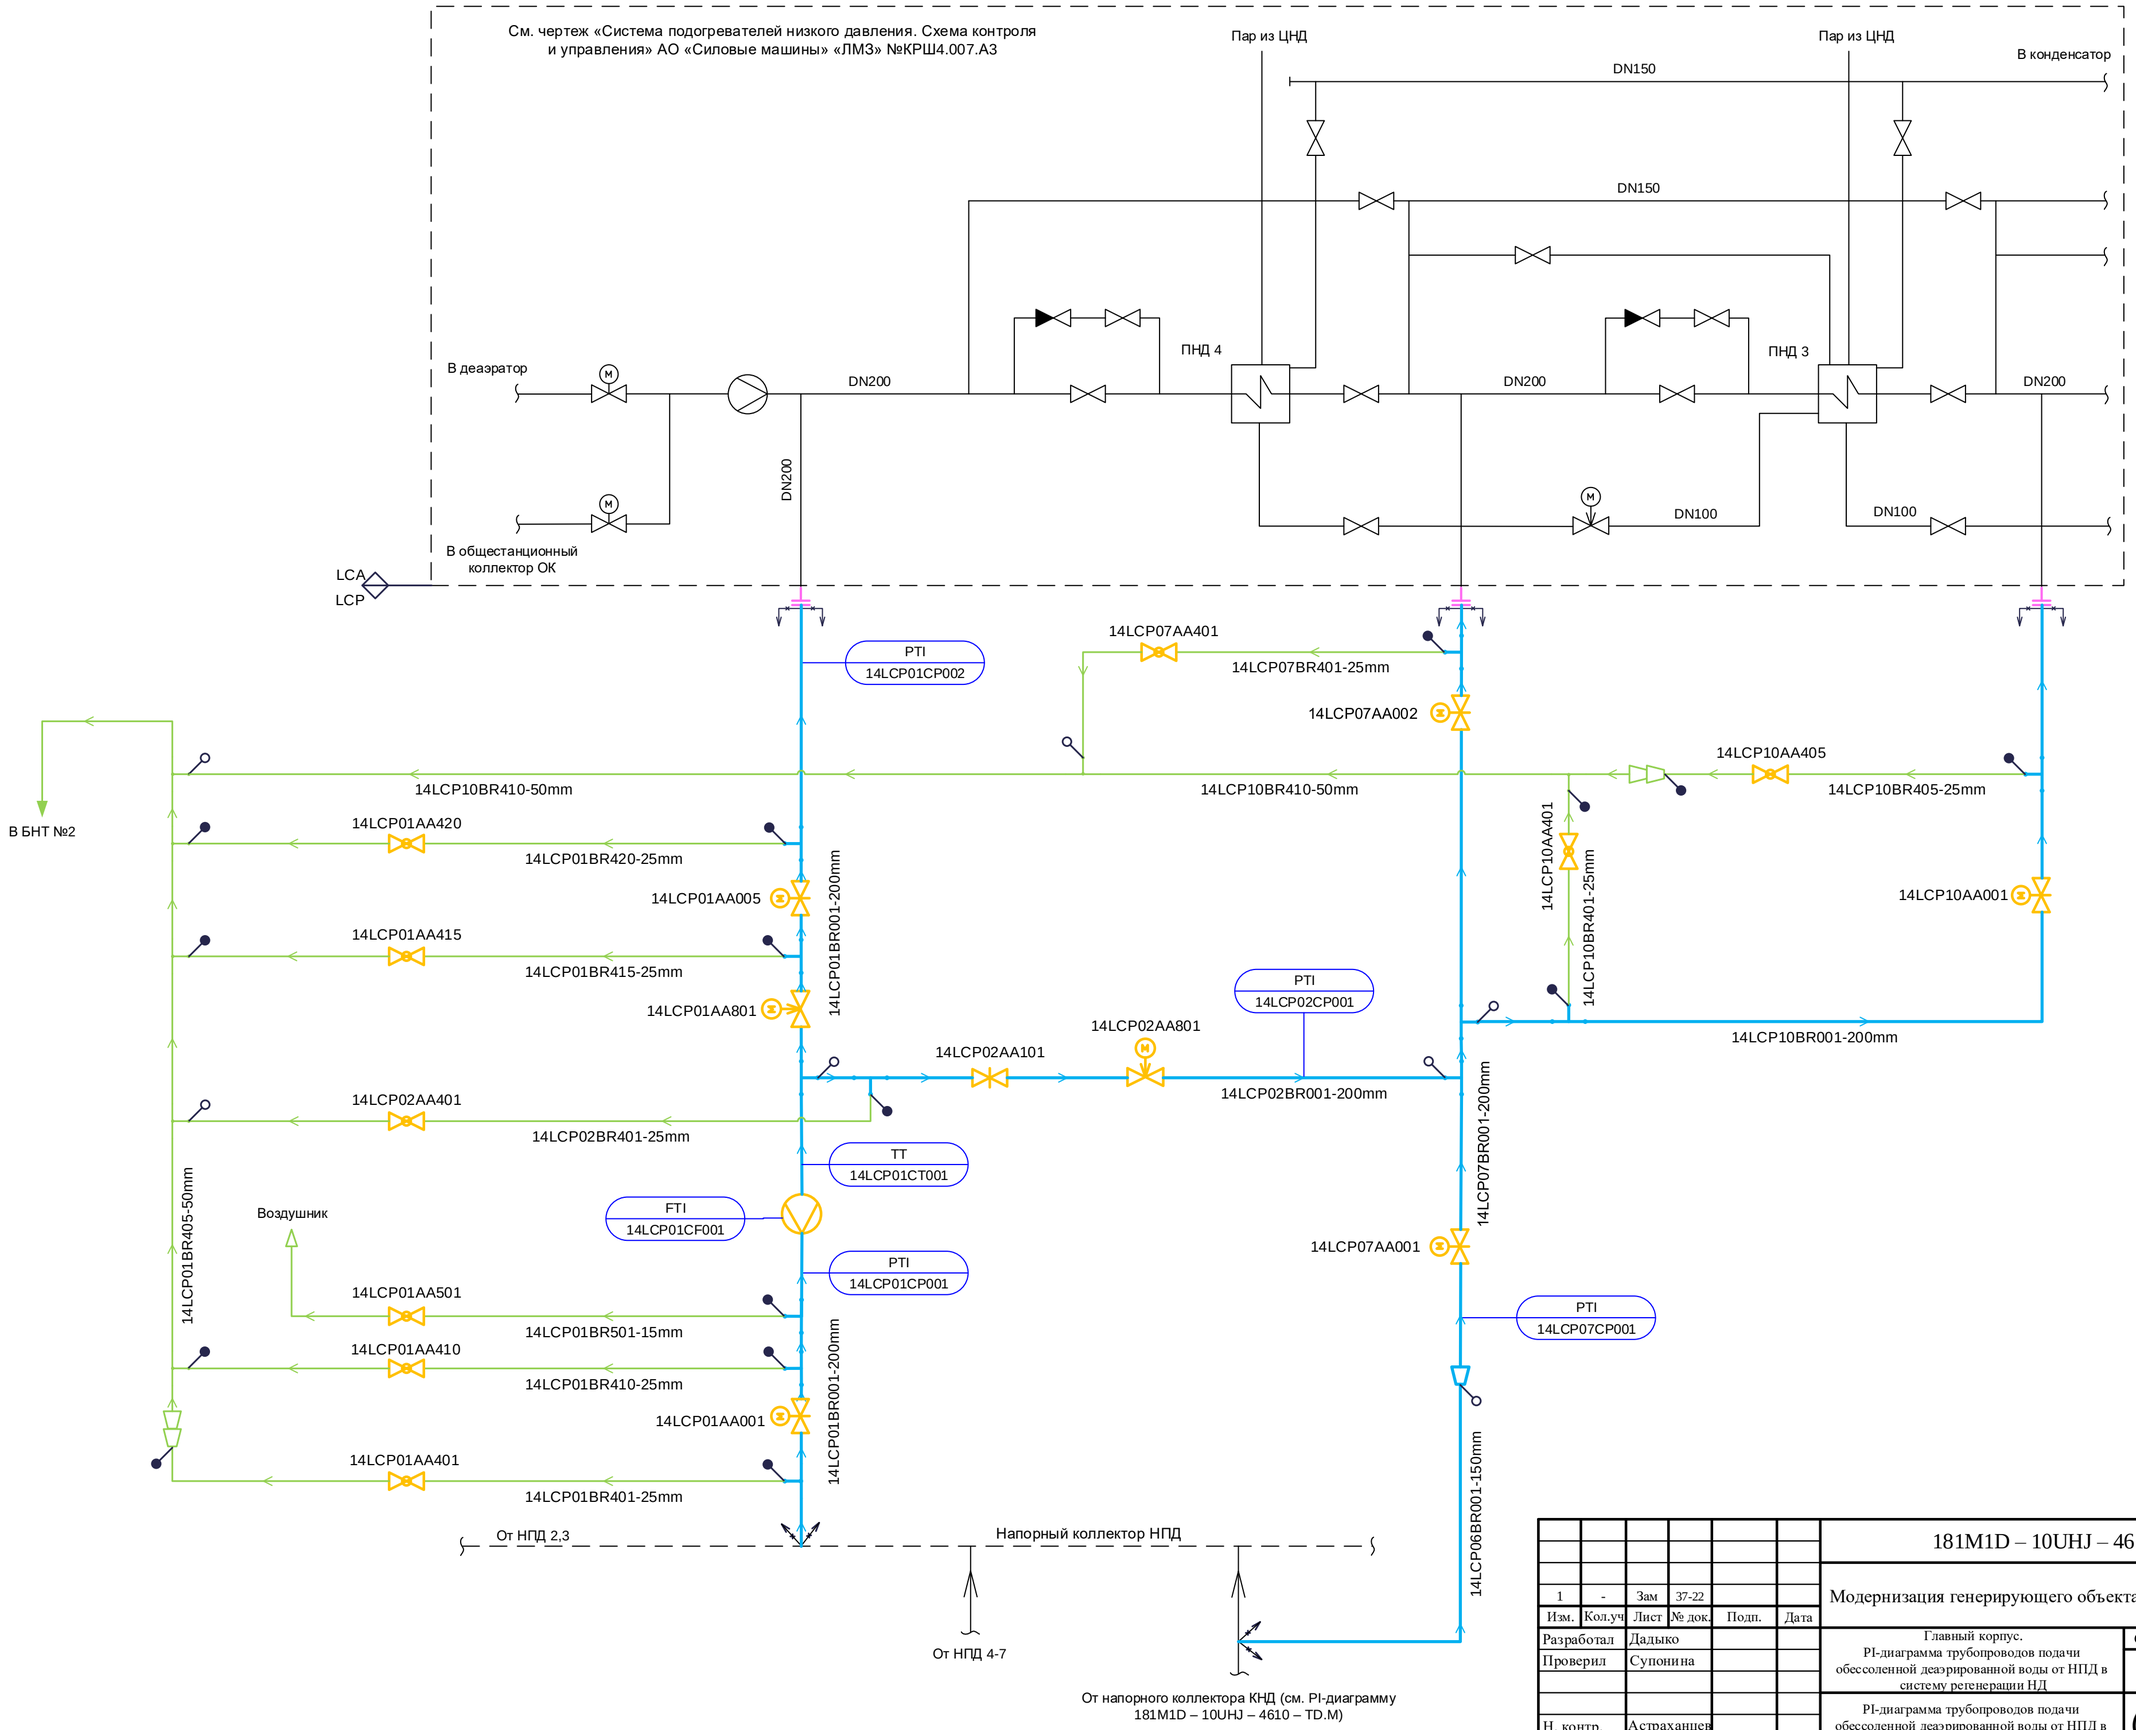

1	-	Зам	37-22			
Изм.	Кол.уч	Лист	№ док.	Подп.	Дата	
Разработал		Дадыко				
Проверил		Супонина				
Н. контр.		Астраханцев				

181M1D – 10UHJ – 4612 – TD.M

Модернизация генерирующего объекта Киришская ГРЭС (Г-4т)

Главный корпус. PI-диаграмма трубопроводов подачи обессоленной деаэрированной воды от НПД в систему регенерации НД

Стадия	Лист	Листов
Р	2	

PI-диаграмма трубопроводов подачи обессоленной деаэрированной воды от НПД в систему регенерации НД. Система LCP

АКЦИОНЕРНОЕ ОБЩЕСТВО ИНСТИТУТ ТЕПЛОЭЛЕКТРОПРОЕКТ г. МОСКВА

Согласовано
ОДСУ Соболева

Взам. инв. №

Подпись и дата

Инв. № подл.

Формат А2