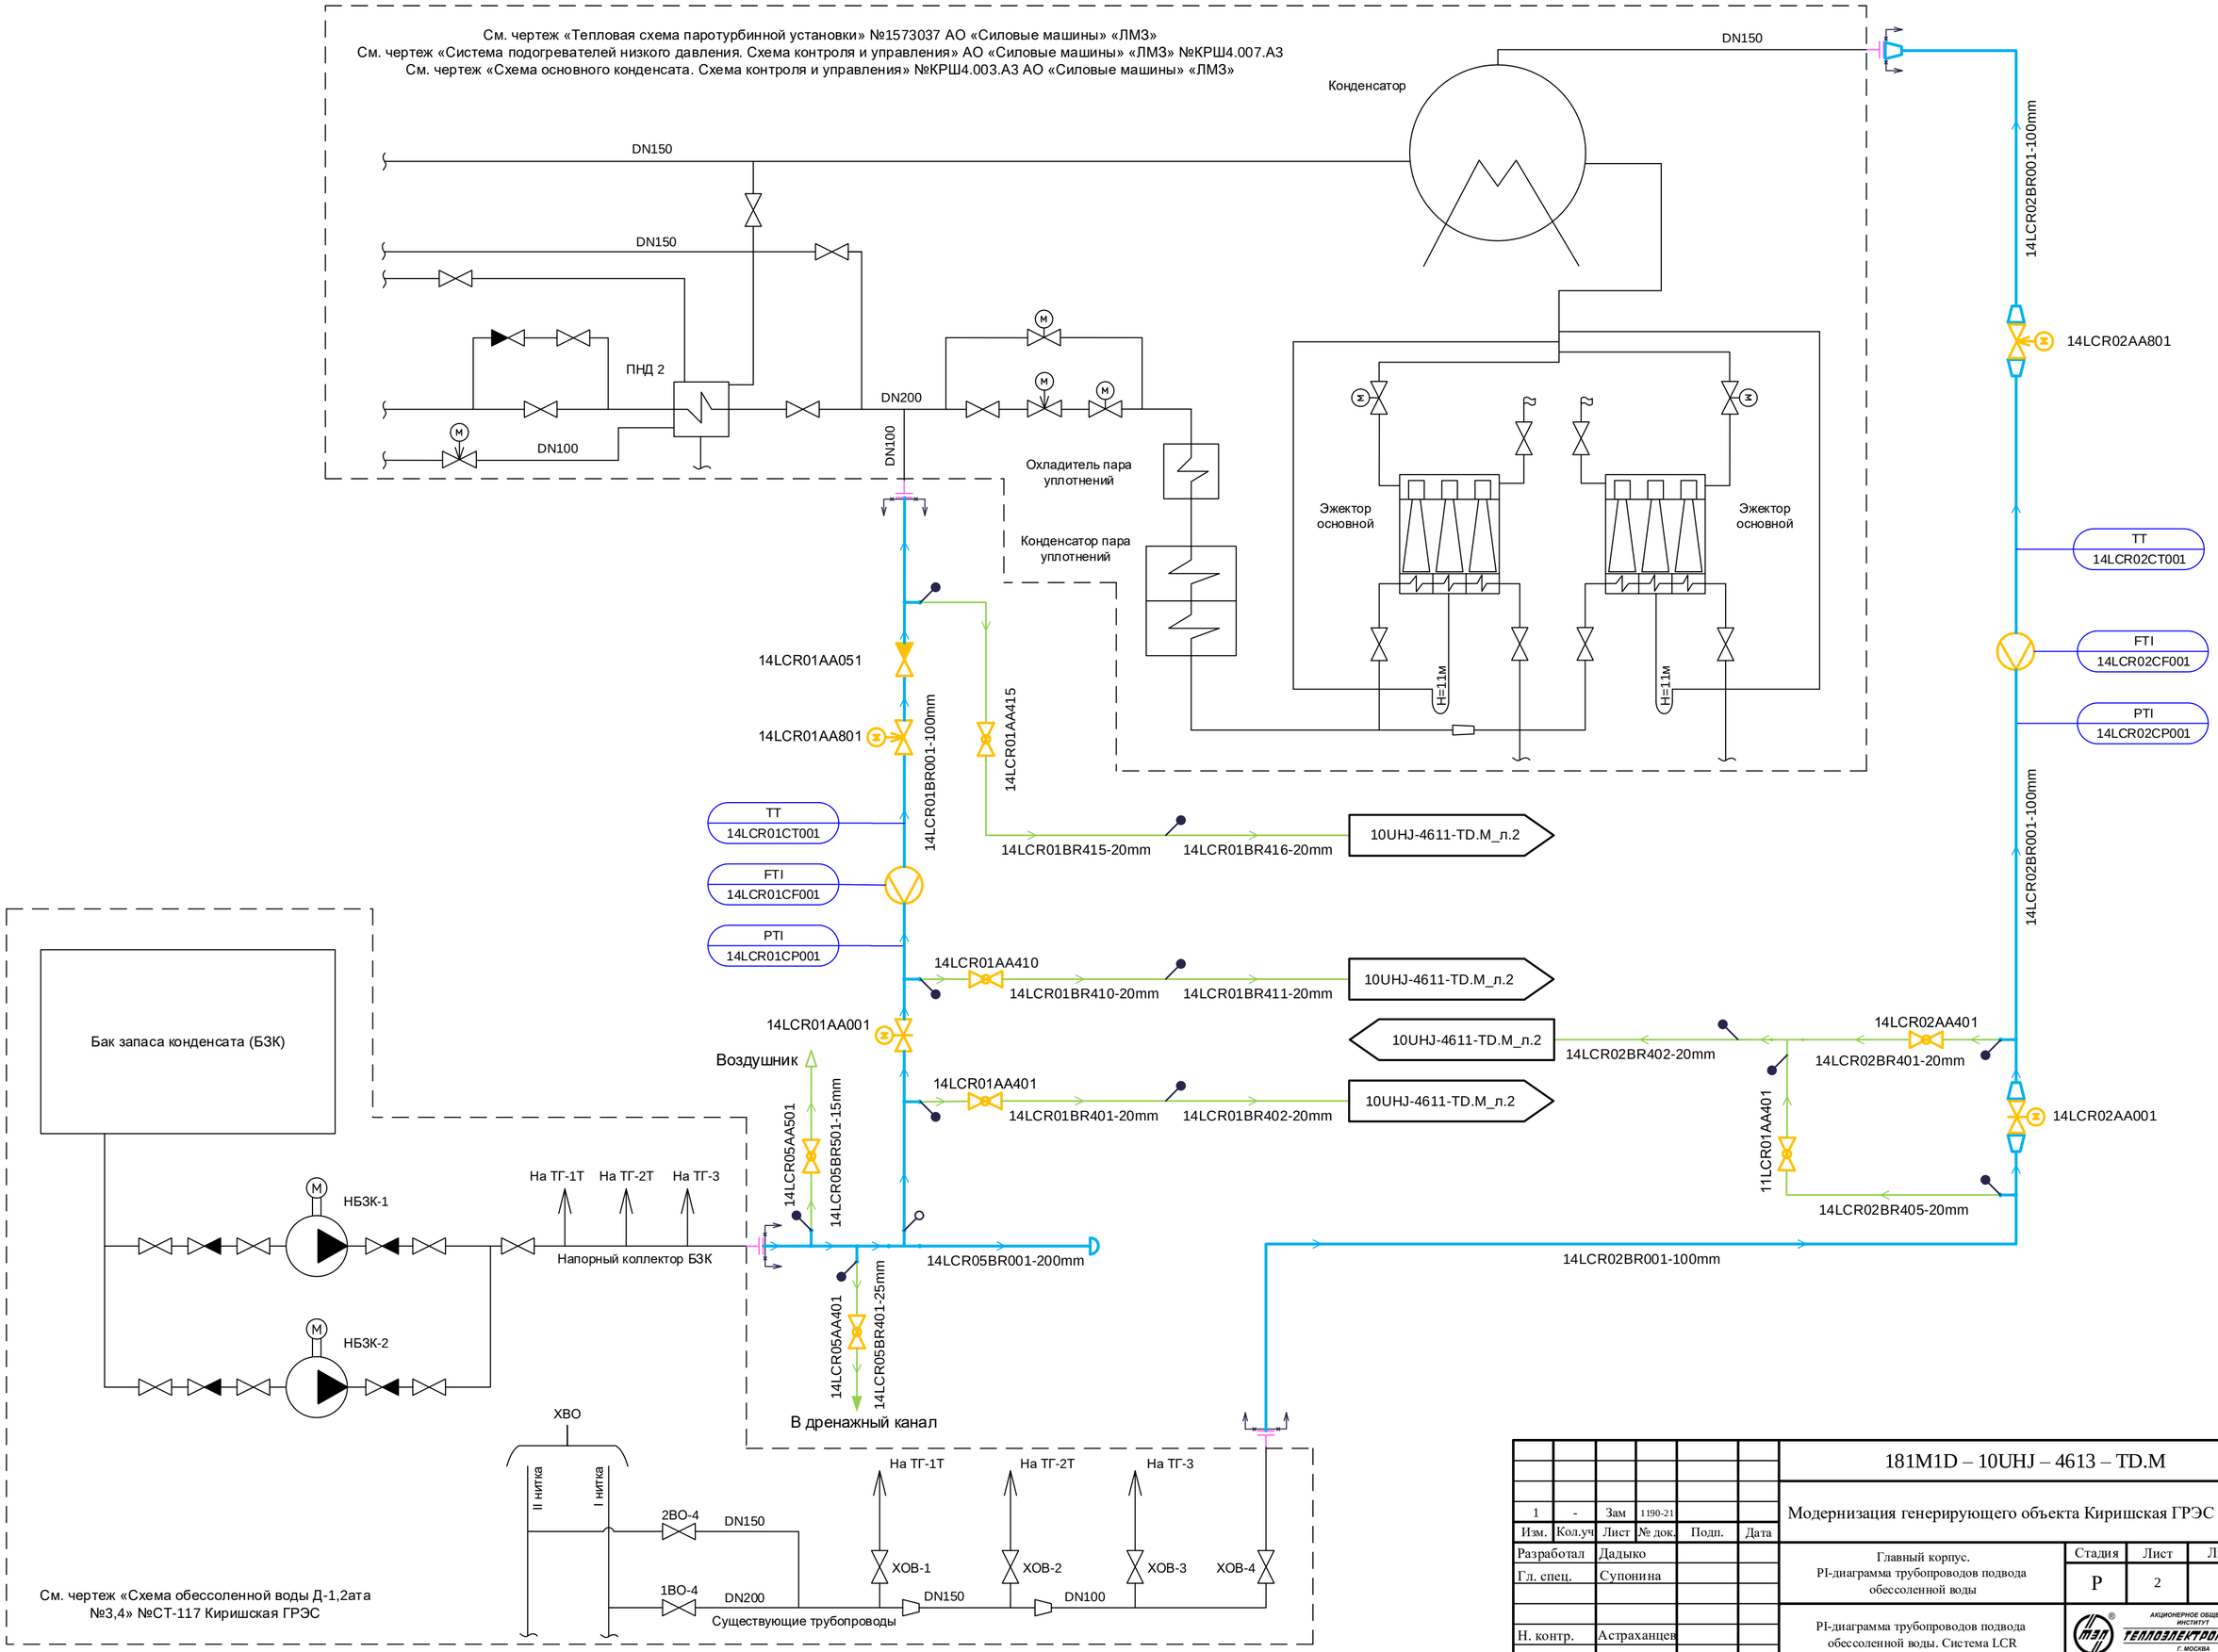

1	-	Зам	1190-21			
Изм.	Кол.уч	Лист	№ док.	Подп.	Дата	
Разработал		Дадыко				
Гл. спец.		Супонина				
Н. контр.		Астраханцев				

181M1D – 10UHJ – 4613 – TD.M

Модернизация генерирующего объекта Киришская ГРЭС (Г-4т)

Главный корпус. PI-диаграмма трубопроводов подвода обессоленной воды

Стадия	Лист	Листов
Р	2	

PI-диаграмма трубопроводов подвода обессоленной воды. Система LCR

АКЦИОНЕРНОЕ ОБЩЕСТВО ИНСТИТУТ ТЕПЛОЭЛЕКТРОПРОЕКТ Г. МОСКВА

Согласовано: Соболева, ОАСУ

Взам. инв. №

Подпись и дата

Инв. № подл.

Формат А2