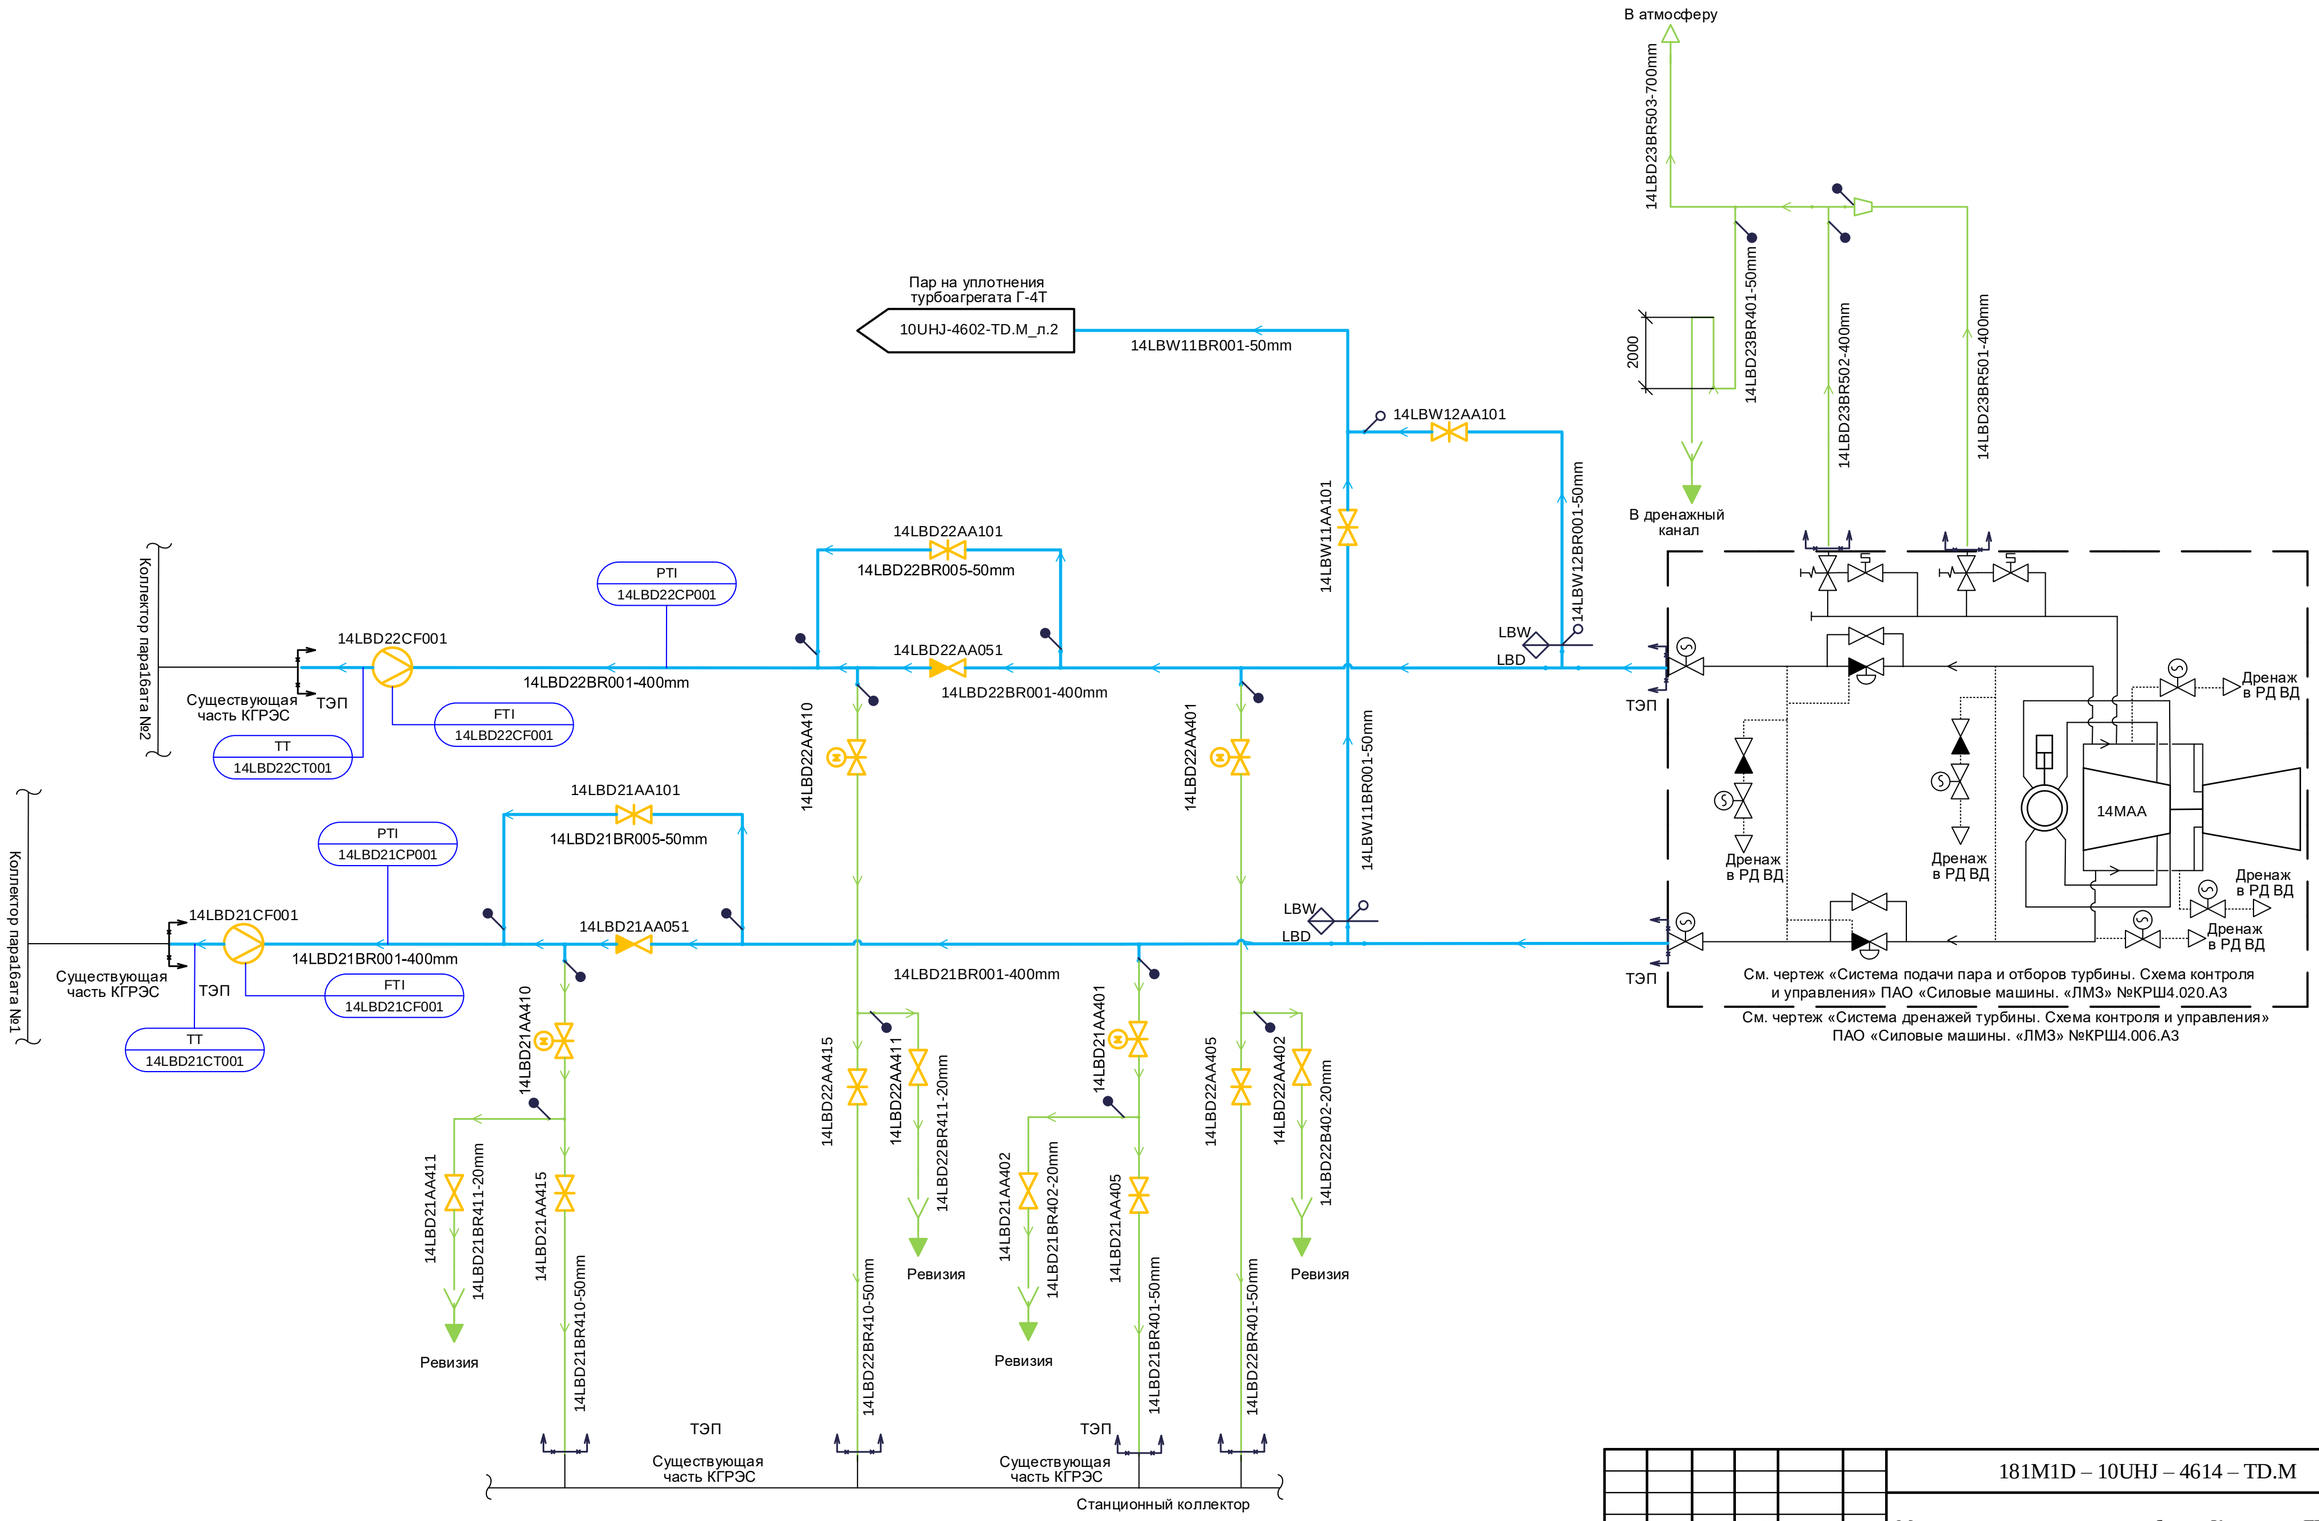

1	-	Зам	37-22			181M1D – 10UHJ – 4614 – TD.M
Изм.	Кол.уч	Лист	№ док.	Подп.	Дата	Модернизация генерирующего объекта Киришская ГРЭС (Г-4т)
Разработал		Сиворова				Главный корпус. PI-диаграмма трубопроводов пара на производство.
Проверил		Супонина				Стадия: Р; Лист: 2; Листов:
Н. контр.		Астраханцев				PI-диаграмма трубопроводов подачи пара на производство. Система LBD, LBW.

АКЦИОНЕРНОЕ ОБЩЕСТВО ИНСТИТУТ ТЕПЛОЭЛЕКТРОПРОЕКТ Г. МОСКВА

Согласовано: ОАСУ Соболева

Взам. инв. № | Подпись и дата | Инв. № подл.

Формат А2