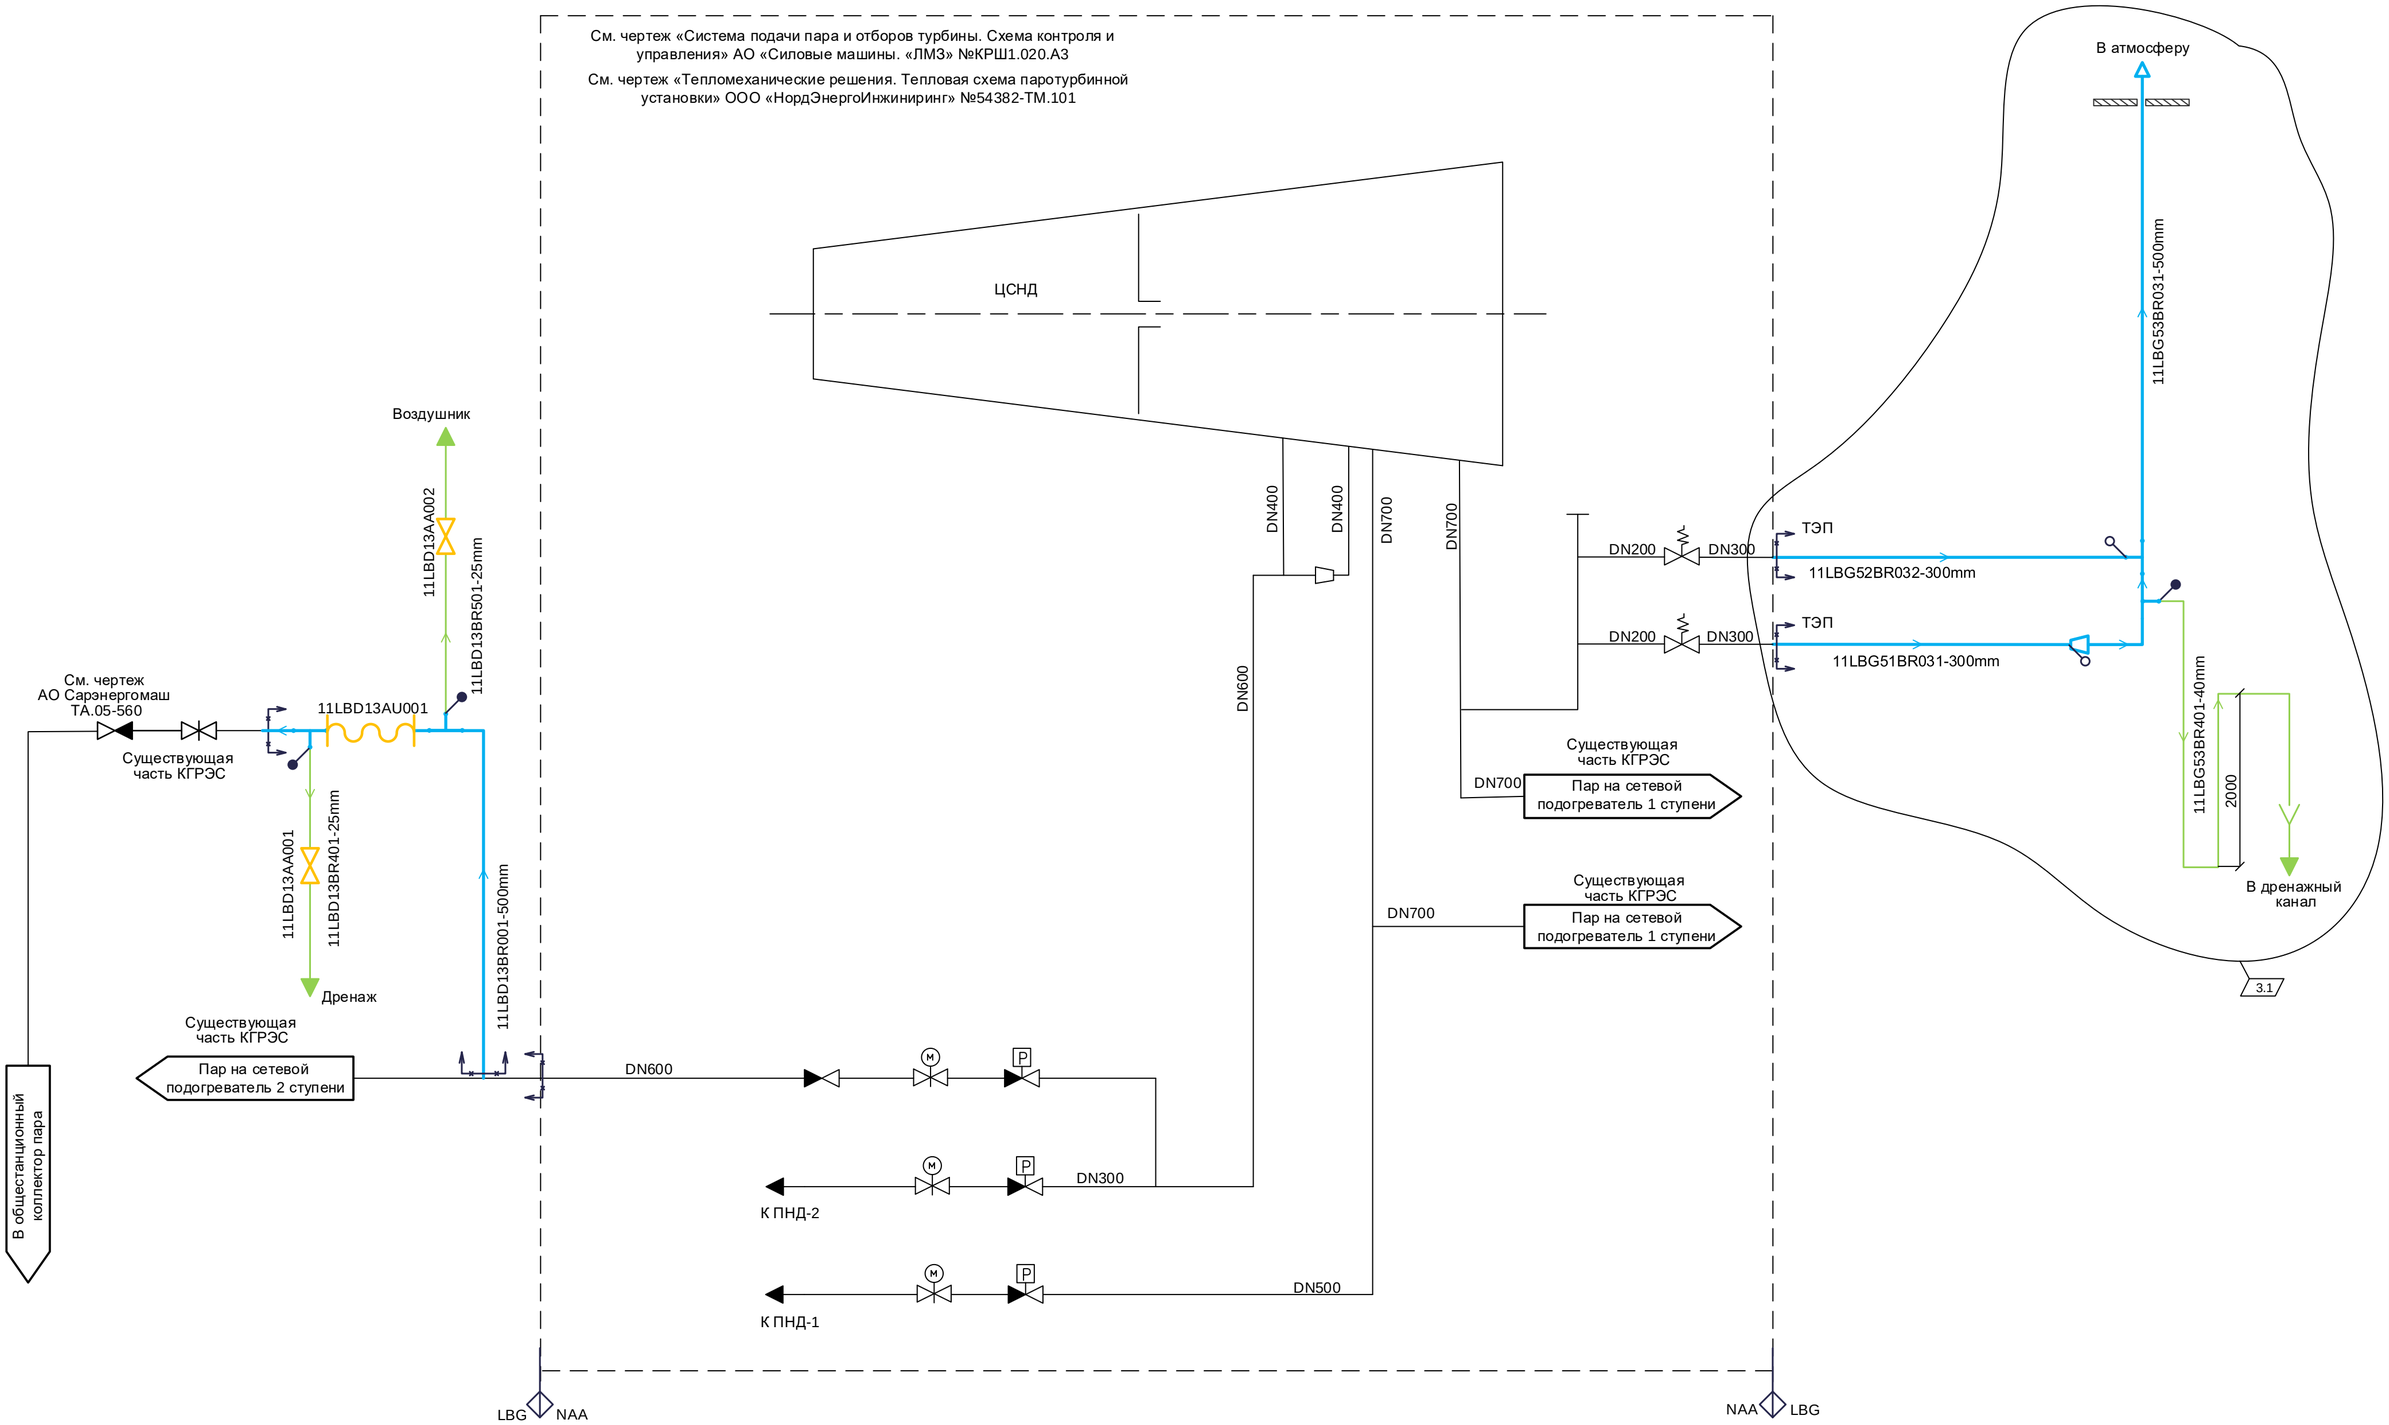

3	1	Изм.	453-23		03.23	
Изм.	Кол.уч	Лист	№ док.	Подп.	Дата	
Разработал		Гусев				
Проверил		Супонина				
Н. контр.		Черемушкина				

181M1D – 13UHJ – 5242 – TD.M

Модернизация генерирующего объекта Киришская ГРЭС (Г1-т)

Главный корпус. PI-диаграмма пара теплофикационного отбора собственных нужд

Стадия	Лист	Листов
Р	2	

PI-диаграмма пара теплофикационного отбора собственных нужд

АКЦИОНЕРНОЕ ОБЩЕСТВО ИНСТИТУТ ТЕПЛОЭЛЕКТРОПРОЕКТ Г. МОСКВА

Согласовано

Взам. инв. №

Подпись и дата

Инв. № подл.

Формат А2