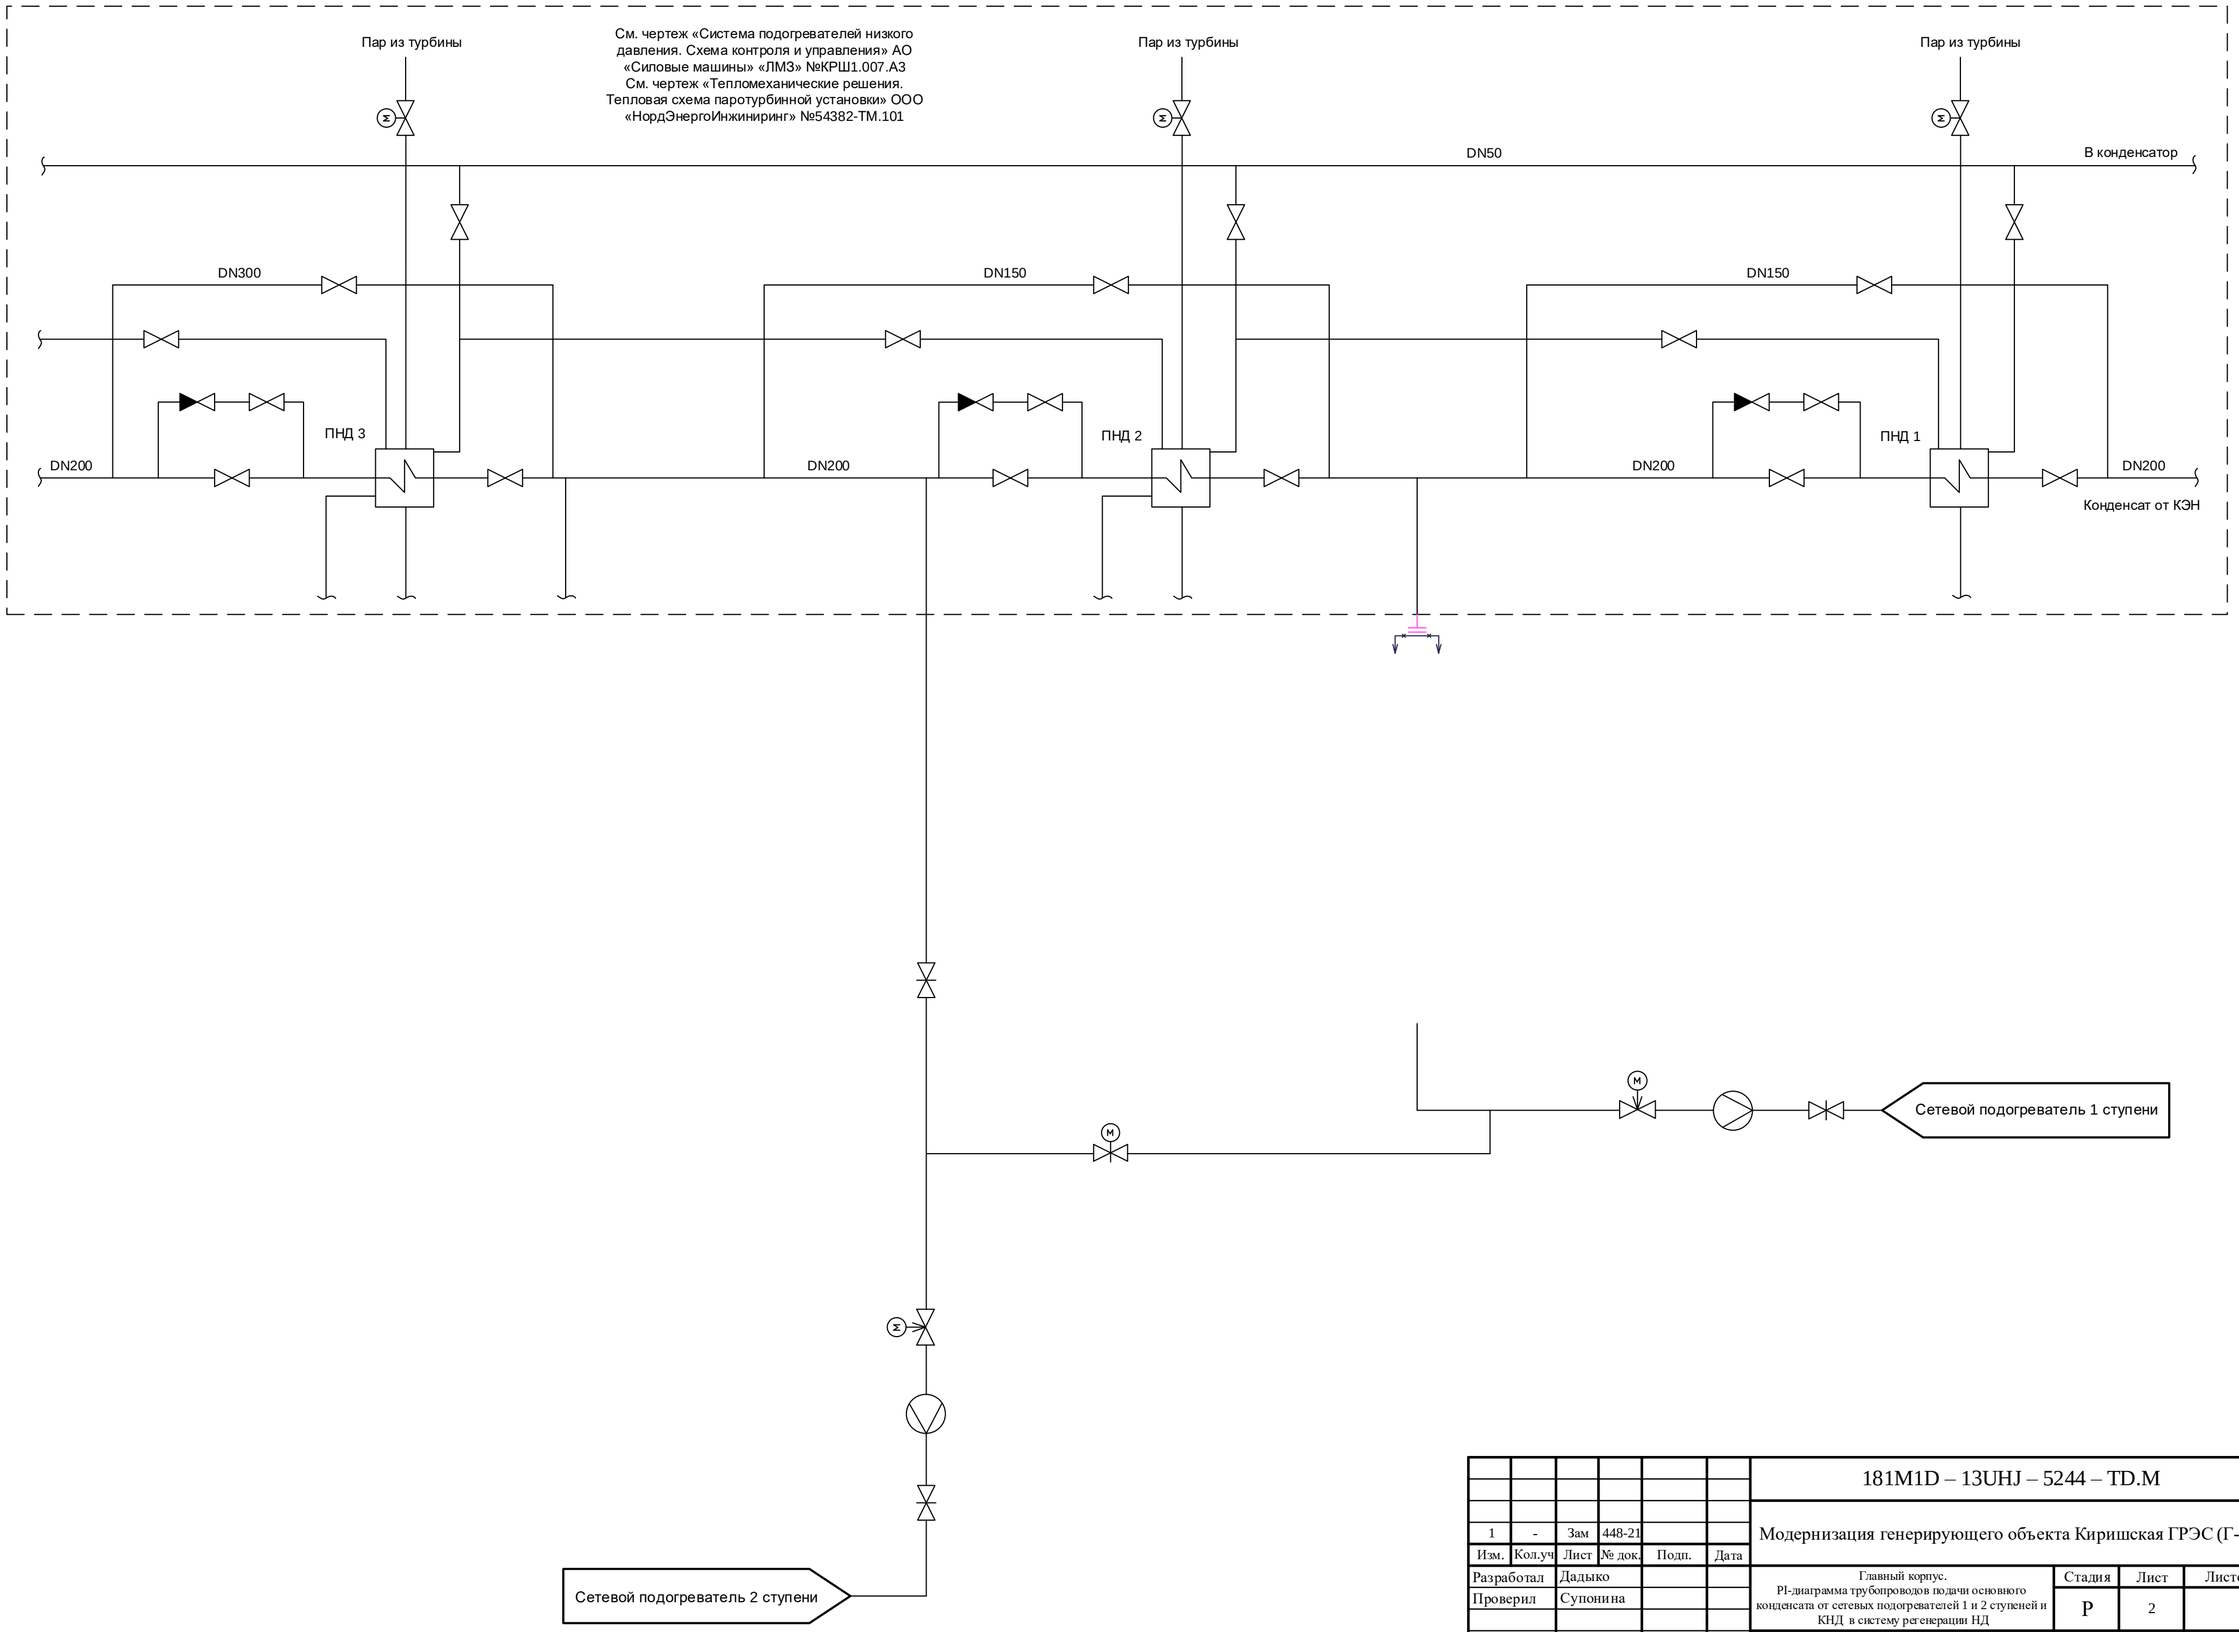

1	-	Зам	448-21			
Изм.	Кол.уч	Лист	№ док.	Подп.	Дата	
Разработал		Дадыко				
Проверил		Супонина				
Н. контр.		Астраханцев				

181M1D – 13UHJ – 5244 – TD.M

Модернизация генерирующего объекта Киришская ГРЭС (Г-1т)

Главный корпус.
PI-диаграмма трубопроводов подачи основного конденсата от сетевых подогревателей 1 и 2 ступеней и КНД в систему регенерации НД

Стадия	Лист	Листов
Р	2	

PI-диаграмма трубопроводов подачи основного конденсата от сетевых подогревателей 1 и 2 ступеней и КНД в систему регенерации НД. Система LCA

АКЦИОНЕРНОЕ ОБЩЕСТВО ИНСТИТУТ ТЕПЛОЭЛЕКТРОПРОЕКТ г. МОСКВА

Согласовано
ОАСУ Соболева

Взам. инв. №
Подпись и дата
Инв. № подл.

Формат А2