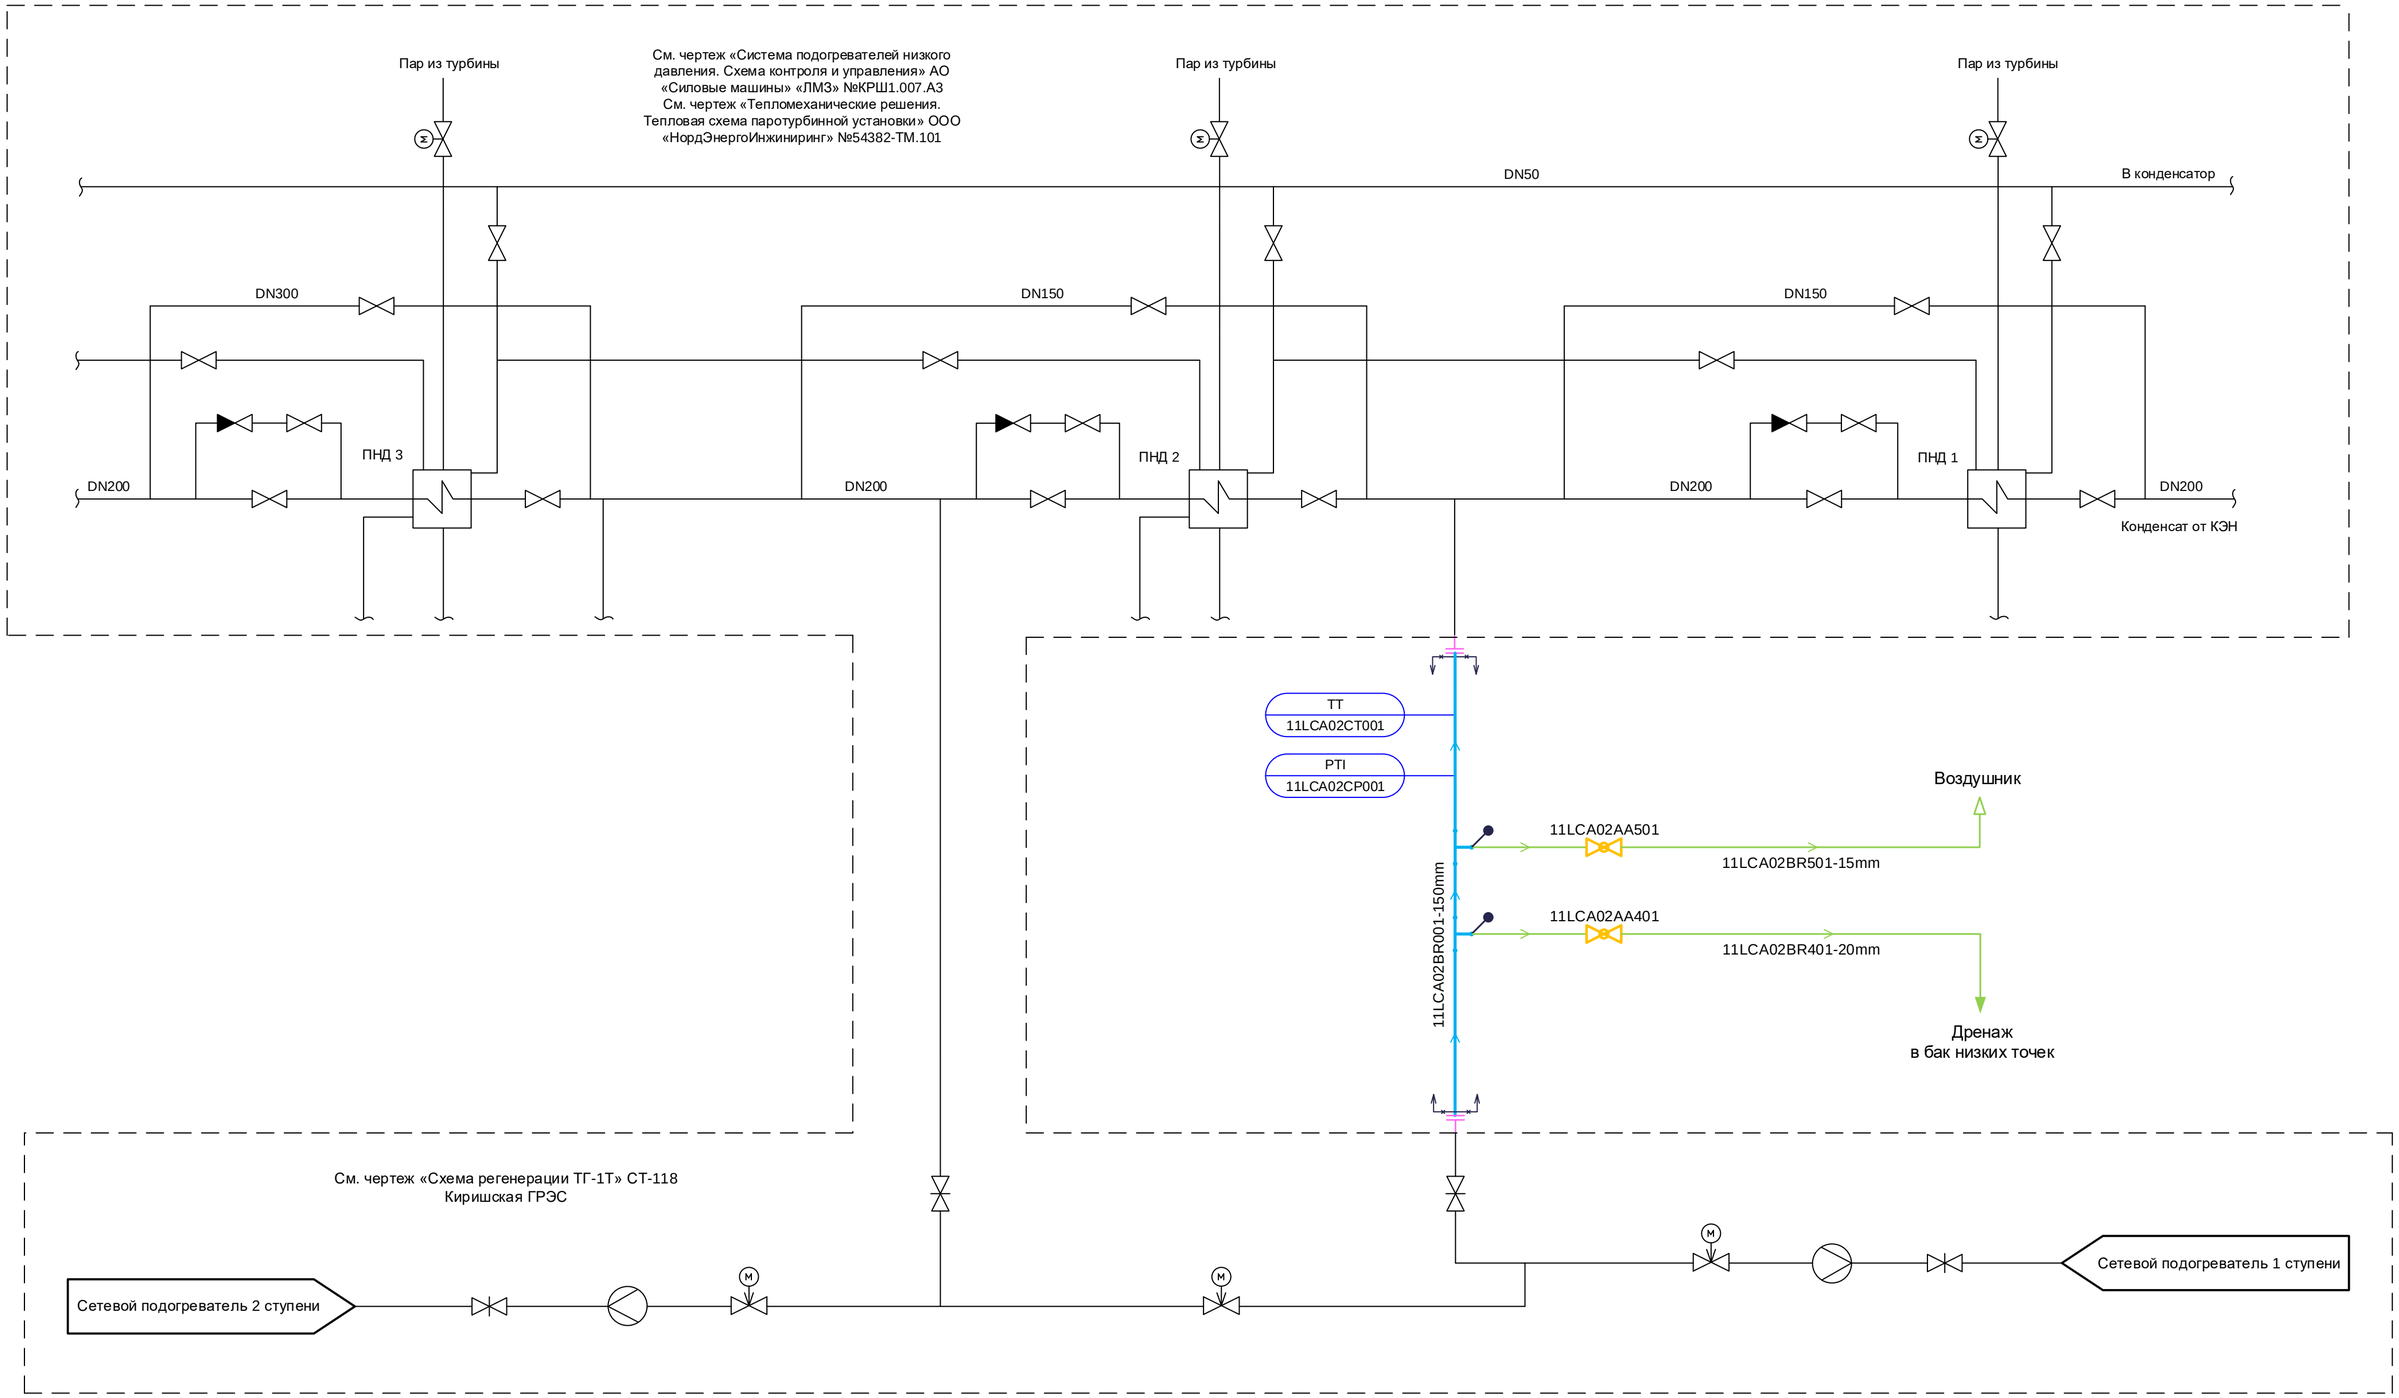

2	-	Зам	588-21		08.21	181M1D – 13UHJ – 5244 – TD.M
Изм.	Кол.уч	Лист	№ док.	Подп.	Дата	Модернизация генерирующего объекта Киришская ГРЭС (Г-1т)
Разработал		Дадыко				Главный корпус. PI-диаграмма трубопроводов подачи основного конденсата от сетевых подогревателей 1 и 2 ступеней и КНД в систему регенерации НД
Проверил		Супонина				Стадия: Р; Лист: 2; Листов:
Н. контр.		Астраханцев				PI-диаграмма трубопроводов подачи основного конденсата от сетевых подогревателей 1 и 2 ступеней и КНД в систему регенерации НД. Система LCA

АКЦИОНЕРНОЕ ОБЩЕСТВО ИНСТИТУТ ТЕПЛОЭЛЕКТРОПРОЕКТ г. МОСКВА

Согласовано
ОАСУ Соболева

Взам. инв. №
Подпись и дата
Инв. № подл.

Формат А2