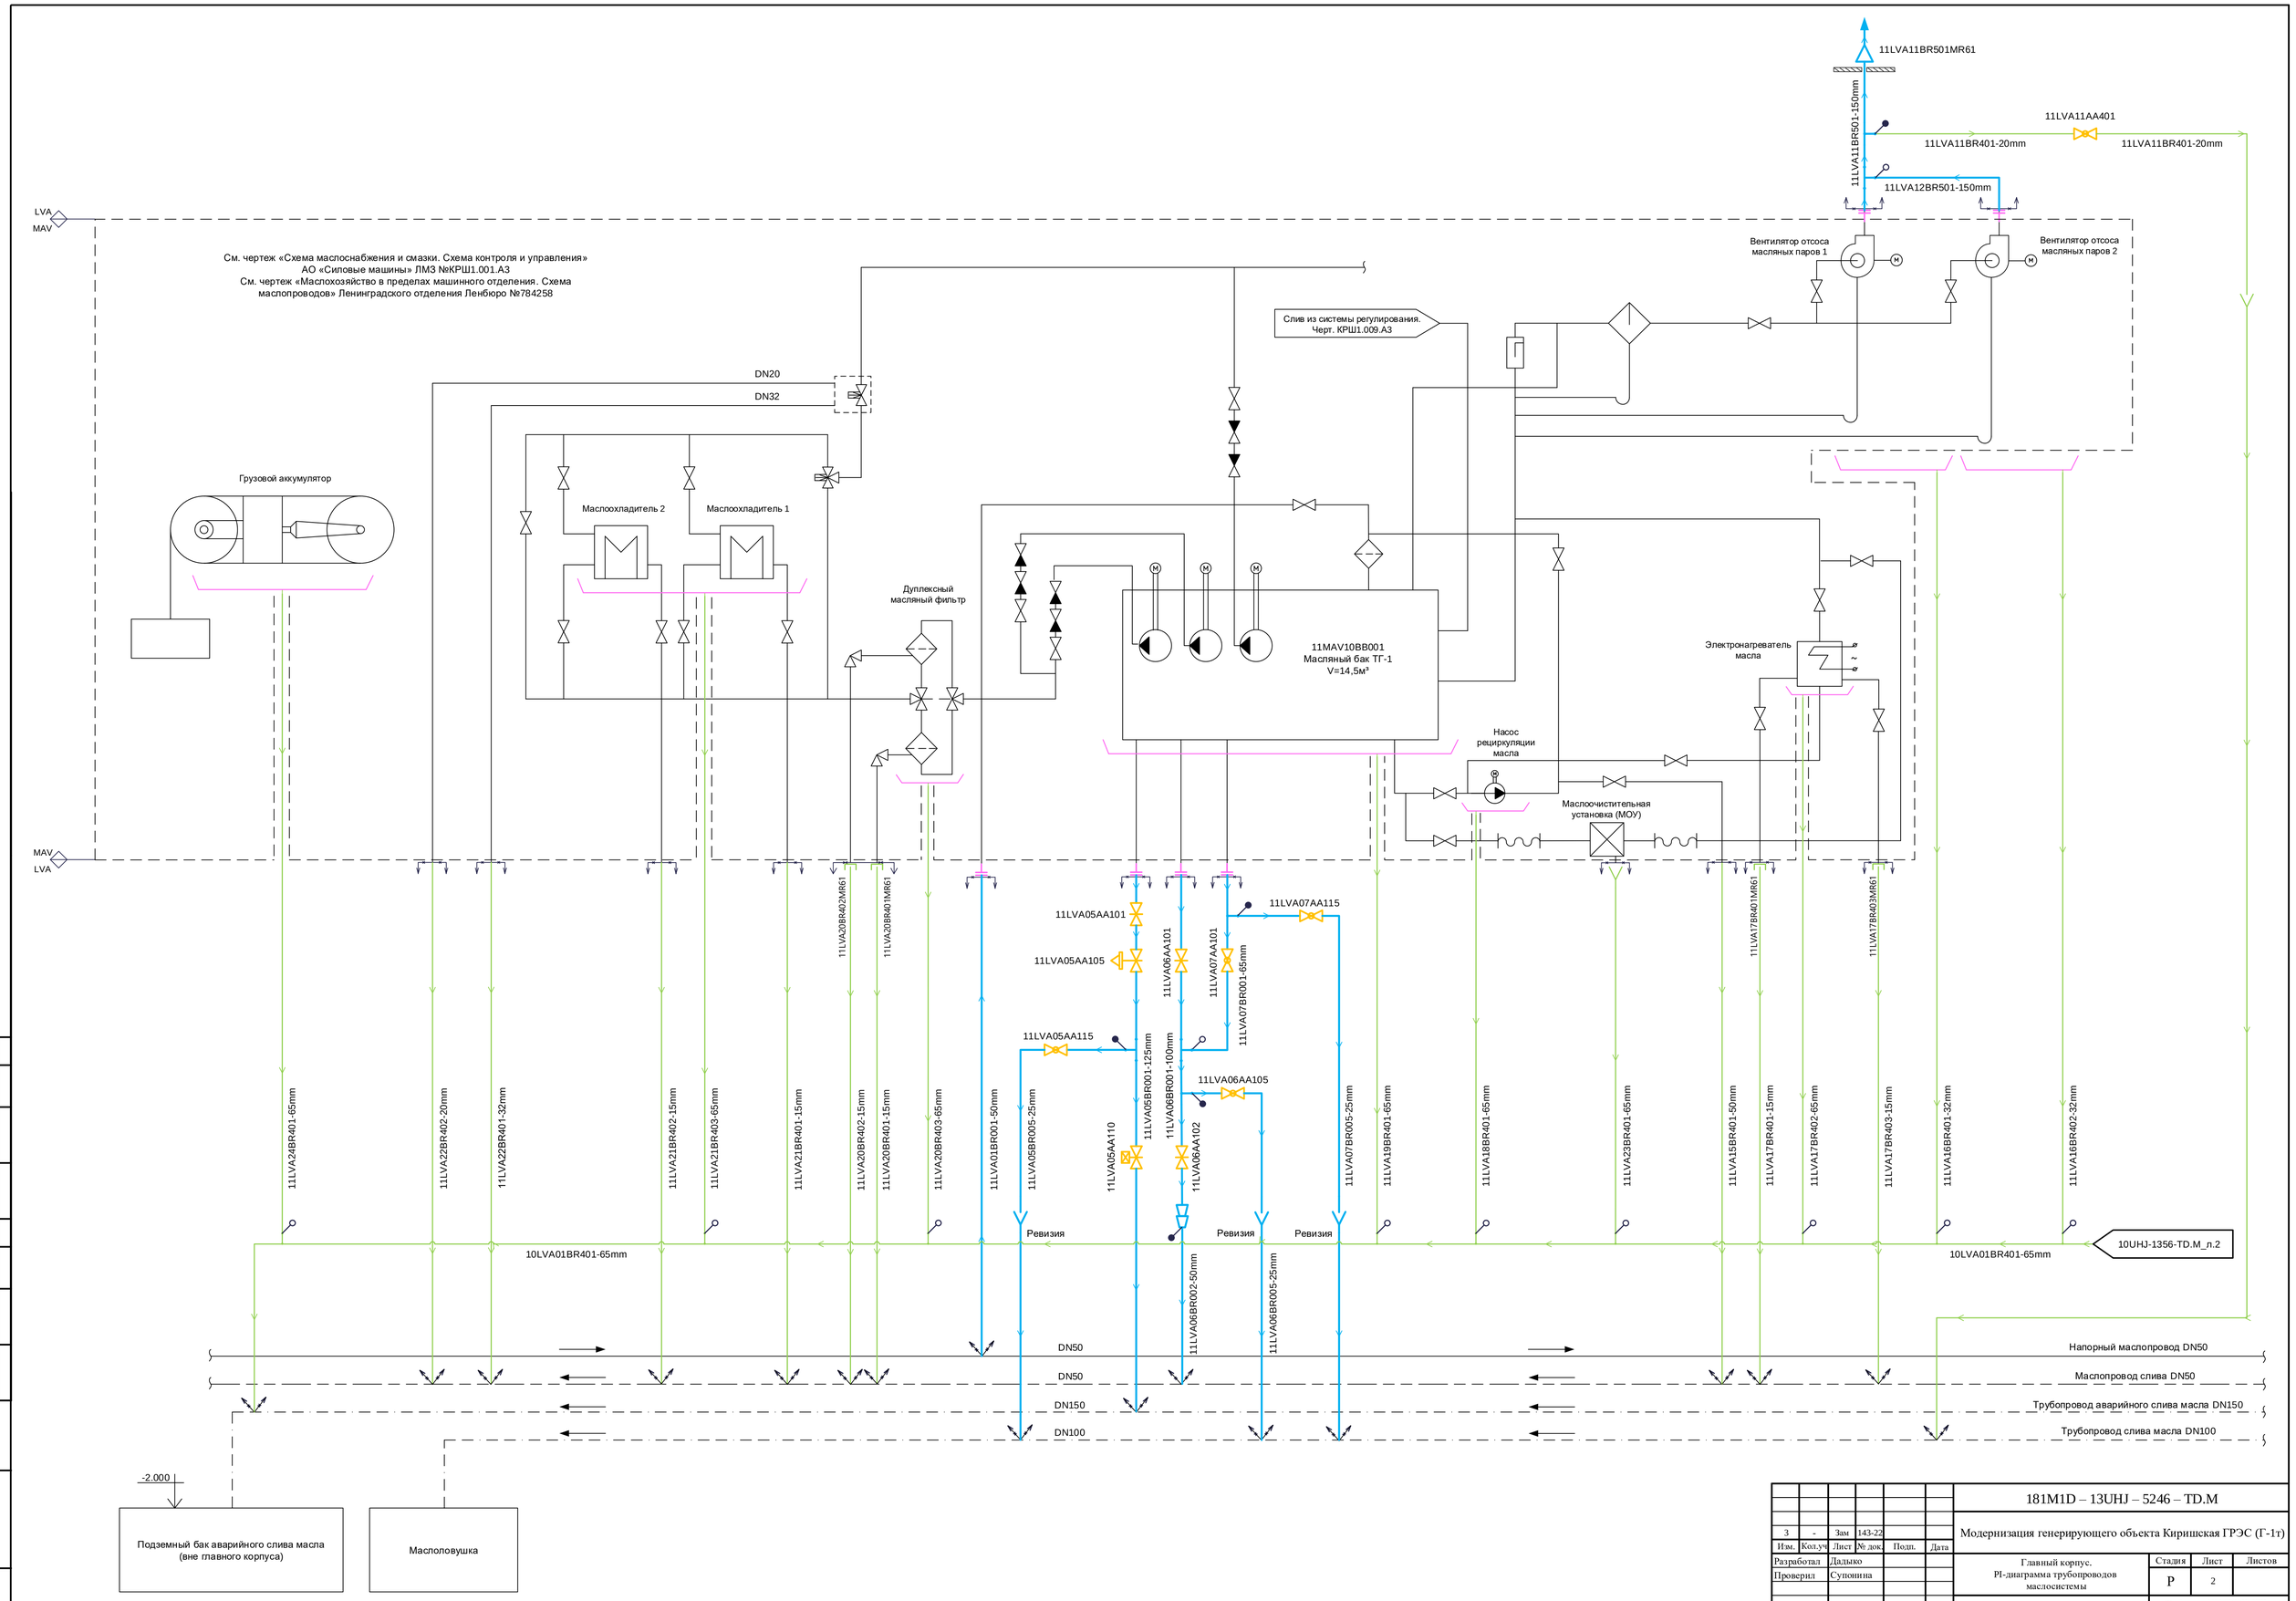

3	-	Зам	143-22			
Изм.	Кол.уч	Лист	№ док.	Подп.	Дата	
Разработал		Дадыко				
Проверил		Супонина				
Н. контр.		Астраханцев				

181M1D – 13UHJ – 5246 – TD.M

Модернизация генерирующего объекта Киришская ГРЭС (Г-1т)

Главный корпус.
PI-диаграмма трубопроводов
маслосистемы

Стадия	Лист	Листов
Р	2	

PI-диаграмма трубопроводов
маслосистемы. Система LVA

АКЦИОНЕРНОЕ ОБЩЕСТВО ИНСТИТУТ ТЕПЛОЭЛЕКТРОПРОЕКТ г. МОСКВА

Согласовано

Взам. инв. №

Подпись и дата

Инв. № подл.

Формат А1