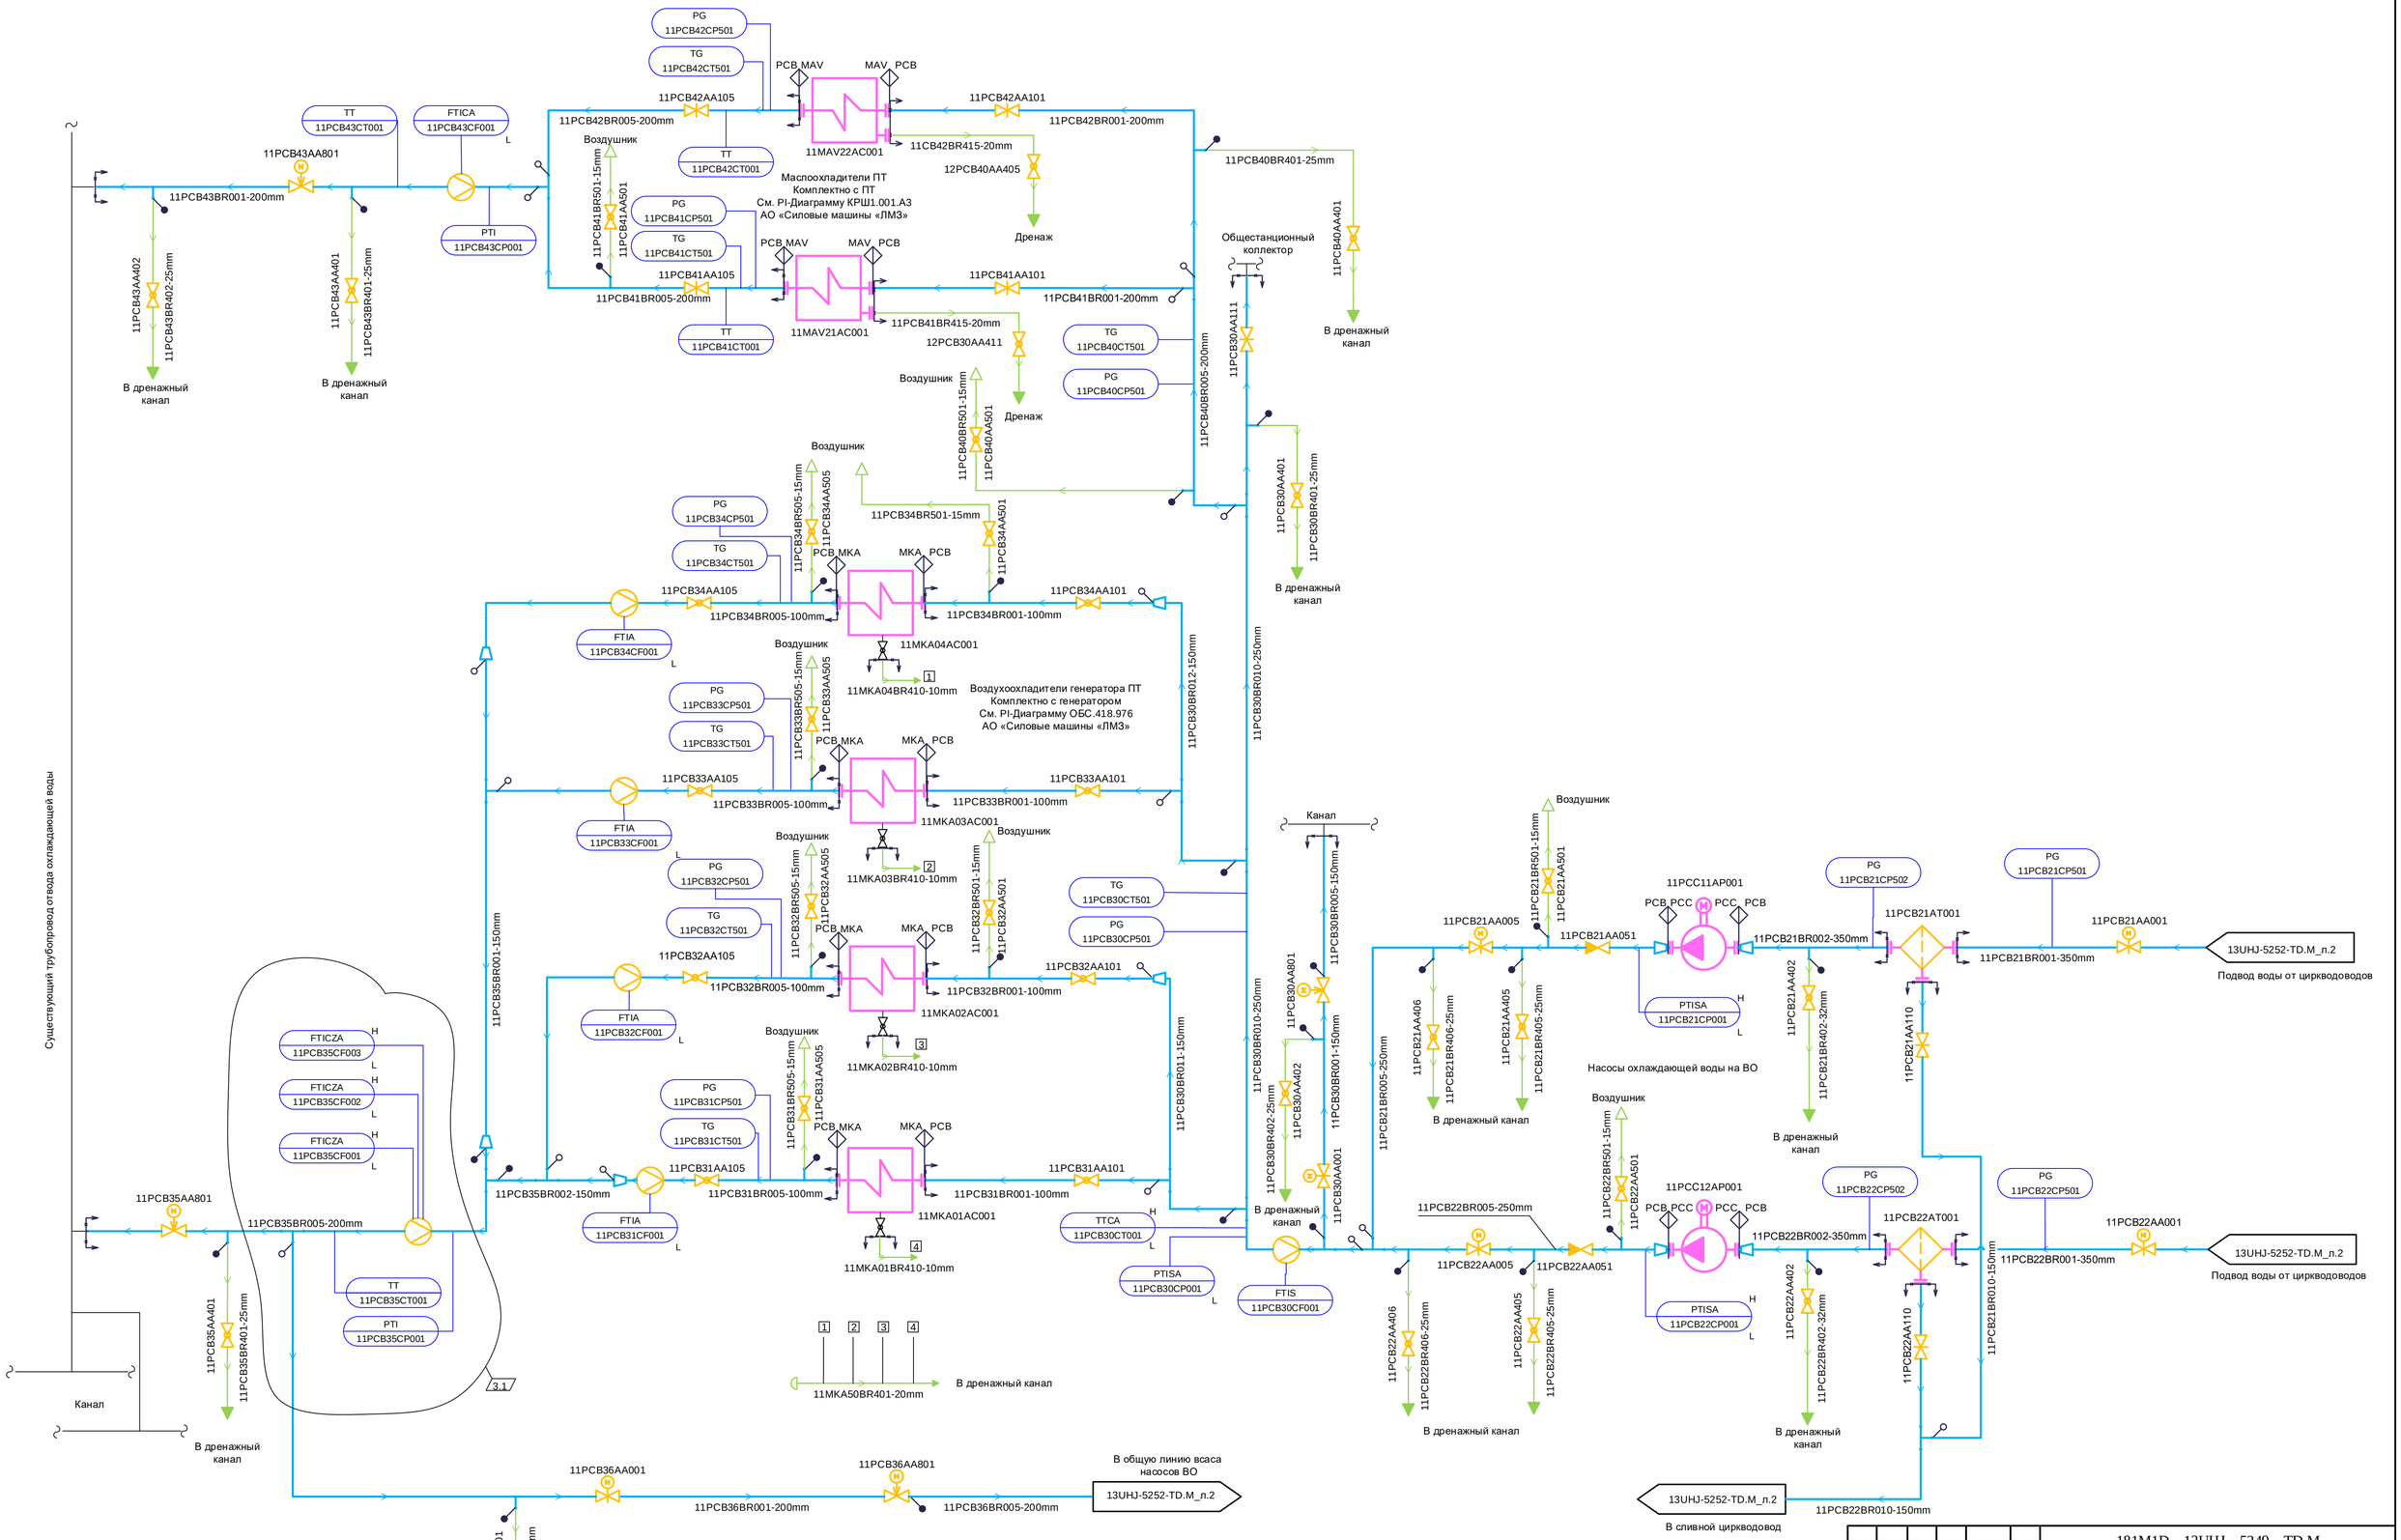

3	1	Изм.	966-23		06.23	181M1D – 13UHJ – 5249 – TD.M	
Изм.	Кол.уч	Лист	№ док.	Подп.	Дата	Модернизация генерирующего объекта Киришская ГРЭС (Г-1т)	
Разработал		Дёмина				Главный корпус. PI-диаграмма охлаждающей воды вспомогательного оборудования турбоагрегата	Стадия: Р; Лист: 2; Листов:
Проверил		Супонина					
Н. контр.		Астраханцев				PI-диаграмма охлаждающей воды вспомогательного оборудования турбоагрегата. Система PCB, PCC	Акционерное общество Институт Теплоэлектропроект г. Москва

Согласовано
ОАСУ
Соболева
Взам. инв. №
Подпись и дата
Инв. № подл.

Формат А1