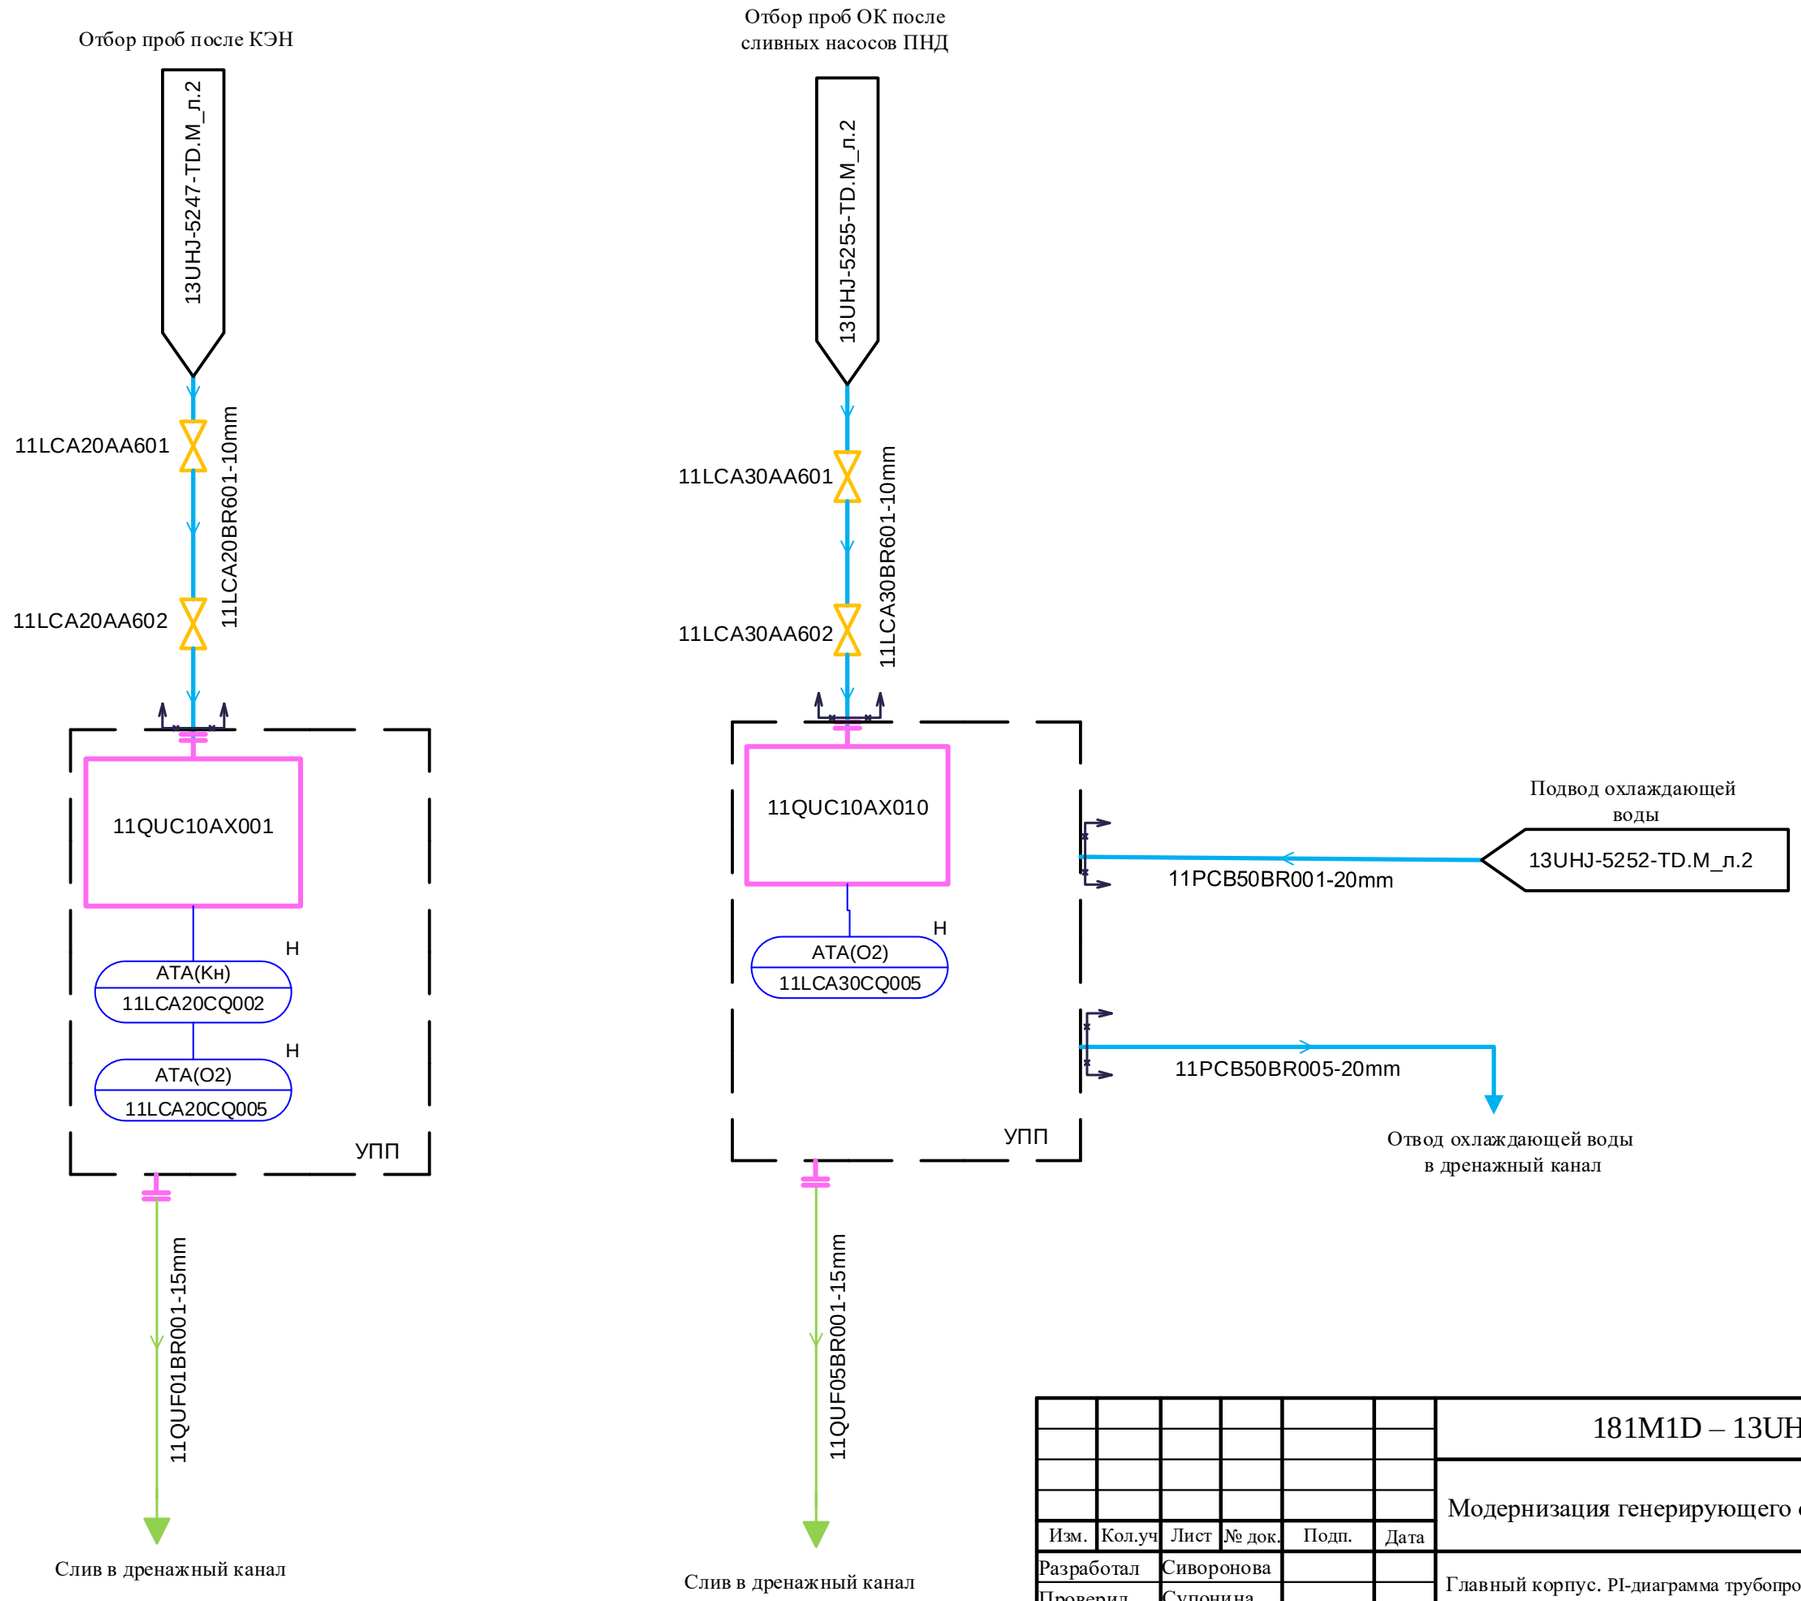

Согласовано

Соболева

ОАСУ

Взам. инв. №

Подпись и дата

Инв. № подл.

Изм.	Кол.уч	Лист	№ док.	Подп.	Дата
Разработал		Сиворонова			
Проверил		Супонина			
Н. контр.		Астраханцев			

181M1D – 13UHJ – 5251 – TD.M

Модернизация генерирующего объекта Киришская ГРЭС (Г-1т)

Главный корпус. PI-диаграмма трубопроводов отборов проб основного конденсата.

Стадия	Лист	Листов
Р	2	

PI-диаграмма трубопроводов отборов проб основного конденсата . Система LCA, QUC, QUF.

АКЦИОНЕРНОЕ ОБЩЕСТВО ИНСТИТУТ ТЕПЛОЭЛЕКТРОПРОЕКТ Г. МОСКВА

Формат А3