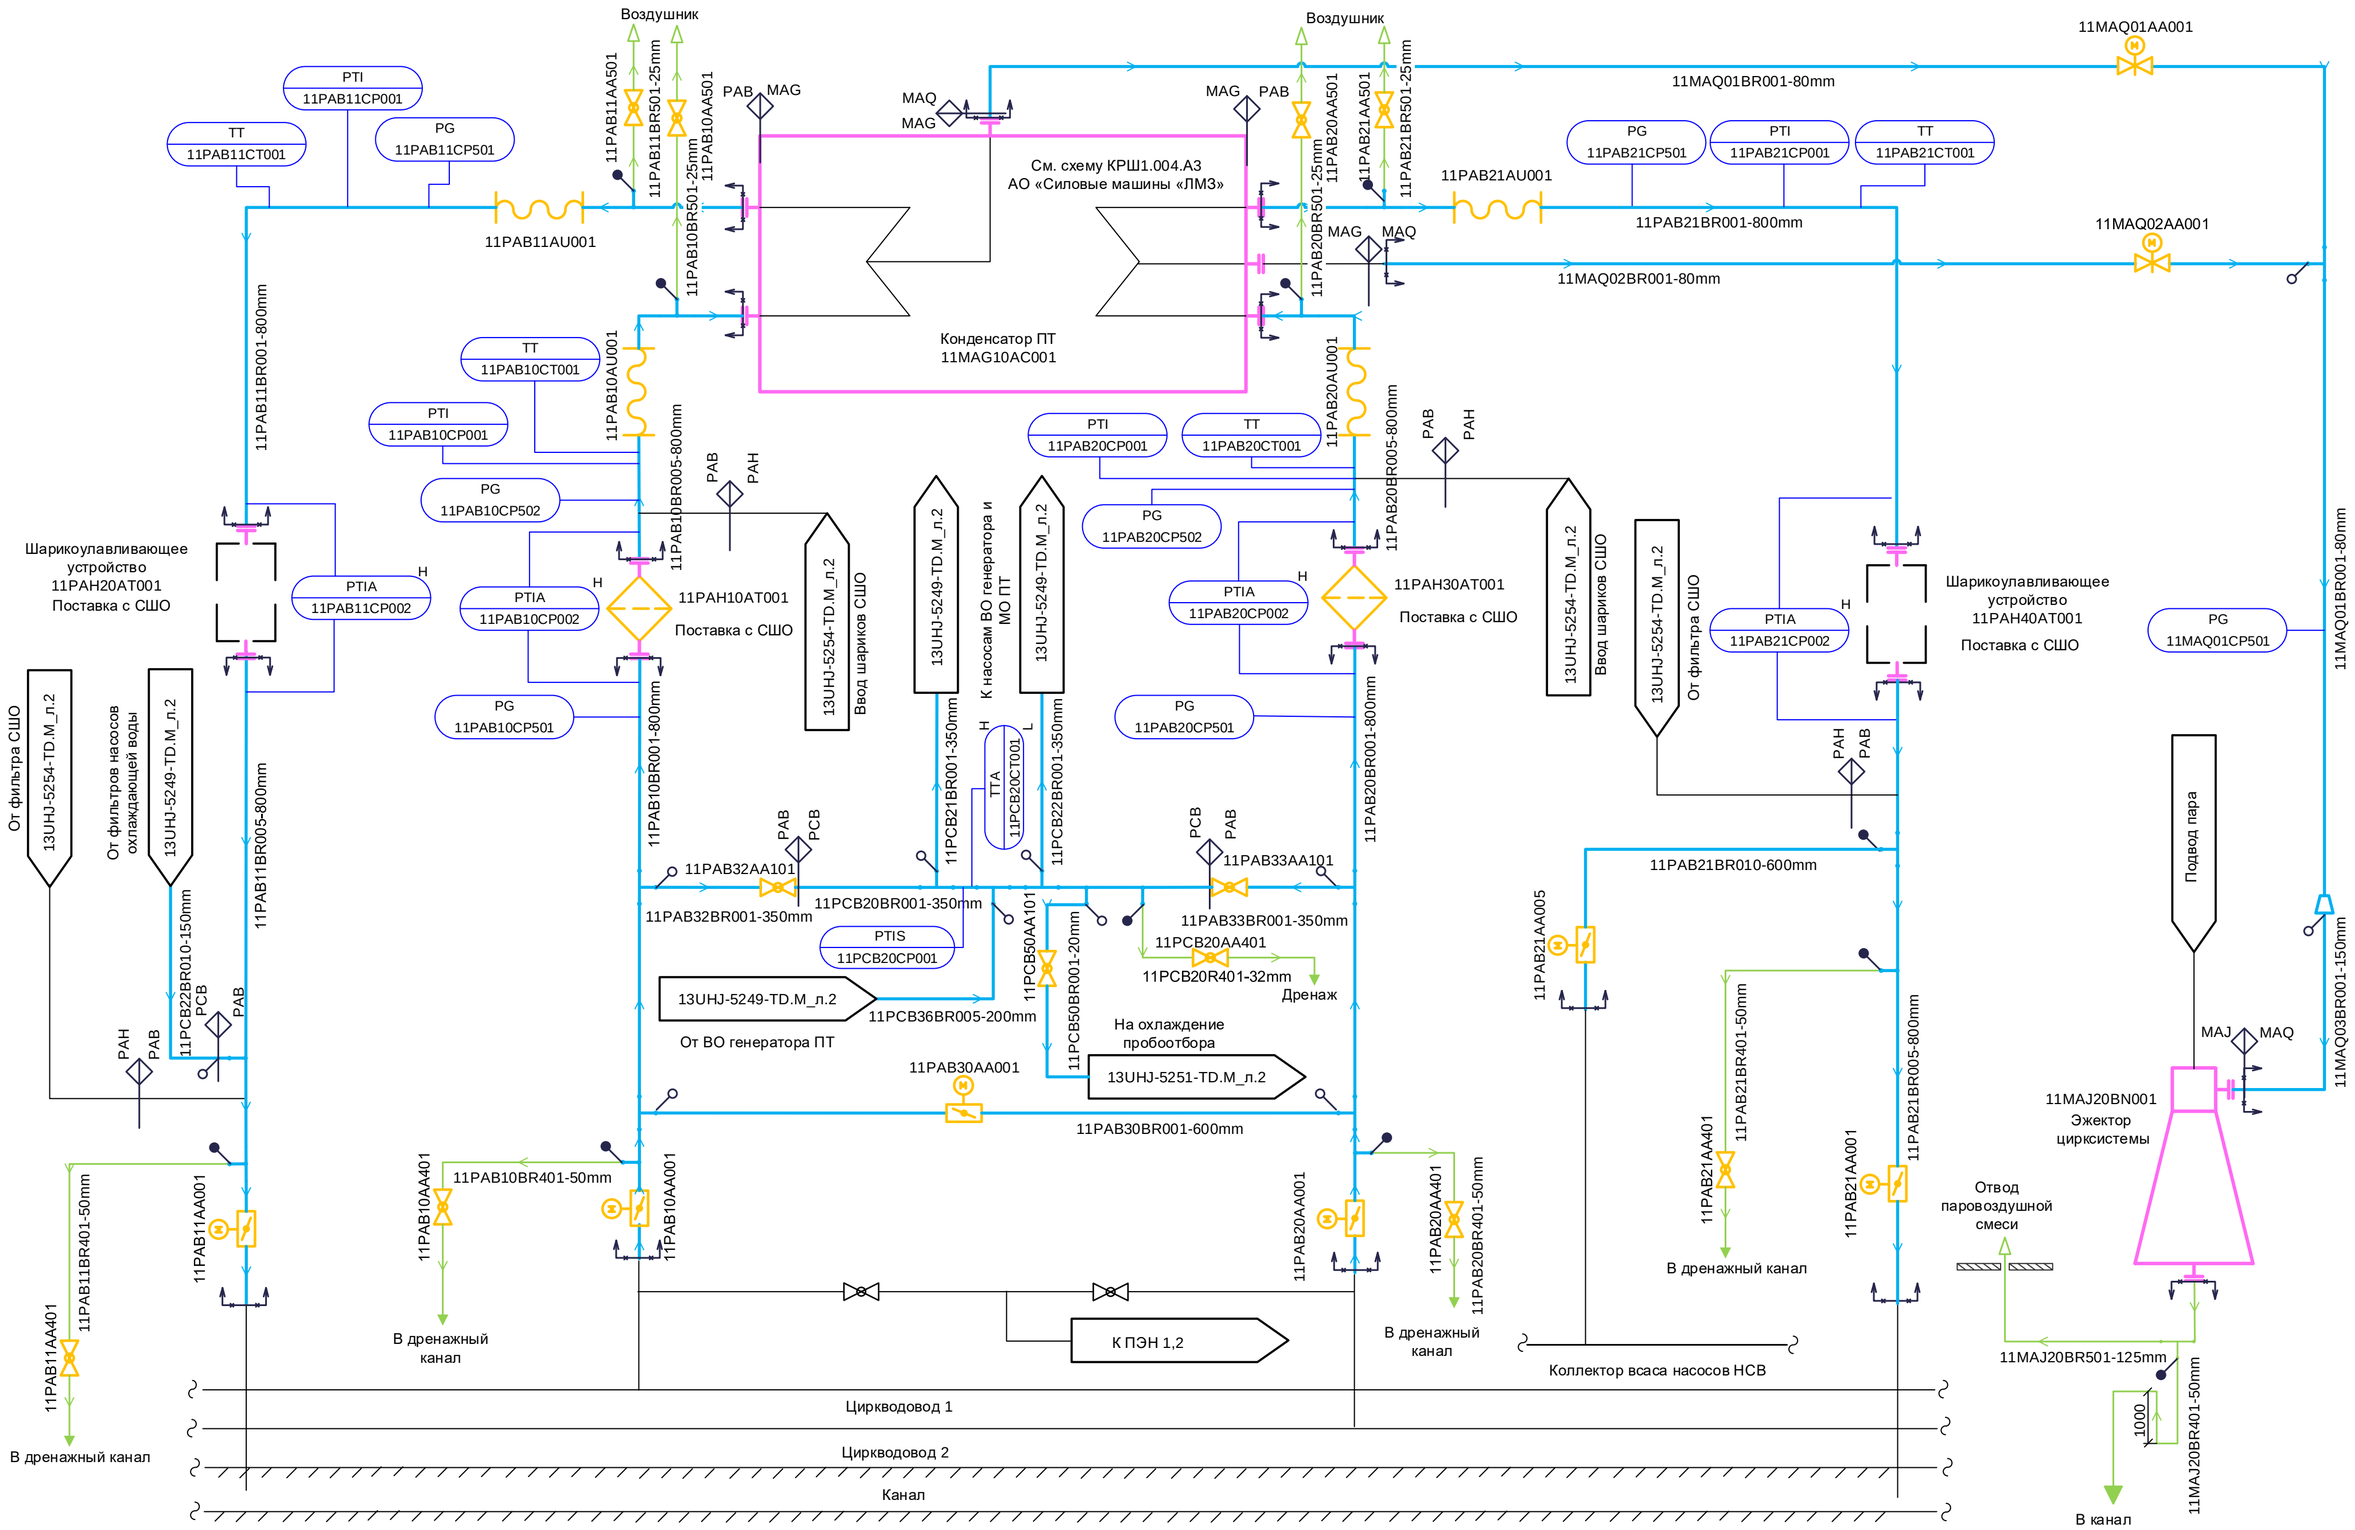

Примечание: Система шариковой очистки конденсатора см. PI-Диаграмму 13UHJ-5254-TD.M

1	-	Зам.	524-21		06.21	181M1D – 13UHJ – 5252 – TD.M
Изм.	Кол.уч	Лист	№ док.	Подп.	Дата	Модернизация генерирующего объекта Киришская ГРЭС (Г-1т)
Разработал		Дёмина				Главный корпус. PI-диаграмма трубопроводов охлаждающей воды конденсатора турбоагрегата
Проверил		Супонина				Стадия: Р; Лист: 2; Листов:
Н. контр.		Астраханцев				PI-диаграмма трубопроводов охлаждающей воды конденсатора турбоагрегата. Система PAB

АКЦИОНЕРНОЕ ОБЩЕСТВО ИНСТИТУТ ТЕПЛОЭЛЕКТРОПРОЕКТ Г. МОСКВА

Согласовано: ОАСУ Соболева

Инв. № подл.

Формат А2