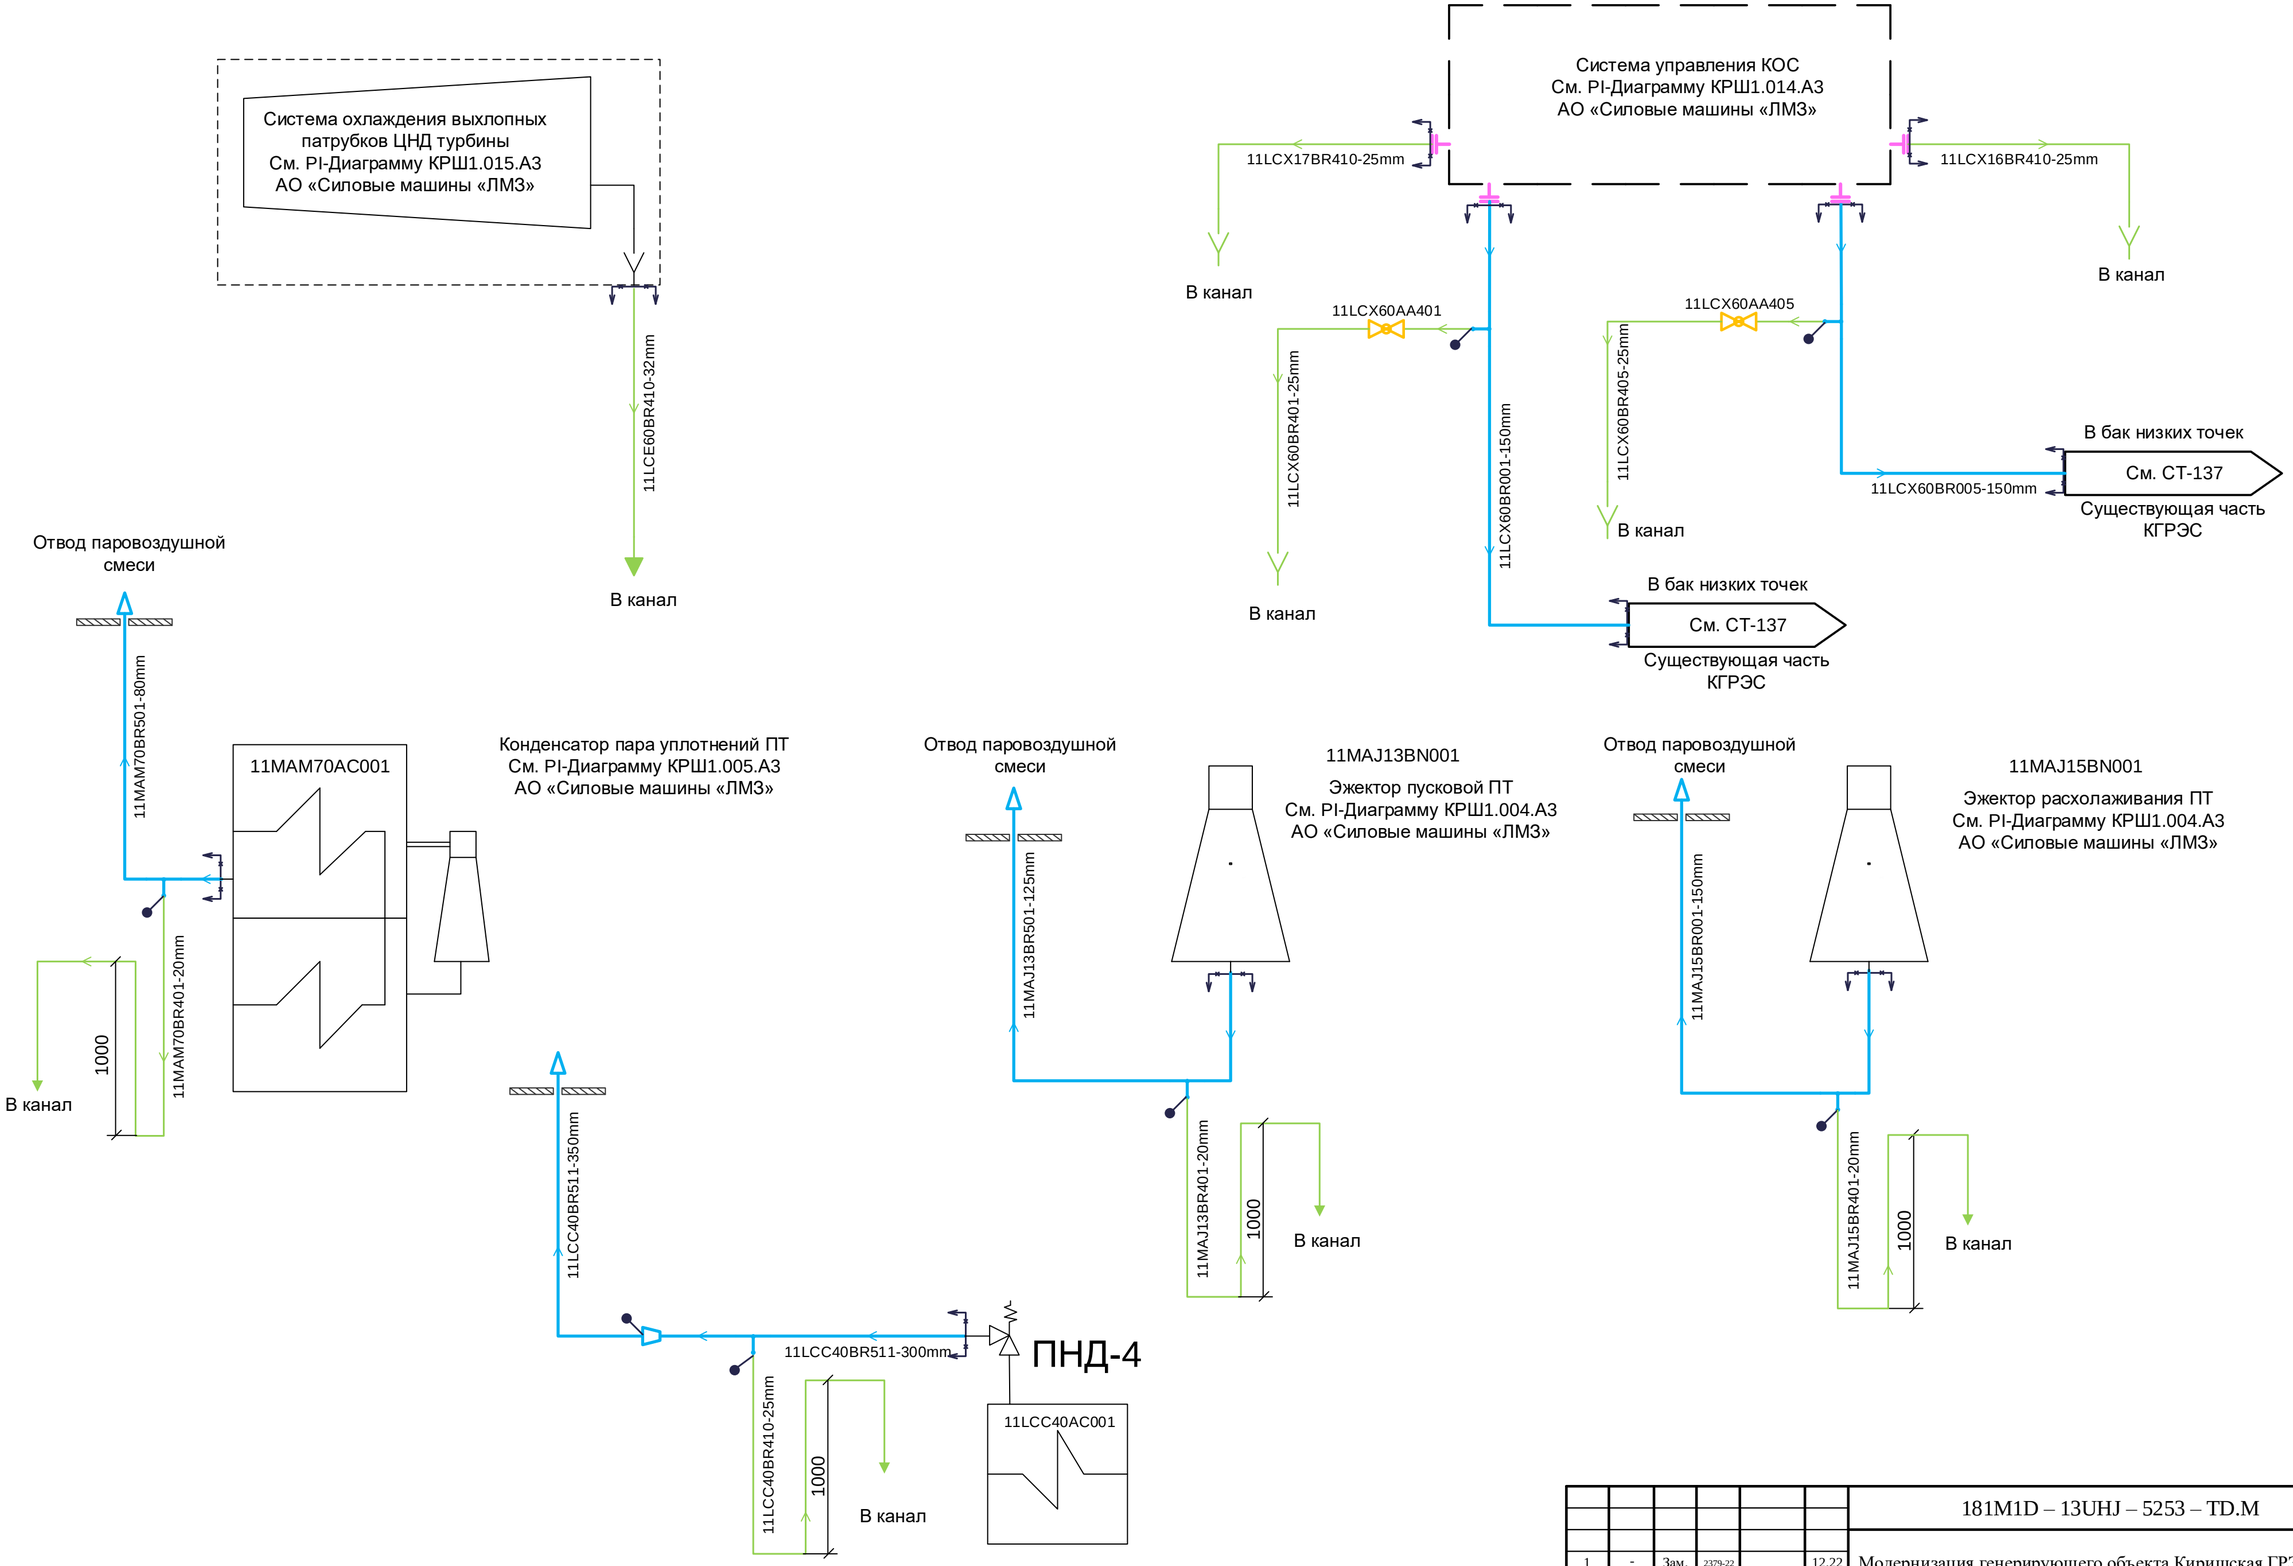

1	-	Зам.	2379-22		12.22	181M1D – 13UHJ – 5253 – TD.M
Изм.	Кол.уч	Лист	№ док.	Подп.	Дата	Модернизация генерирующего объекта Киришская ГРЭС (Г-1т)
Разработал		Гусев.Т				Главный корпус. PI-диаграмма дренажей, воздушников и вспомогательных трубопроводов турбоагрегата
Проверил		Супонина				Стадия: Р; Лист: 2; Листов:
Н. контр.		Астраханцев				PI-диаграмма дренажей, воздушников и вспомогательных трубопроводов турбоагрегата

АКЦИОНЕРНОЕ ОБЩЕСТВО ИНСТИТУТ ТЕПЛОЭЛЕКТРОПРОЕКТ Г. МОСКВА

Согласовано: ОДСУ Соболева

Взам. инв. № | Подпись и дата | Инв. № подл.

Формат А2