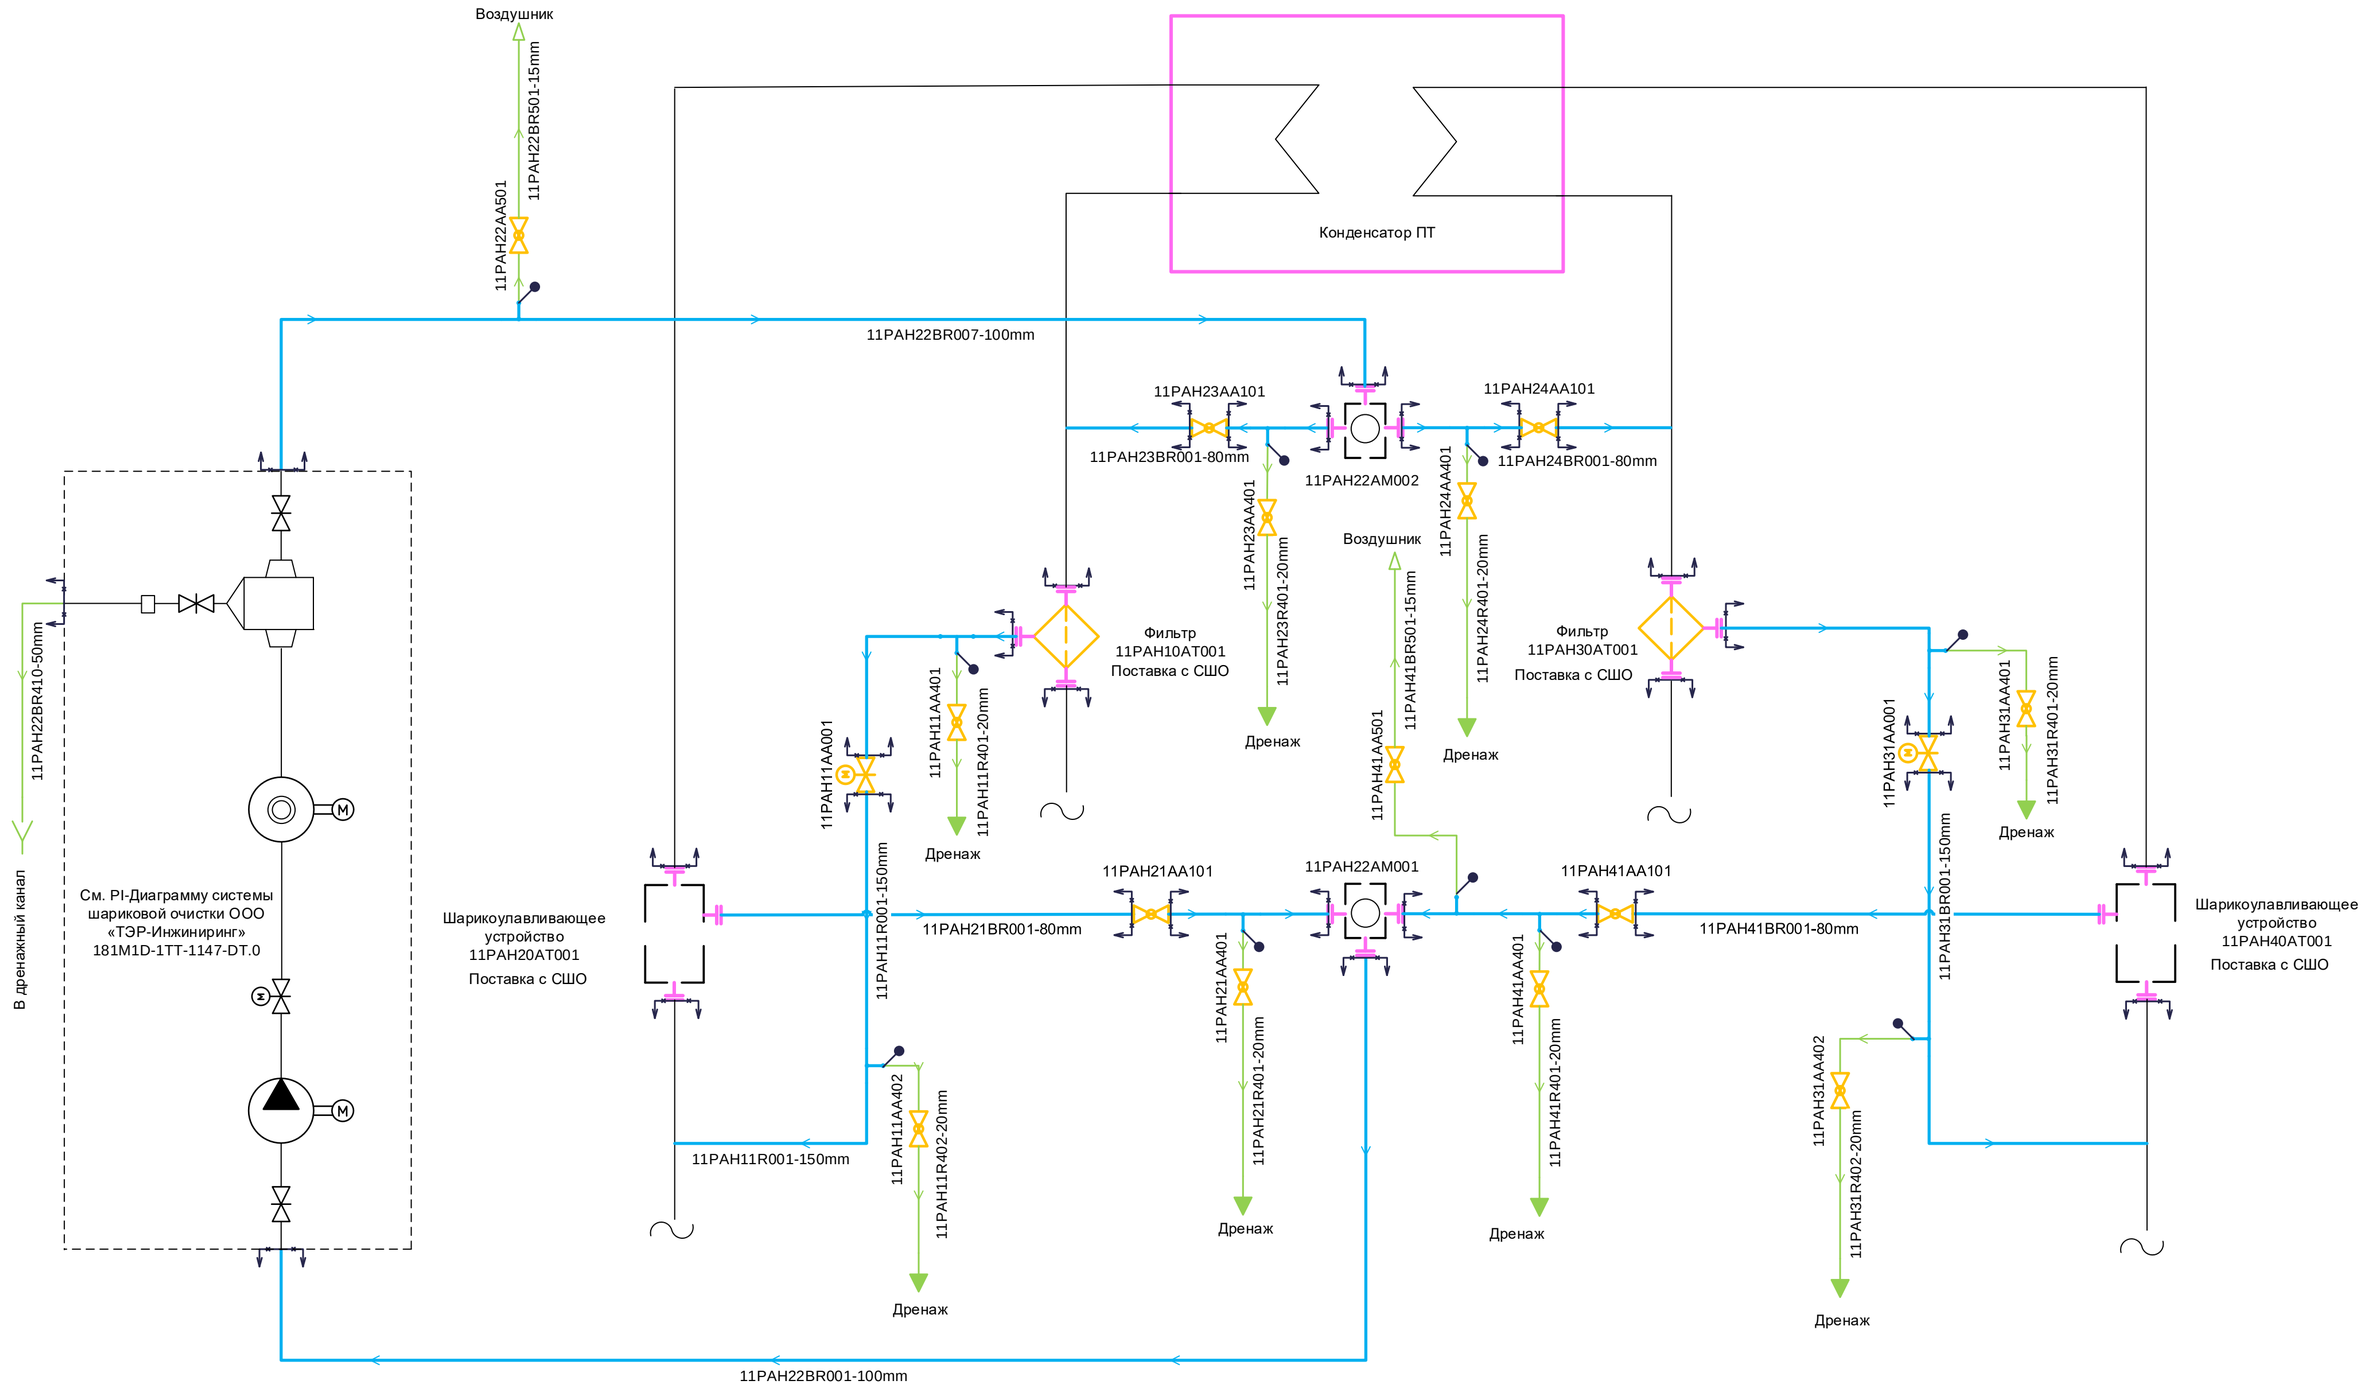

Примечание: 1. Основные трубопроводы охлаждения конденсатора турбины см. PI-Диаграмму13UHJ-5252-TD.M

2. Установка шариковой очистки конденсатора турбины См. PI-Диаграмму ООО «ТЭР-Инжиниринг»181M1D-2TT-2147-DT.0O

1	-	Зам.	588-21		08.21	
Изм.	Кол.уч	Лист	№ док.	Подп.	Дата	
Разработал		Дёмина				
Проверил		Супонина				
Н. контр.		Астраханцев				

181M1D – 13UHJ – 5254 – TD.M

Модернизация генерирующего объекта Киришская ГРЭС (Г-1т)

Главный корпус. PI-диаграмма трубопроводов системы шариковой очистки конденсатора турбоагрегата

Стадия	Лист	Листов
Р	2	

PI-диаграмма трубопроводов системы шариковой очистки конденсатора турбоагрегата. Система PAH

АКЦИОНЕРНОЕ ОБЩЕСТВО ИНСТИТУТ ТЕПЛОЭЛЕКТРОПРОЕКТ Г. МОСКВА

Формат А2

Согласовано

ОАСУ Соболева

Взам. инв. №

Подпись и дата

Инв. № подл.