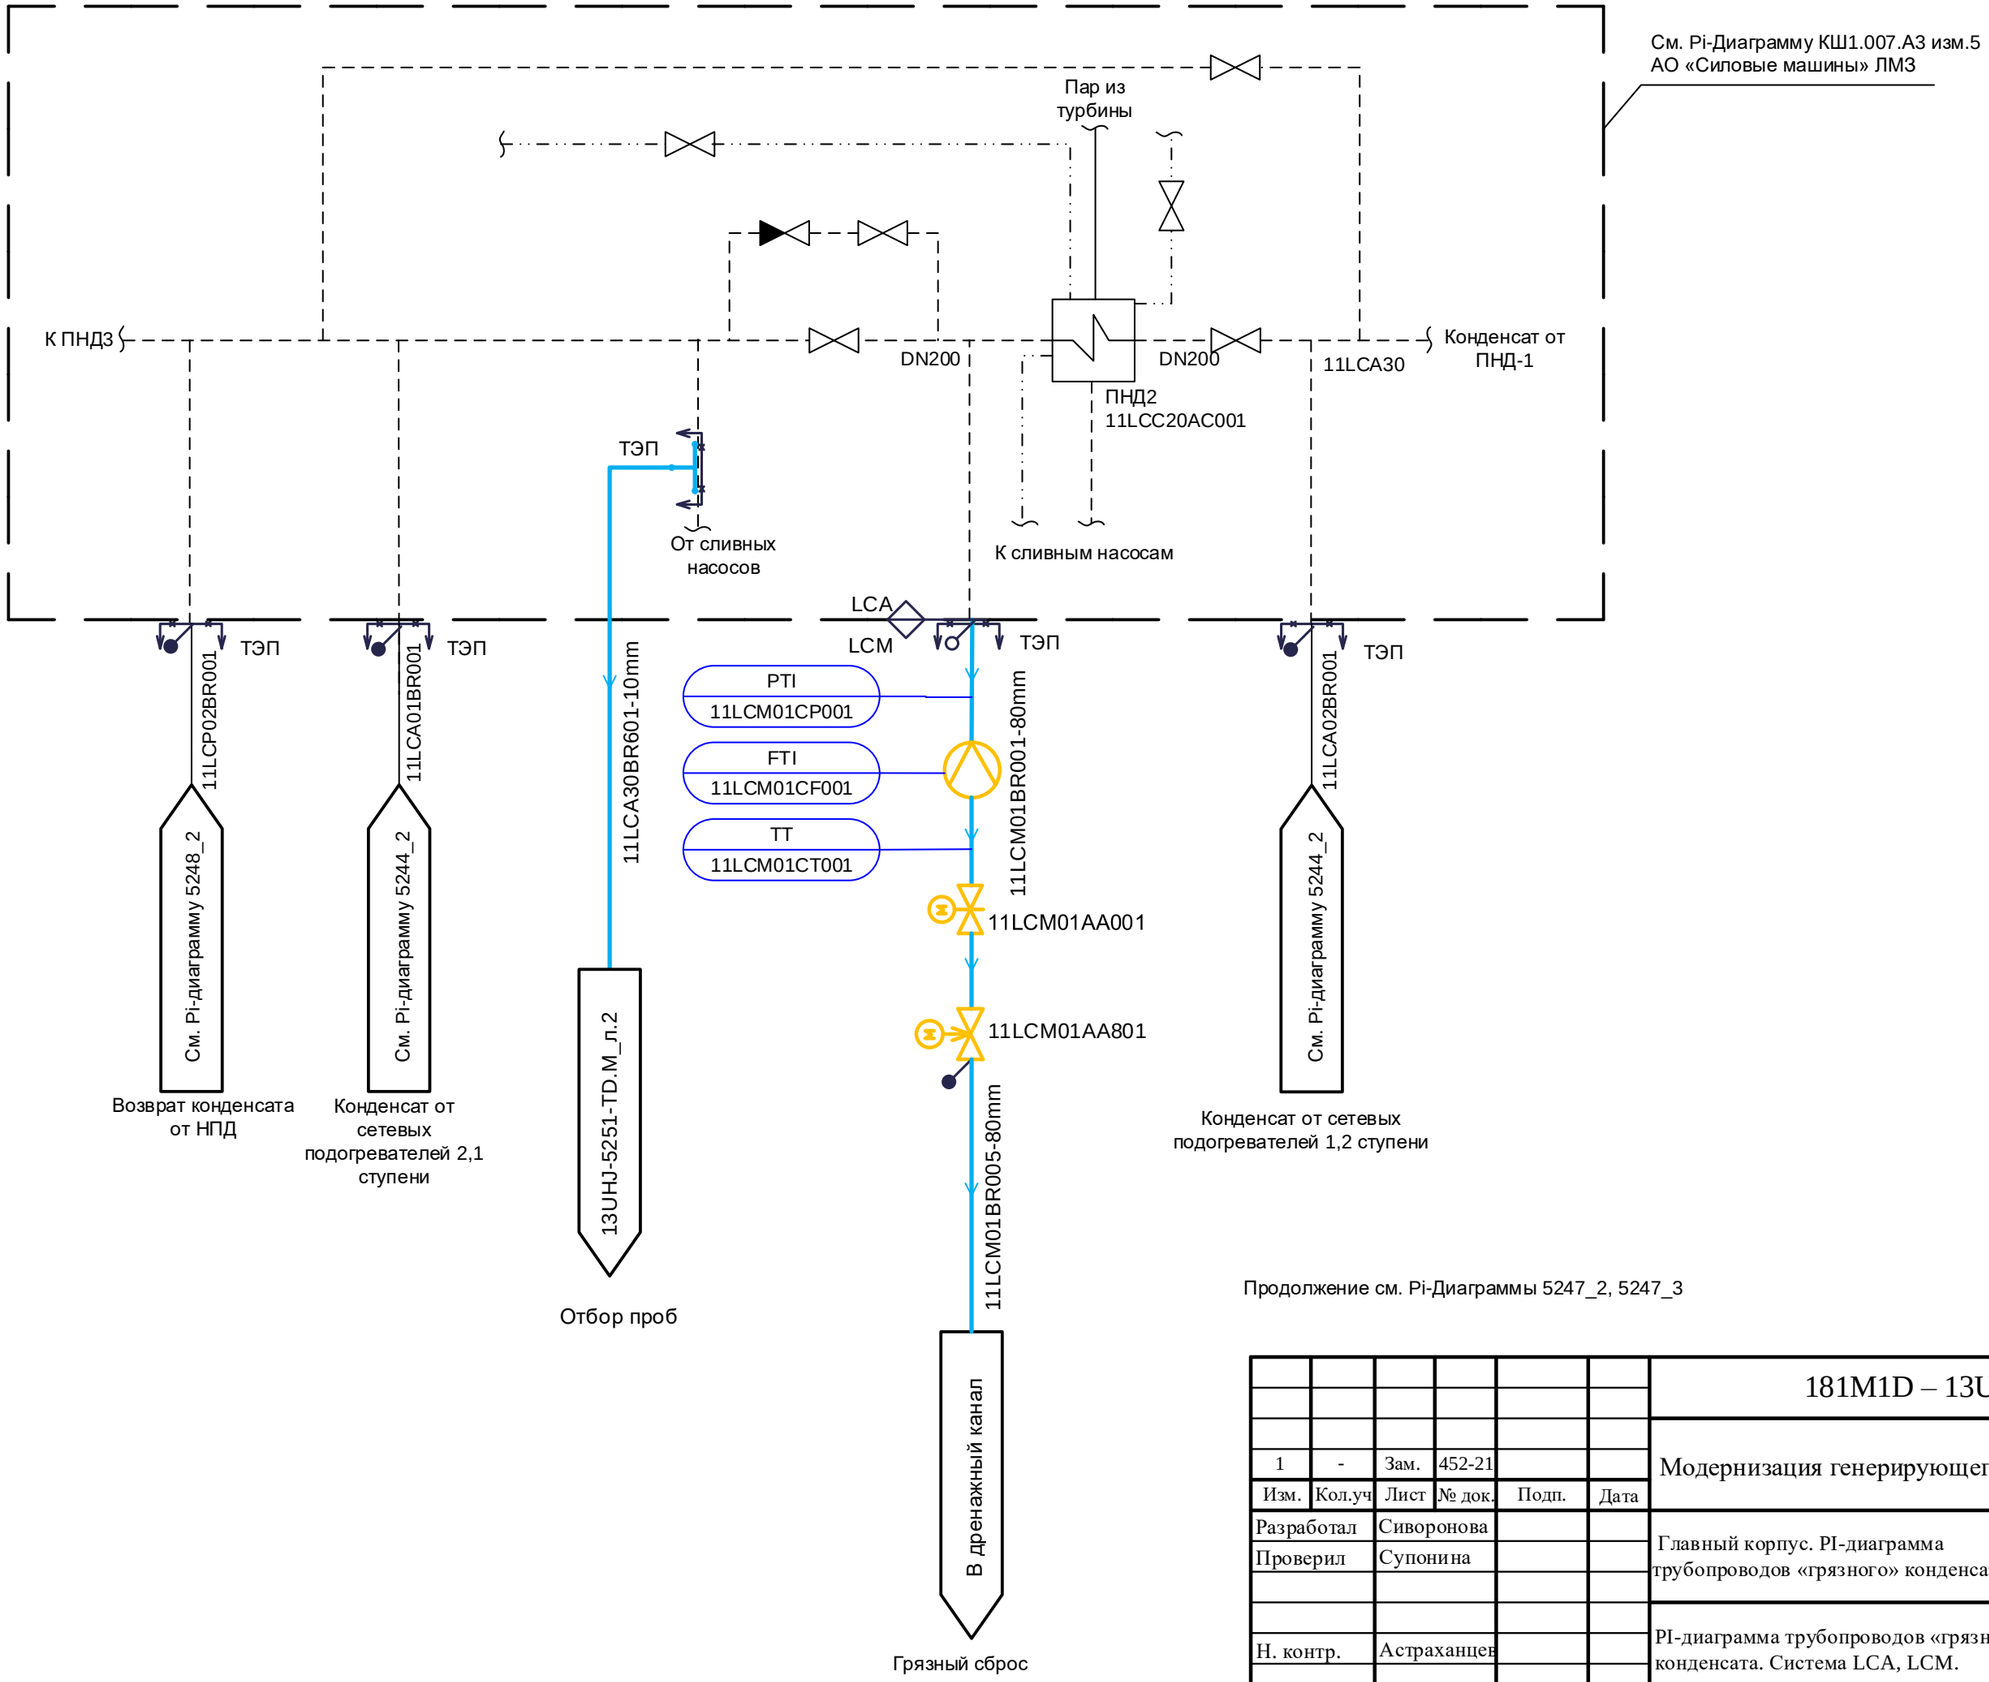

Согласовано

Соболева

ОАСУ

Взам. инв. №

Подпись и дата

Инв. № подл.

1	-	Зам.	452-21			
Изм.	Кол.уч	Лист	№ док.	Подп.	Дата	
Разработал		Сиворонова				
Проверил		Супонина				
Н. контр.		Астраханцев				

181M1D – 13UHJ – 5255 – TD.M

Модернизация генерирующего объекта Киришская ГРЭС (Г-1т)

Главный корпус. PI-диаграмма трубопроводов «грязного» конденсата

Стадия	Лист	Листов
Р	2	

PI-диаграмма трубопроводов «грязного» конденсата. Система LCA, LCM.

АКЦИОНЕРНОЕ ОБЩЕСТВО ИНСТИТУТ ТЕПЛОЭЛЕКТРОПРОЕКТ Г. МОСКВА

Формат А3