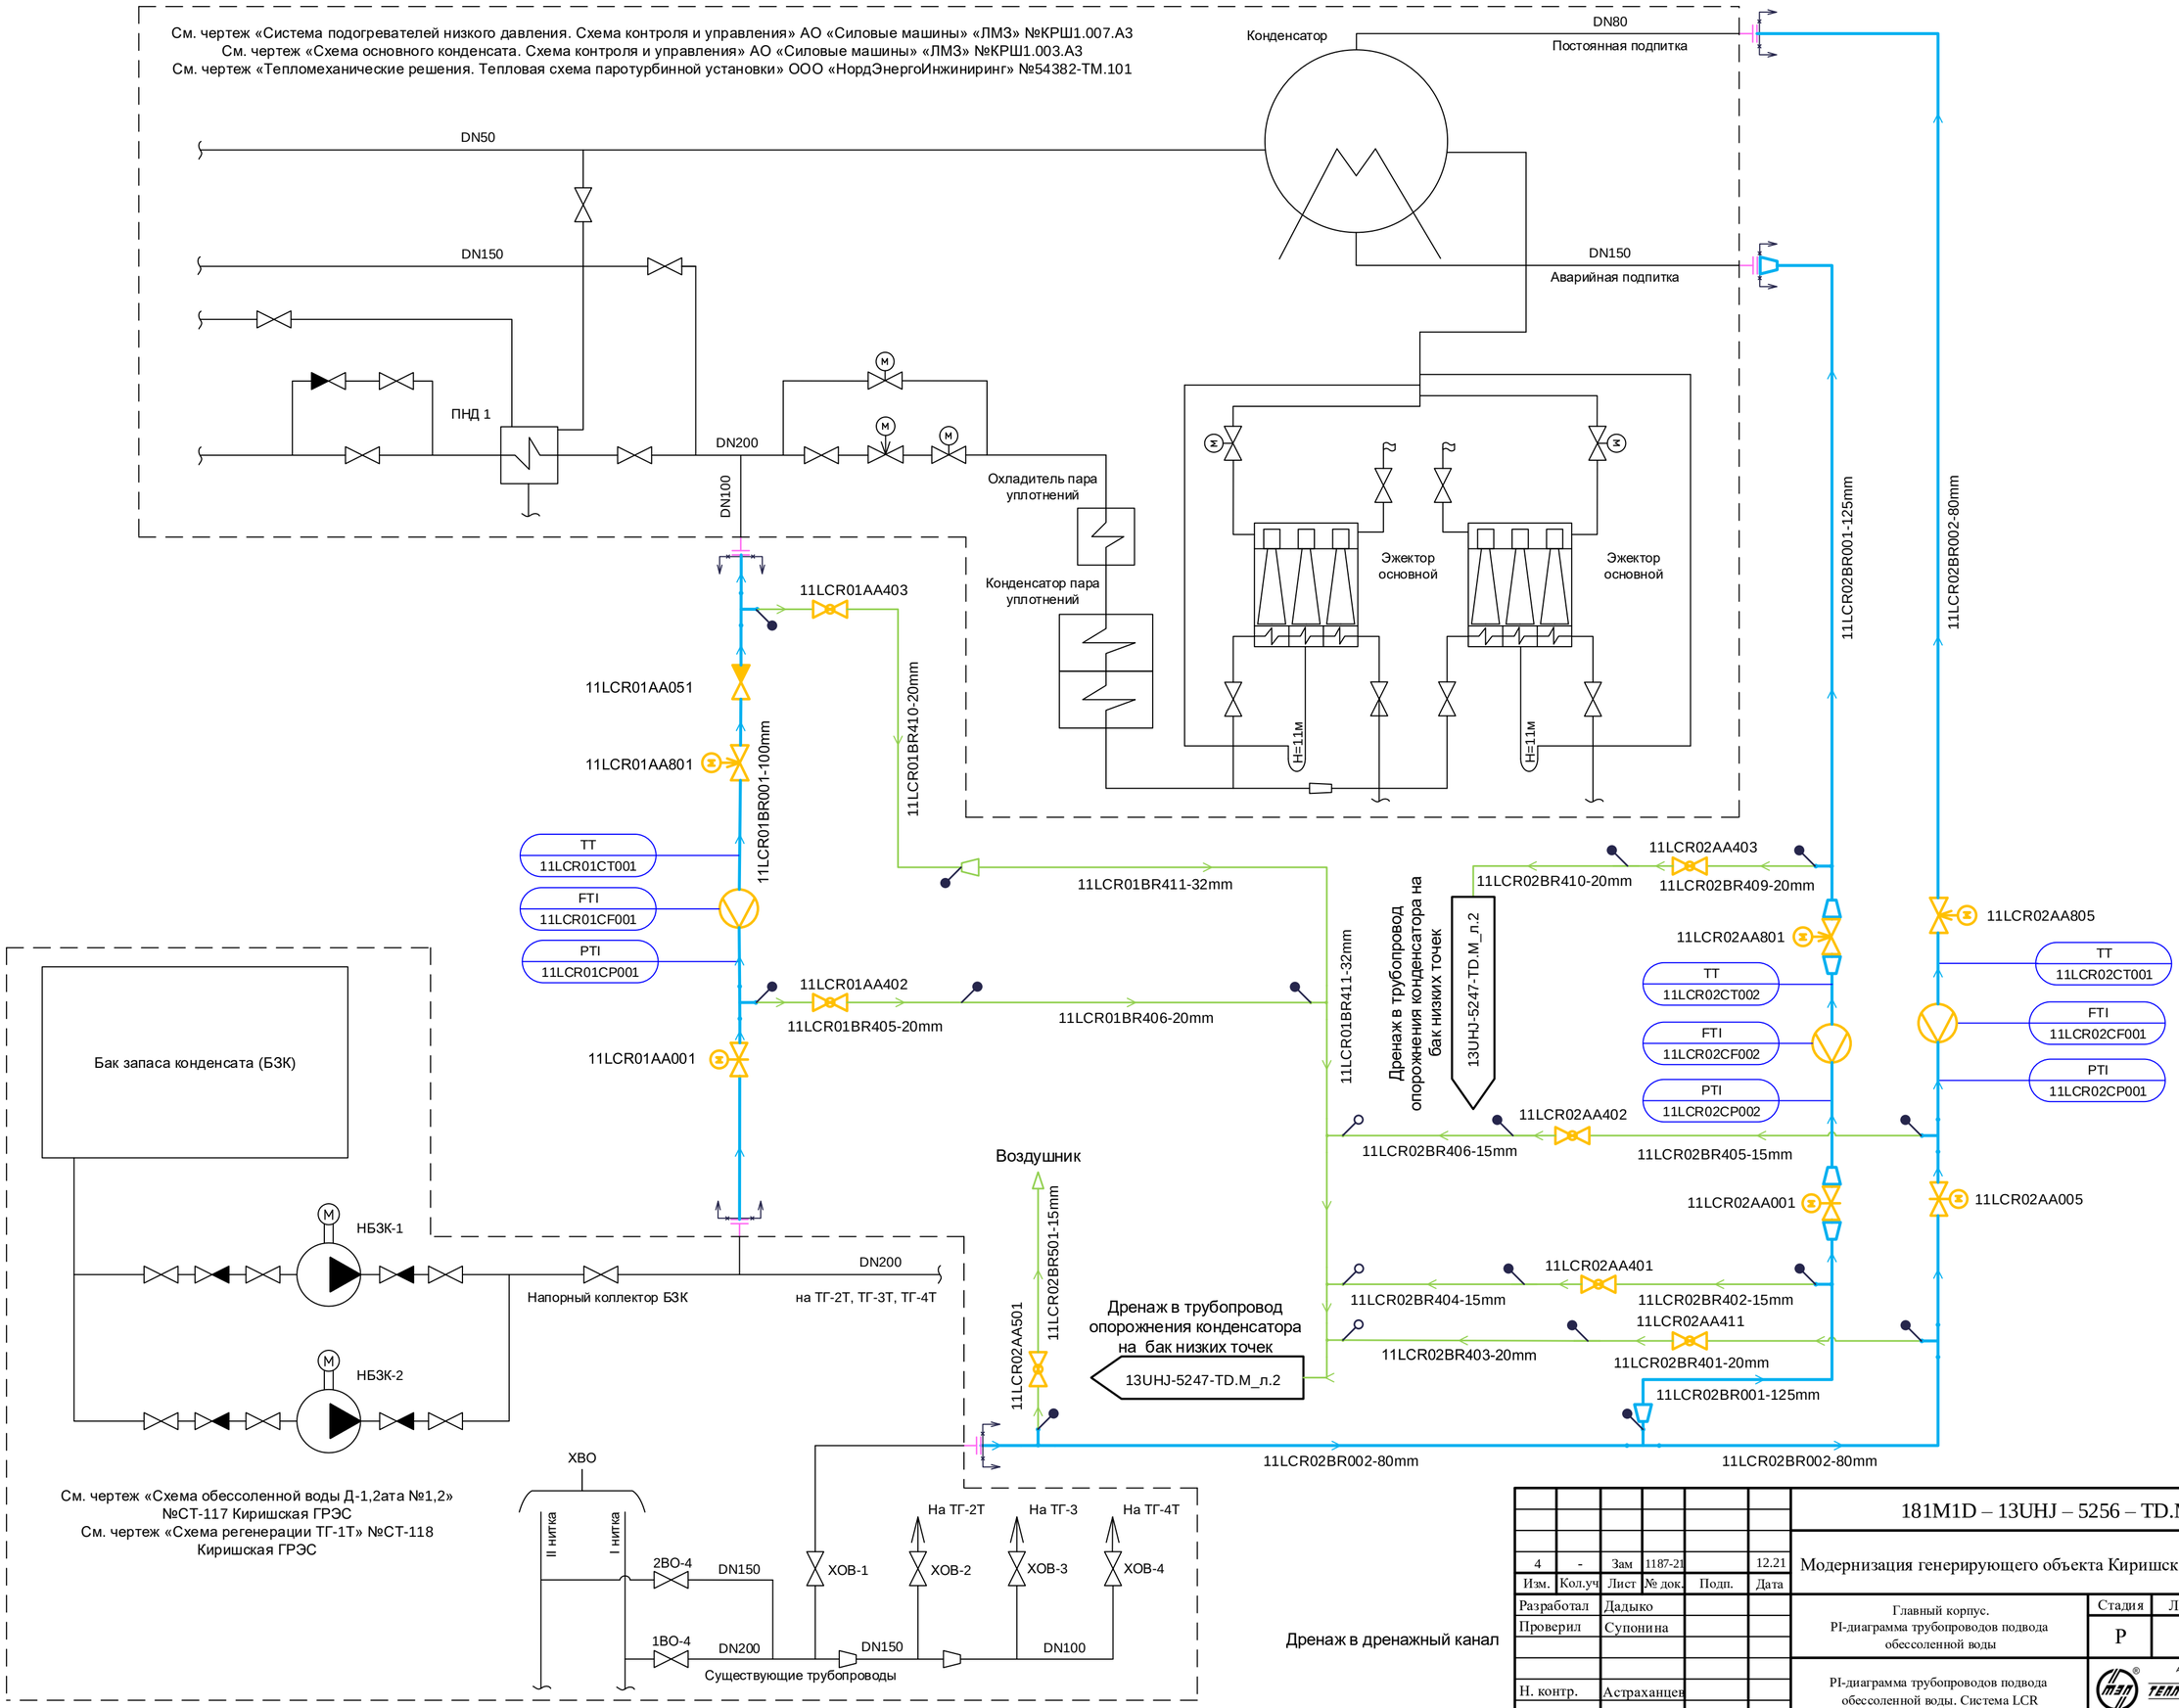

Изм.	Кол.уч	Лист	№ док.	Подп.	Дата
4	-	Зам	1187-21		12.21
Разработал		Дадыко			
Проверил		Супонина			
Н. контр.		Астраханцев			

181M1D – 13UHJ – 5256 – TD.M

Модернизация генерирующего объекта Киришская ГРЭС (Г-1т)

Главный корпус. PI-диаграмма трубопроводов подвода обессоленной воды

Стадия	Лист	Листов
Р	2	

PI-диаграмма трубопроводов подвода обессоленной воды. Система LCR

АКЦИОНЕРНОЕ ОБЩЕСТВО ИНСТИТУТ ТЕПЛОЭЛЕКТРОПРОЕКТ Г. МОСКВА

Согласовано
ОАСУ Соболева
Взам. инв. №
Подпись и дата
Инв. № подл.

Формат А2