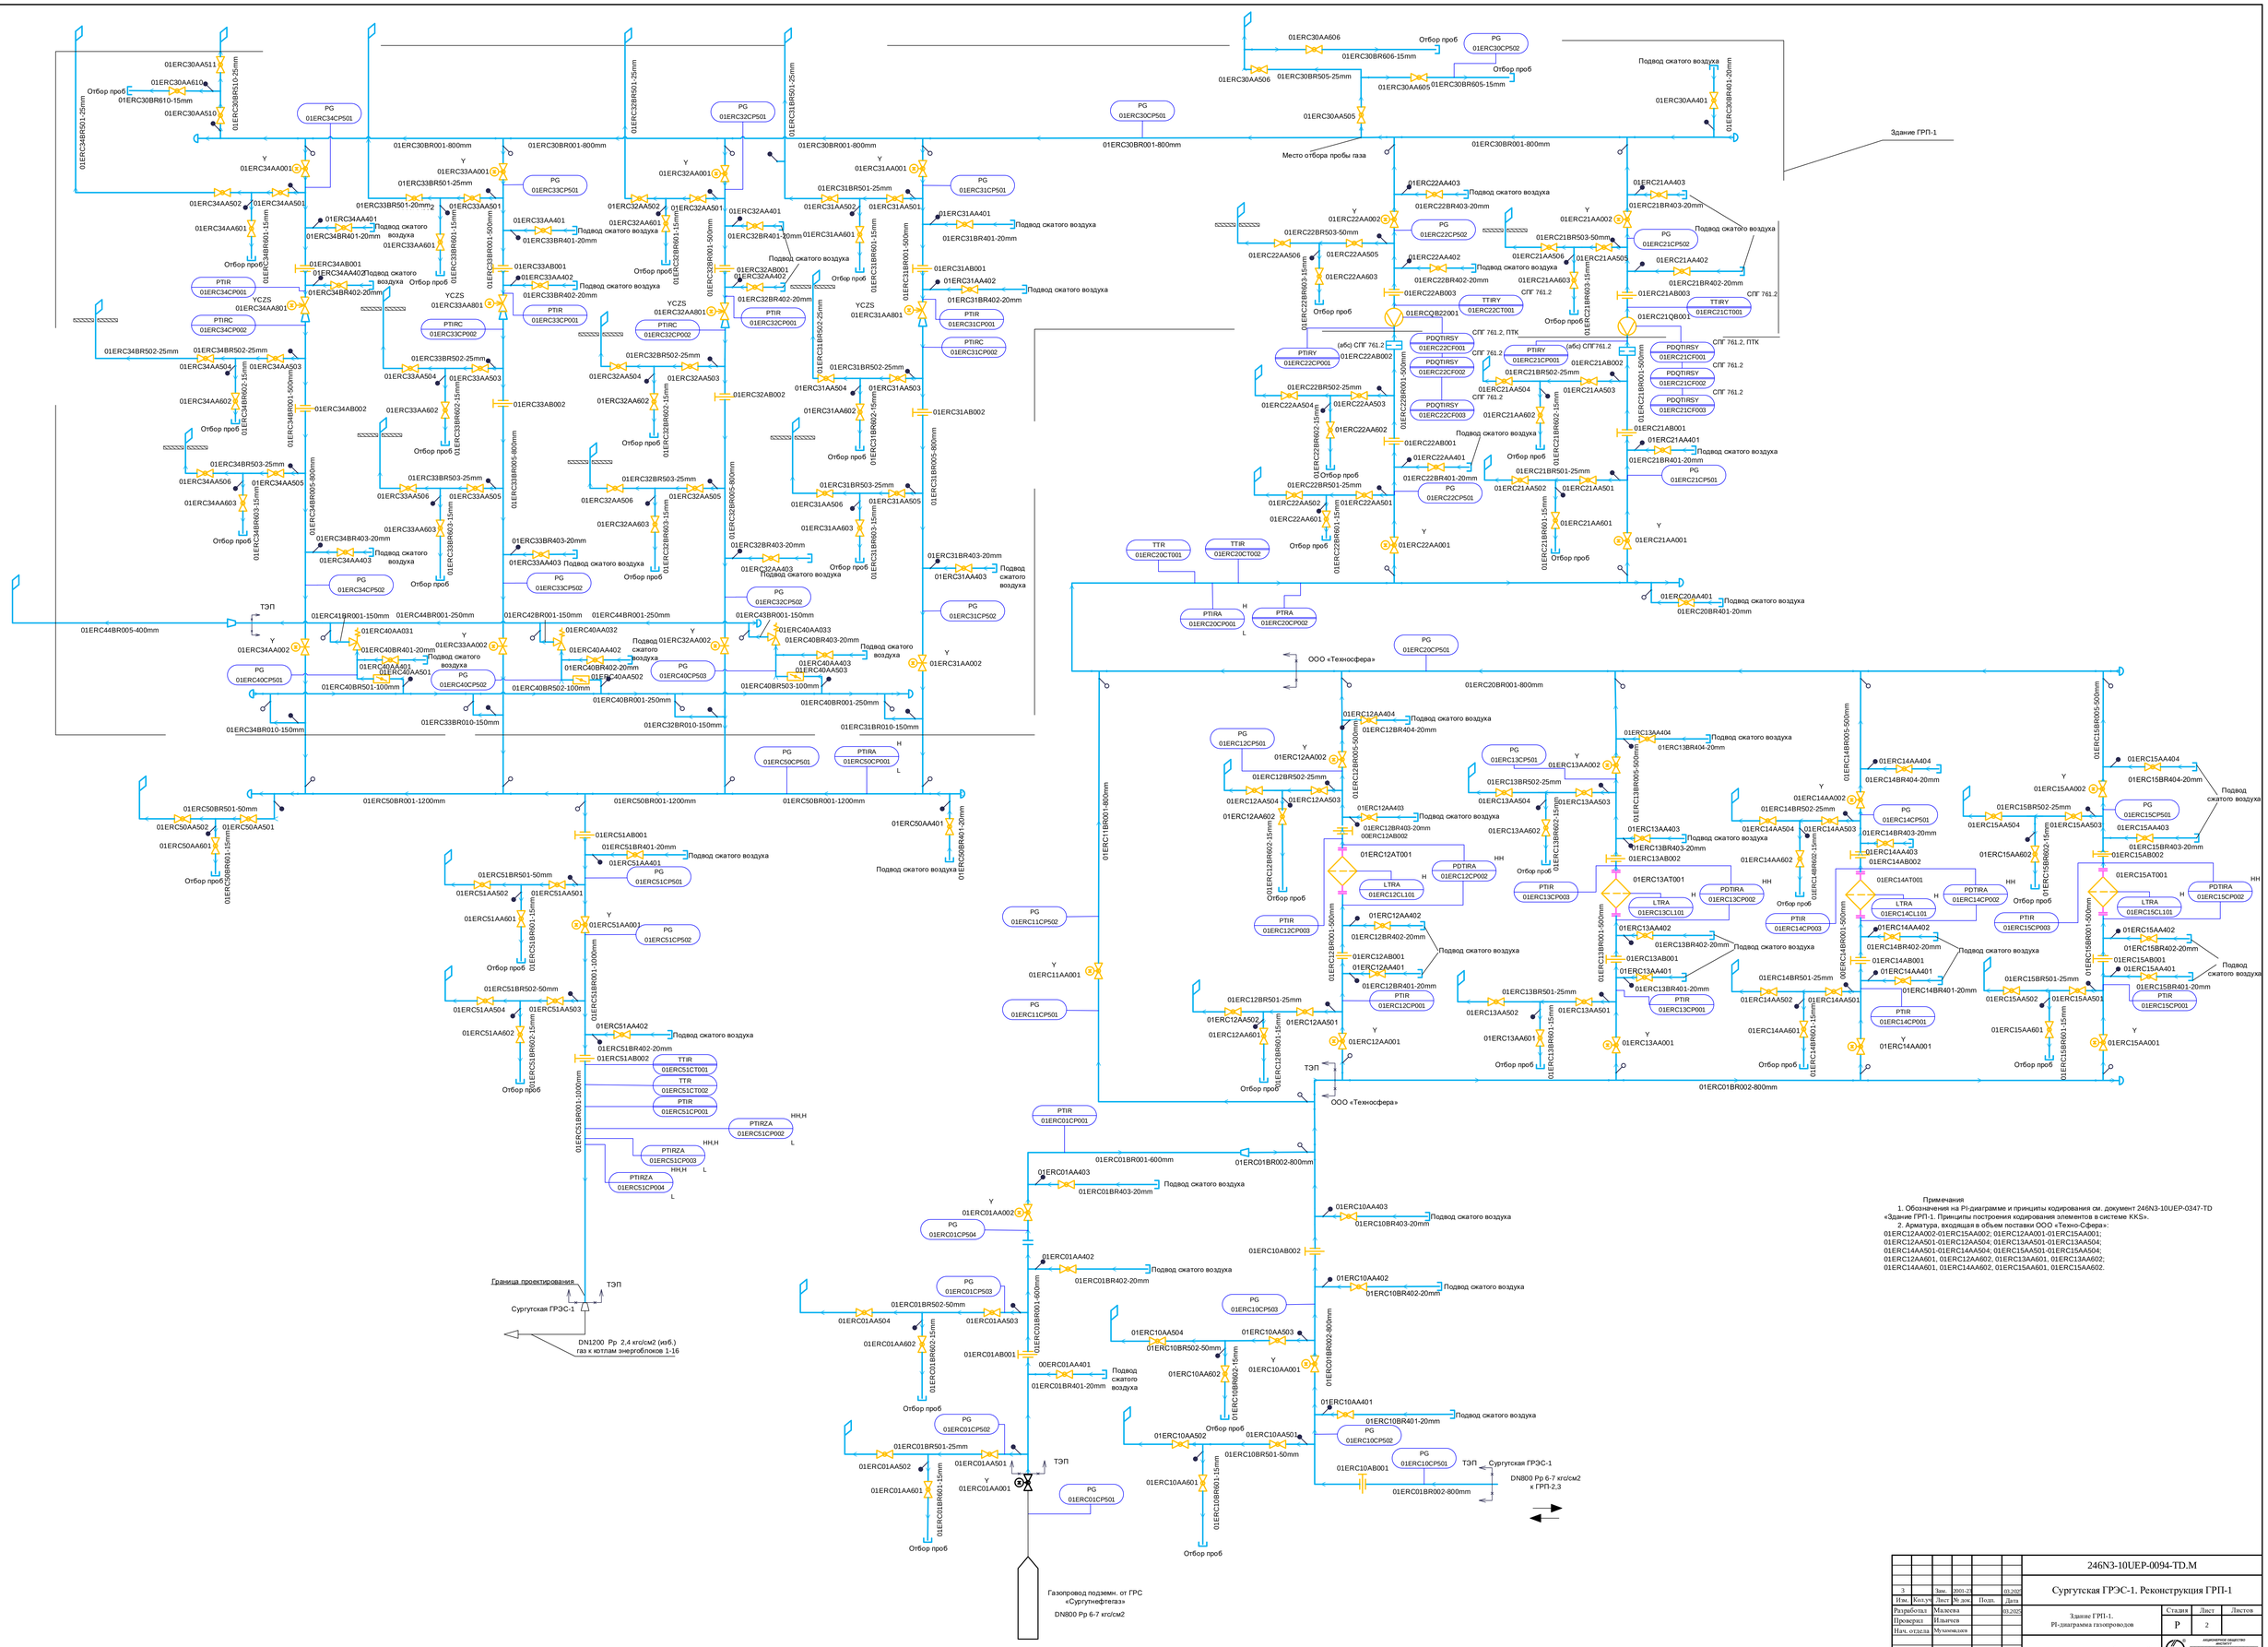

Примечания

1. Обозначения на PI-диаграмме и принципы кодирования см. документ 246N3-10UEP-0347-TD «Здание ГРП-1. Принципы построения кодирования элементов в системе KKS».
2. Арматура, входящая в объем поставки ООО «Техно-Сфера»:
01ERC12AA002-01ERC15AA002; 01ERC12AA001-01ERC15AA001;
01ERC12AA501-01ERC12AA504; 01ERC13AA501-01ERC13AA504;
01ERC14AA501-01ERC14AA504; 01ERC15AA501-01ERC15AA504;
01ERC12AA601, 01ERC12AA602, 01ERC13AA601, 01ERC13AA602;
01ERC14AA601, 01ERC14AA602, 01ERC15AA601, 01ERC15AA602.

3		Зам.	2001-22		03.2022	246N3-10UEP-0094-TD.M	
Изм.	Кол.уч.	Лист	№ док.	Подп.	Дата	Сургутская ГРЭС-1. Реконструкция ГРП-1	
Разработал		Малеева			03.2022	Здание ГРП-1. PI-диаграмма газопроводов	Стадия: Р; Лист: 2; Листов:
Проверил		Ильичев					
Нач. отдела		Мухомедьев					
Н. контр.		Майорова				PI-диаграмма газопроводов. Система ERC	АКЦИОНЕРНОЕ ОБЩЕСТВО «ВНИПИГАЗДОБЫЧА» ГАЗПРОМ

Согласовано: ОАСУ Захаров

Взам. инв. №

Подпись и дата

Инв. № подл.

Формат А0