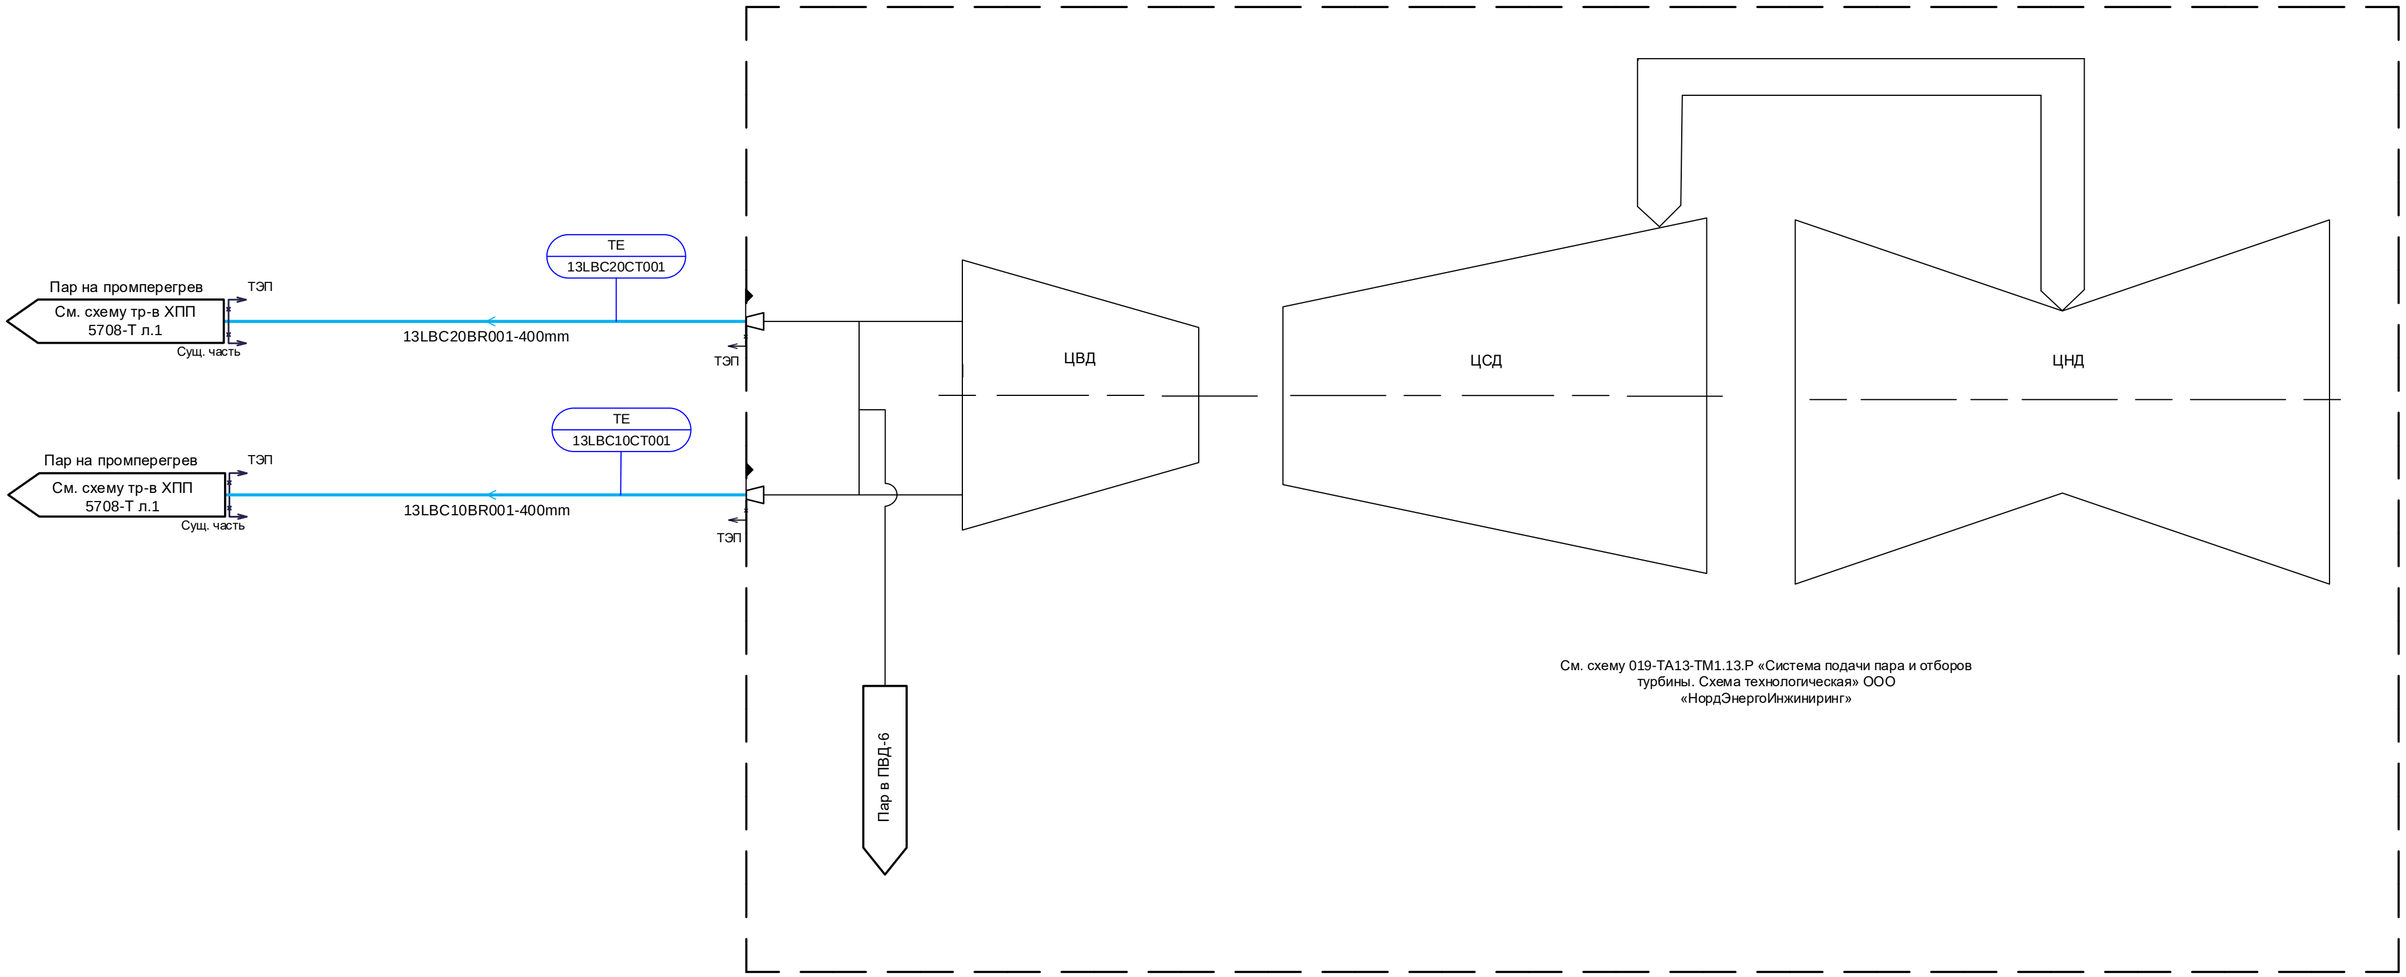

Существующая часть Сургутской ГРЭС-1

АО «Институт Теплоэлектропроект» (ТЭП)

- граница проектирования

АО «Силовые Машины» (СМ)

- граница проектирования

АО «Институт Теплоэлектропроект» (ТЭП)

Согласовано

ОАСУ

Взам. инв. №

Подпись и дата

Инв. № подл.

Изм.	Кол.уч	Лист	№ док.	Подп.	Дата
Разработал		Дёмина			
Проверил		Ястребов			
Н. контр.		Астраханцев			

246N28–13UHJ–1000–TD.M

Трубопроводы ХПП и ГПП за пределами ячейки блока 13г

Главный корпус. PI-диаграмма трубопроводов ХПП

Стадия	Лист	Листов
Р	2	

PI-диаграмма трубопроводов ХПП. Система LBC.

АКЦИОНЕРНОЕ ОБЩЕСТВО ИНСТИТУТ ТЕПЛОЭЛЕКТРОПРОЕКТ Г. МОСКВА

Формат А2