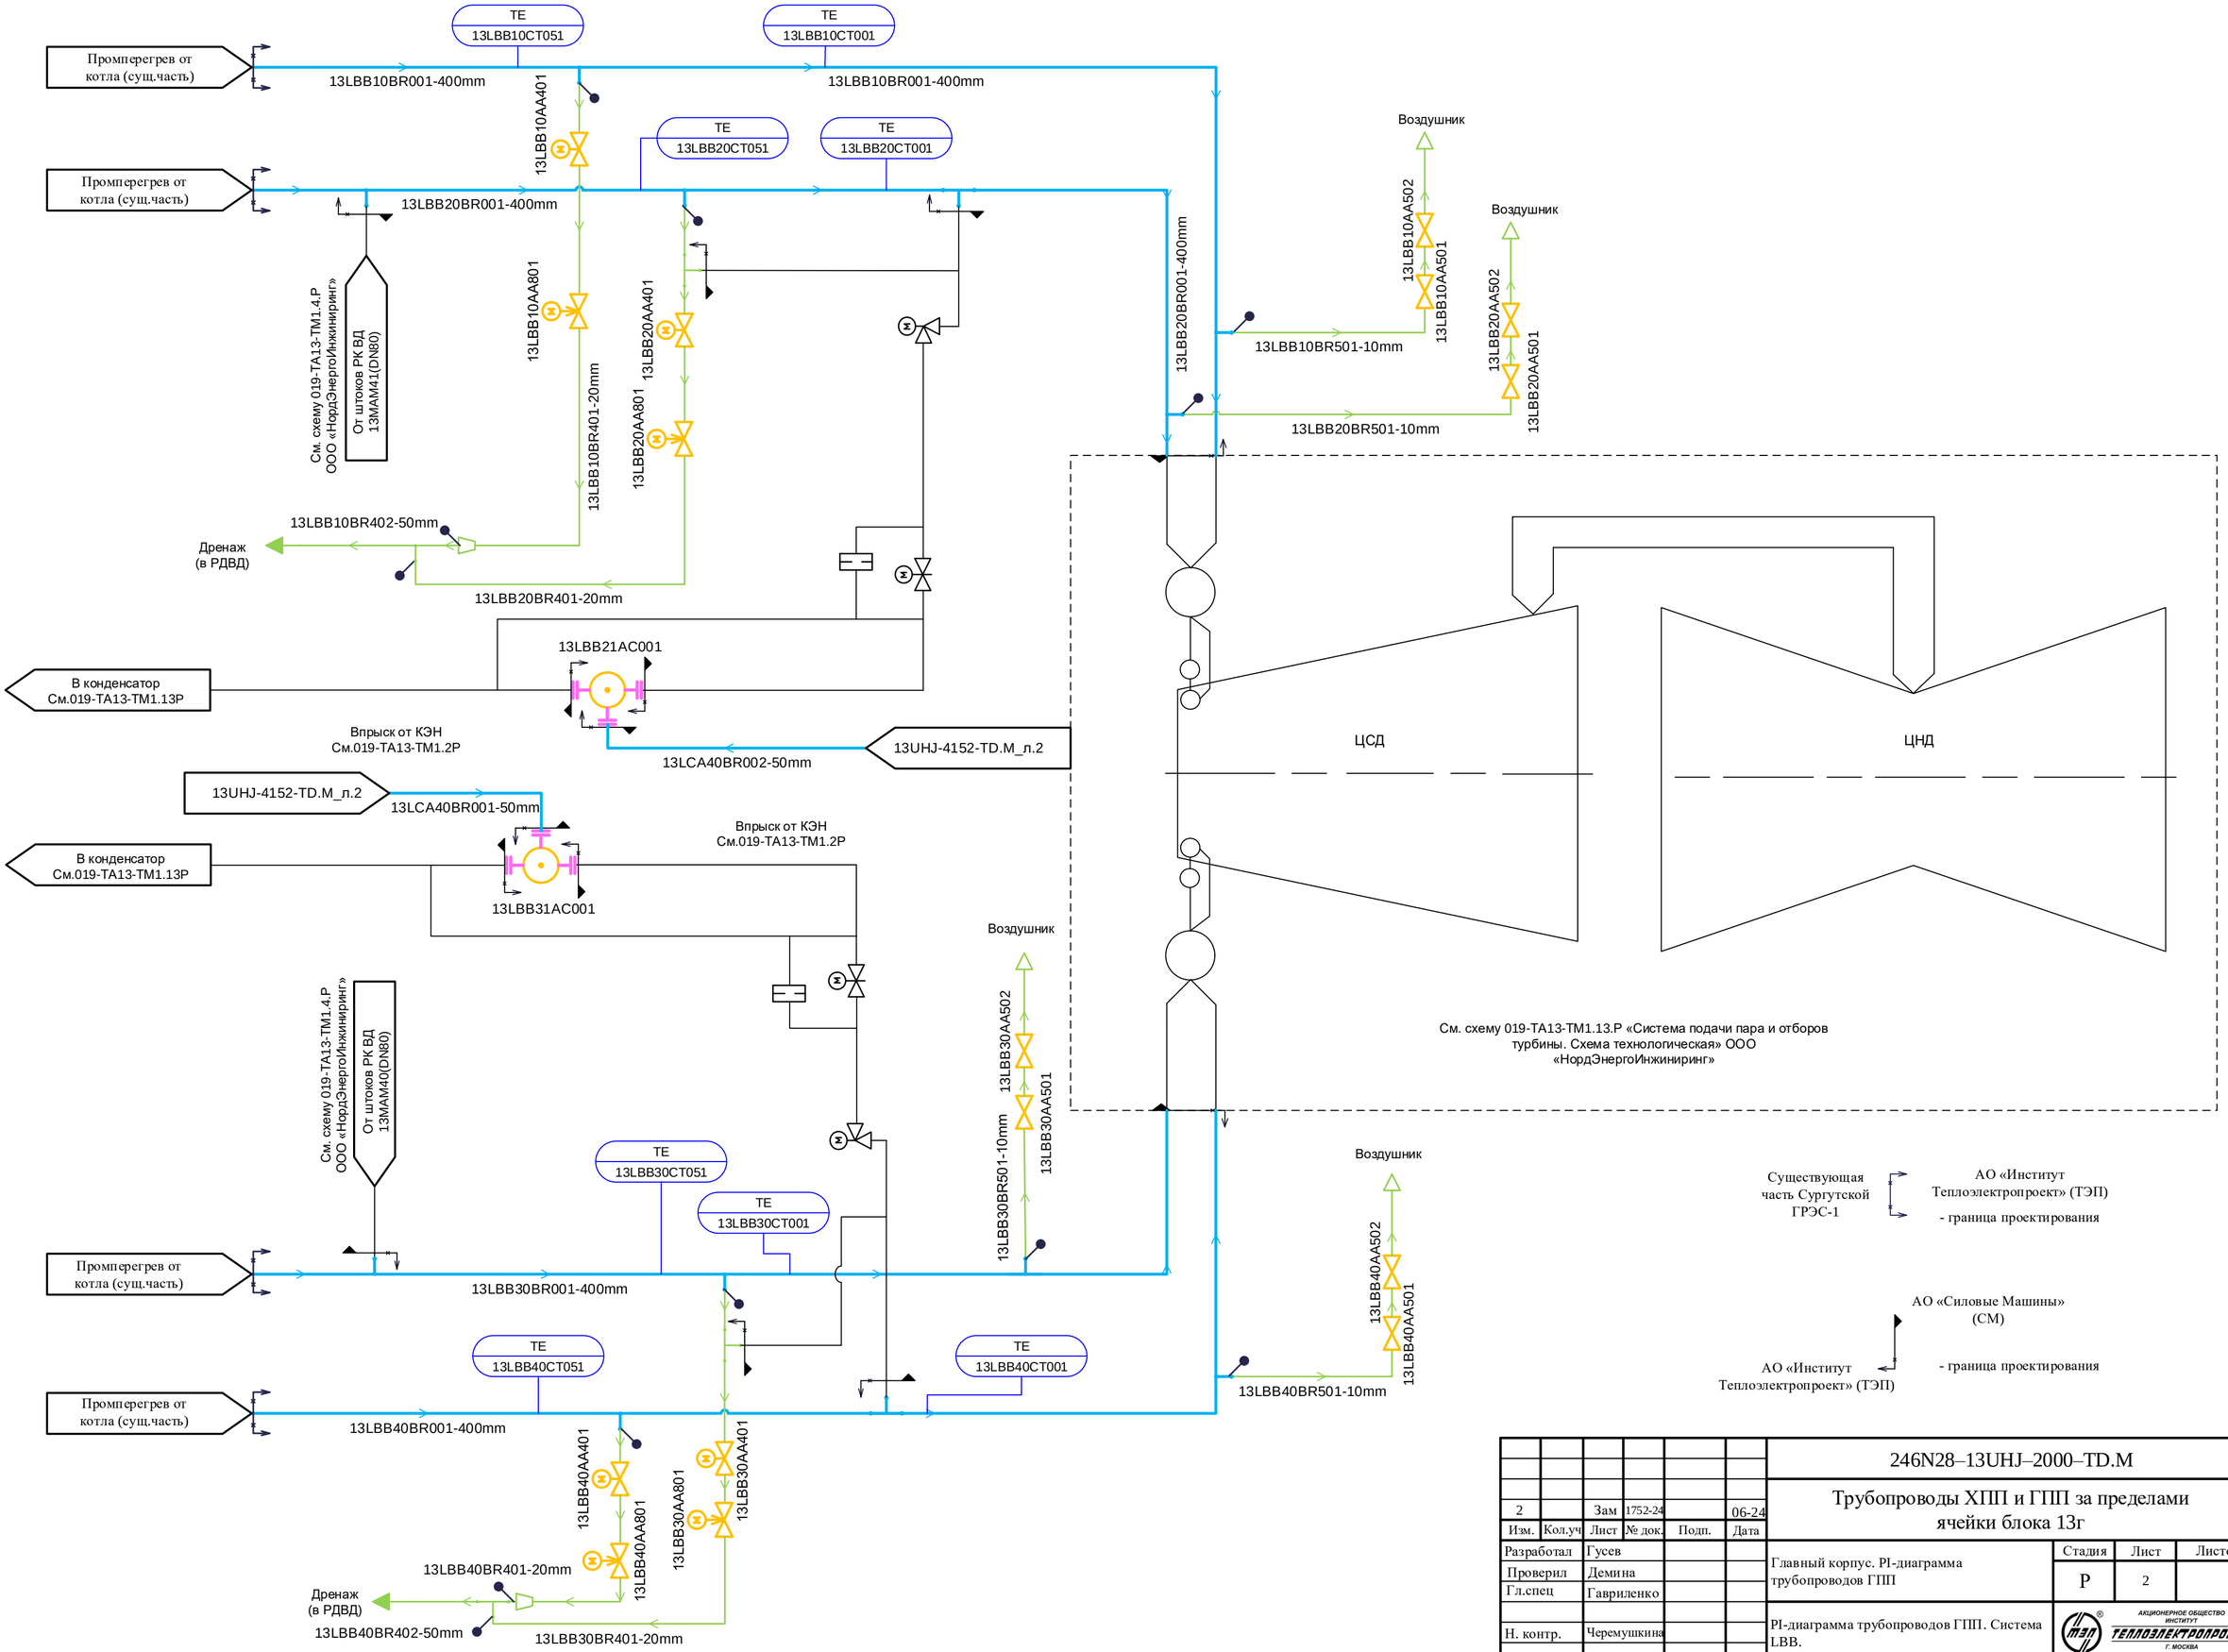

2		Зам	1752-24		06-24	246N28–13UHJ–2000–TD.M
Изм.	Кол.уч	Лист	№ док.	Подп.	Дата	Трубопроводы ХПП и ГПП за пределами ячейки блока 13г
Разработал		Гусев				Главный корпус. PI-диаграмма трубопроводов ГПП
Проверил		Демина				Стадия: Р; Лист: 2; Листов:
Гл.спец		Гавриленко				
Н. контр.		Черемушкина				PI-диаграмма трубопроводов ГПП. Система LBB.

АКЦИОНЕРНОЕ ОБЩЕСТВО ИНСТИТУТ ТЕПЛОЭЛЕКТРОПРОЕКТ Г. МОСКВА

Согласовано

Взам. инв. №

Подпись и дата

Инв. № подл.

Формат А2